

FACULTAD DE INGENIERIA
ESCUELA DE ARQUITECTURA

ASIGNATURA

DISEÑO V

ESTUDIANTE

SONIA RODRIGUEZ
2022-0336
MARIA ISABEL GRULLON
2022-0599

DOCENTE

JOSE ALBERTO DE LA CRUZ

SEMESTRE

2-2025

PROYECTO

HOTEL BOUTIQUE

CONTENIDO

INDICADO

ESCALA

INDICADA

PAGINA

PAC01

PLANTA ARQUITECTONICA DE CONJUNTO
HOTEL BOUTIQUE

ESC:1:850



FACULTAD DE INGENIERIA
ESCUELA DE ARQUITECTURA

ASIGNATURA

DISEÑO V

ESTUDIANTE

SONIA RODRIGUEZ
2022-0336
MARIA ISABEL GRULLON
2022-0599

DOCENTE

JOSE ALBERTO DE LA CRUZ

SEMESTRE

2-2025

PROYECTO

HOTEL BOUTIQUE

CONTENIDO

INDICADO

ESCALA


INDICADA

PAGINA

PAA01

LEYENDA

- | | |
|----------------------|----------------------|
| ① CHECK-IN CHECK-OUT | ⑦ ARCHIVOS |
| ② OFICINA GERENTE | ⑧ MALETERO |
| ③ CONTABILIDAD | ⑨ TIENDA |
| ④ RECURSOS HUMANOS | ⑩ CAFE |
| ⑤ BAÑOS - PANTRY | ⑪ BAÑOS |
| ⑥ CUARTO DE RED | ⑫ CUARTO DE LIMPIEZA |
| ⑬ PISO DE CRISTAL | |

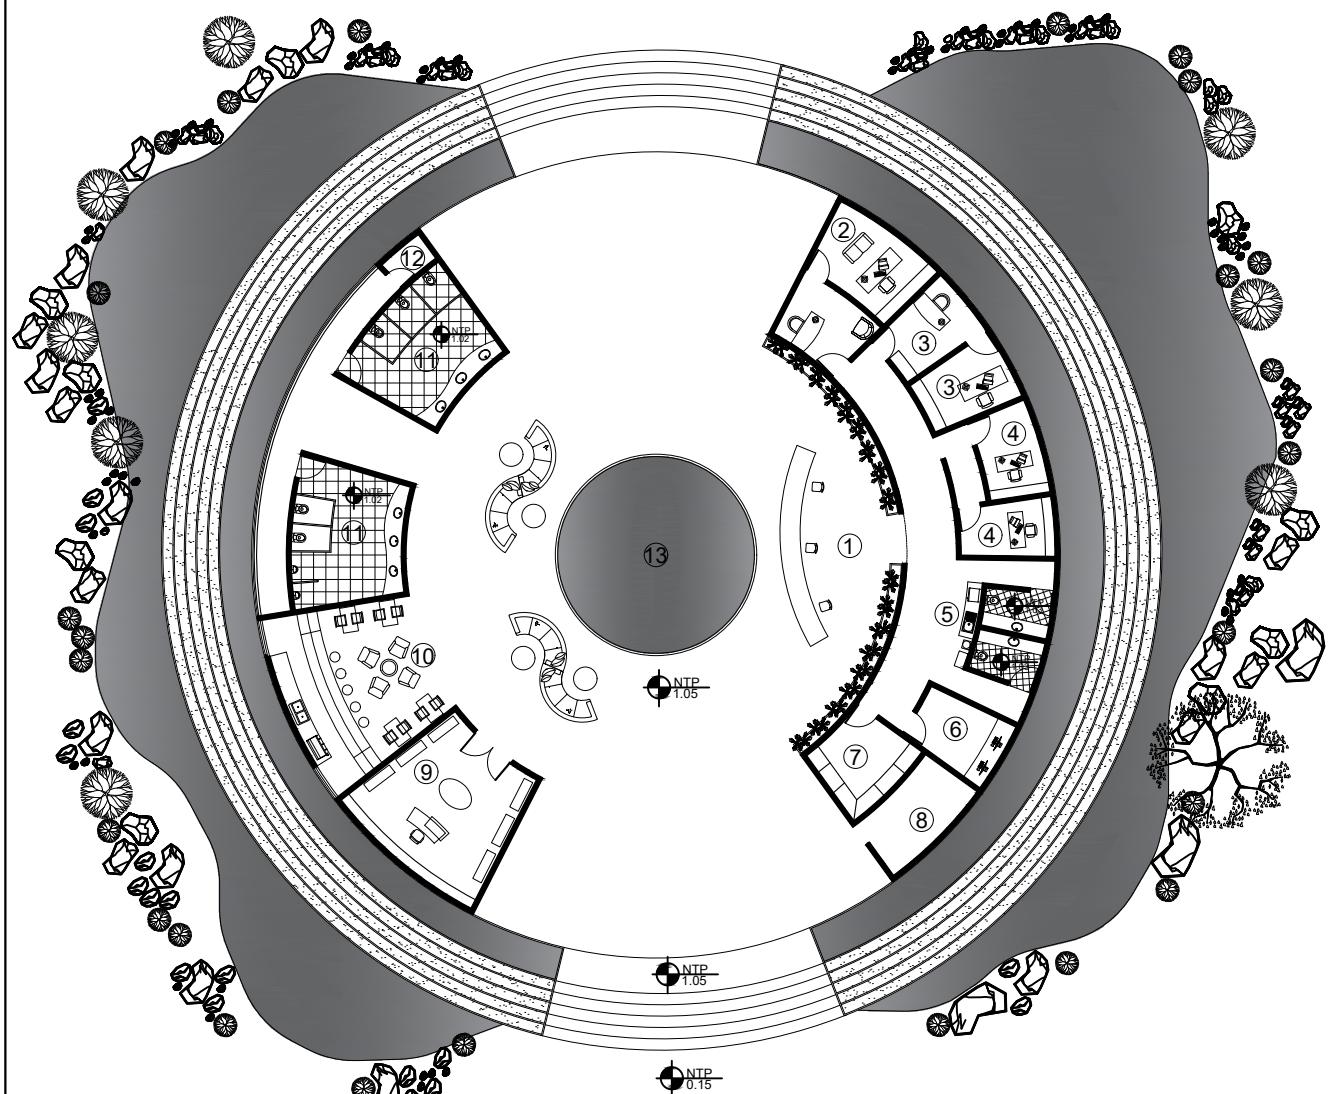


SIMBOLOGÍA DE MATERIALES

■ REVESTIMIENTO DE MADERA

LEYENDA

- | | |
|-----------------------|---------------|
| ① ÁREA COMÚN | ⑦ CAMILLAS |
| ② DORMITORIOS | ⑧ ALMACEN |
| ③ BAÑOS | ⑨ BAÑO |
| ④ DUCHAS - VESTUARIOS | ⑩ ROPA SUCIA |
| ⑤ COCINA | ⑪ ROPA LIMPIA |
| ⑥ ENFERMERÍA | ⑫ COMEDOR |

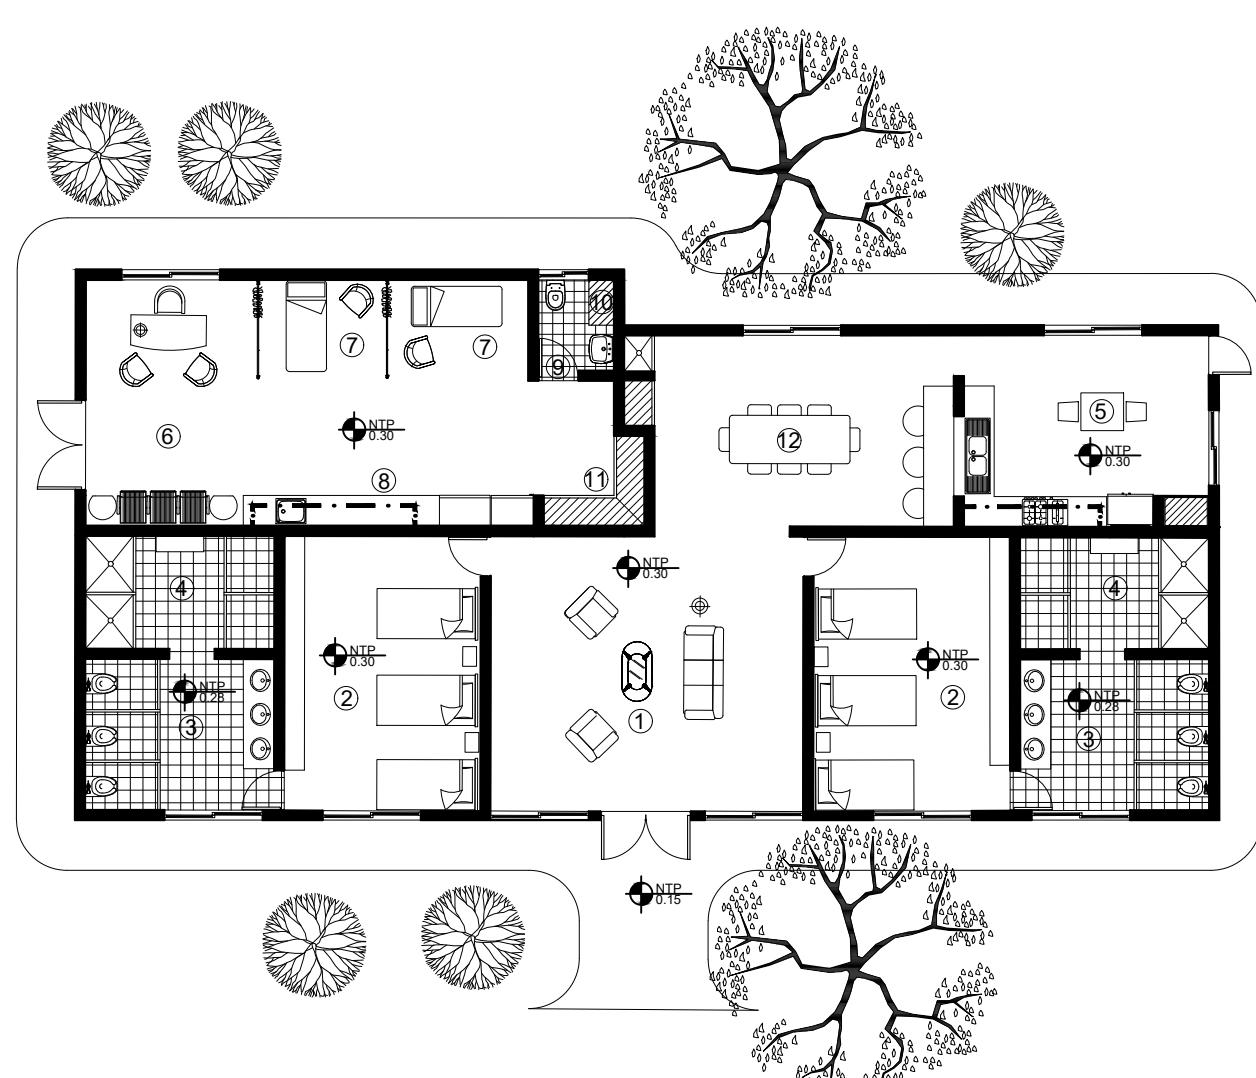

SIMBOLOGÍA DE MATERIALES

■ REVESTIMIENTO DE MADERA



FACULTAD DE INGENIERIA
ESCUELA DE ARQUITECTURA

ASIGNATURA

DISEÑO V

ESTUDIANTE

SONIA RODRIGUEZ
2022-0336
MARIA ISABEL GRULLON
2022-0599

DOCENTE

JOSE ALBERTO DE LA CRUZ

SEMESTRE

2-2025

PROYECTO

HOTEL BOUTIQUE

CONTENIDO

INDICADO

ESCALA


INDICADA

PAGINA

PAA02

LEYENDA

- ① KICHENETTE
- ② BAÑO
- ③ CLOSET
- ④ ESCALERA

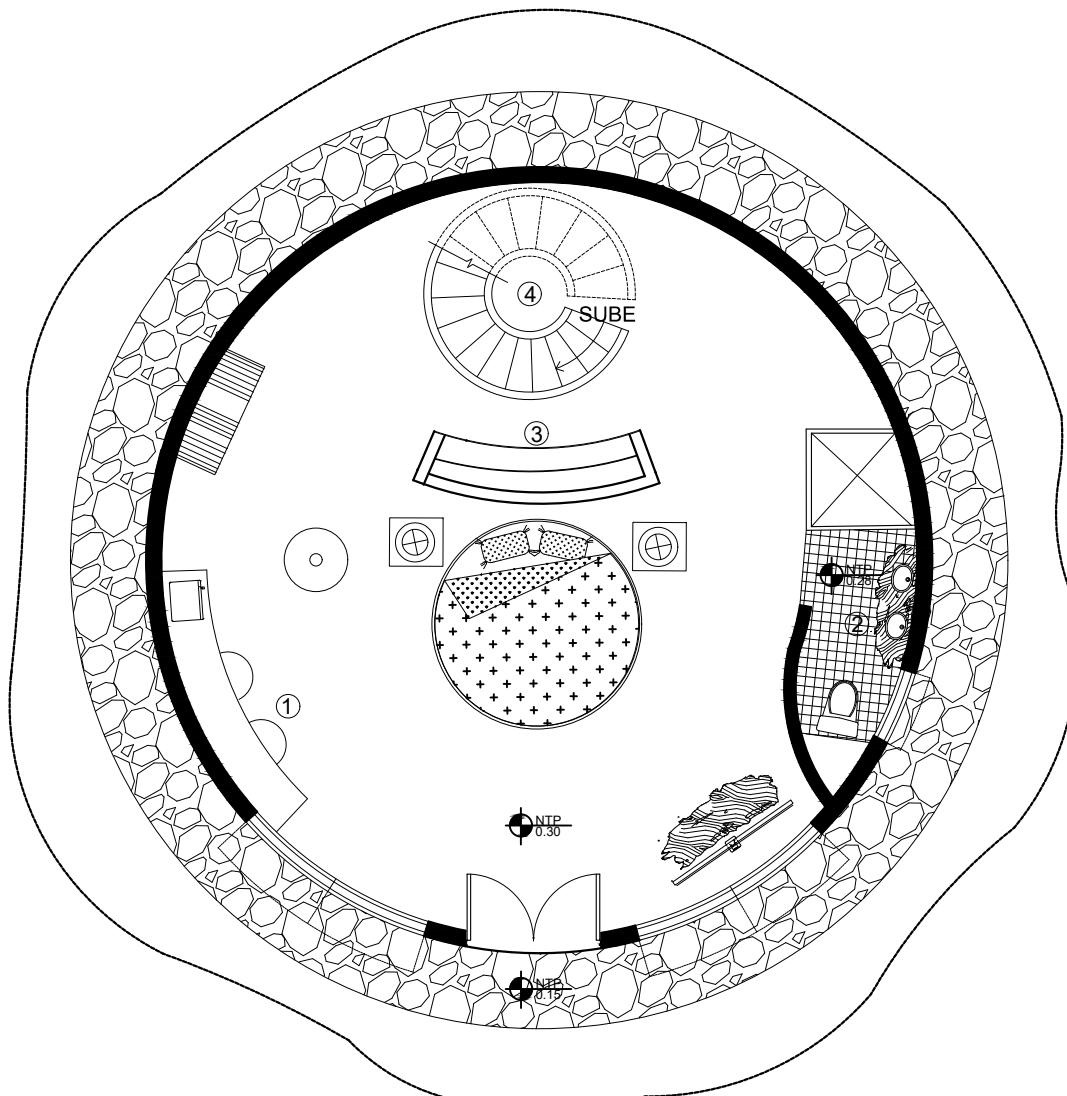

SIMBOLOGÍA DE MATERIALES


- REVESTIMIENTO DE MADERA

PLANTA ARQUITECTONICA AMUEBLADA
COCO SPLASH SUITE - 1ER NIVEL

ESC:1:100

LEYENDA

- ① ESCALERA
- ② CAMA
- ③ BAÑO

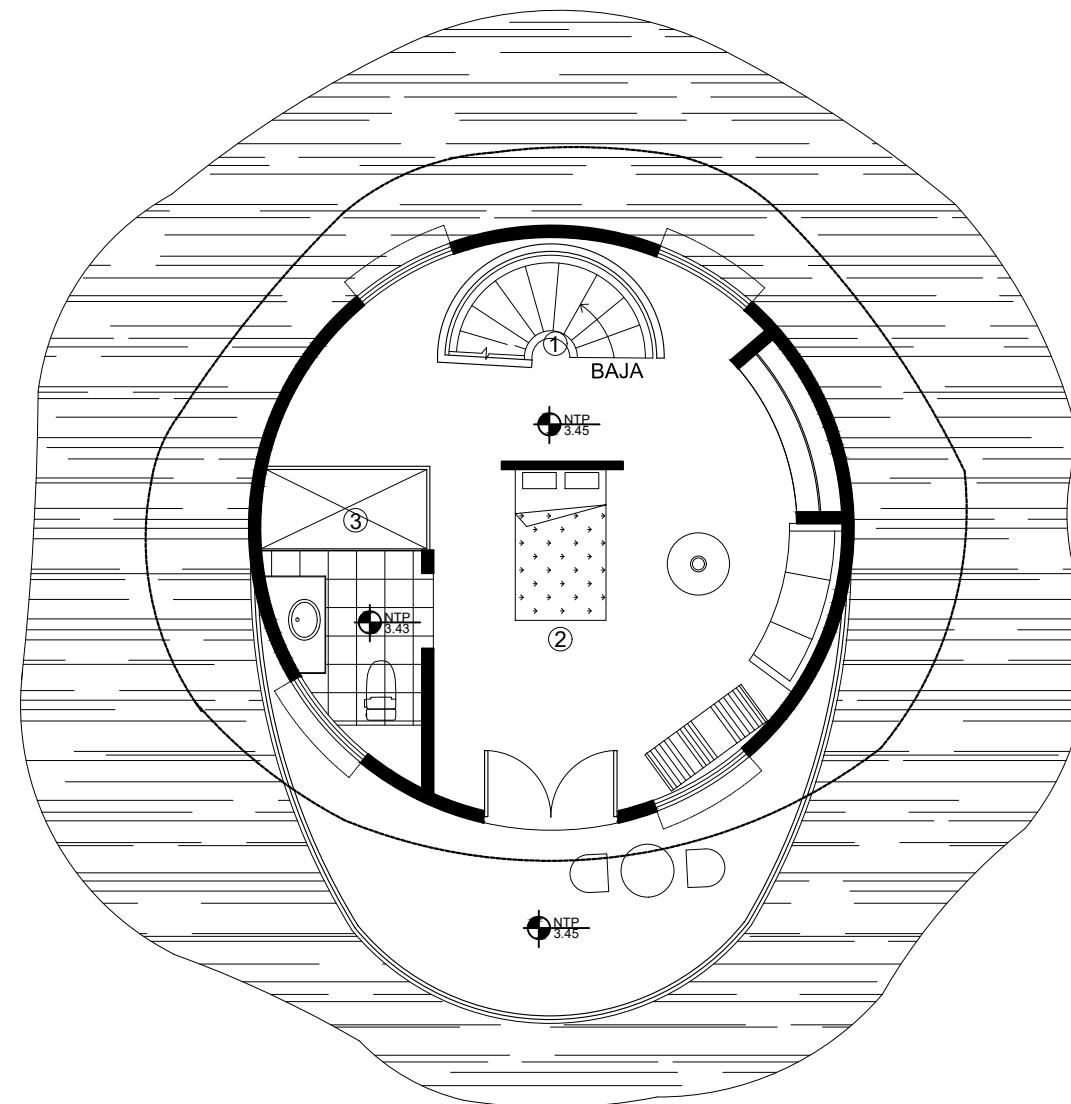

SIMBOLOGÍA DE MATERIALES

- REVESTIMIENTO DE MADERA

PLANTA ARQUITECTONICA AMUEBLADA
COCO SPLASH SUITE - 2DO NIVEL

ESC:1:100



FACULTAD DE INGENIERIA
ESCUELA DE ARQUITECTURA

ASIGNATURA

DISEÑO V

ESTUDIANTE

SONIA RODRIGUEZ
2022-0336
MARIA ISABEL GRULLON
2022-0599

DOCENTE

JOSE ALBERTO DE LA CRUZ

SEMESTRE

2-2025

PROYECTO

HOTEL BOUTIQUE

CONTENIDO

INDICADO

ESCALA


INDICADA

PAGINA

PAA03

LEYENDA

- ① TINA
- ② ESCALERAS

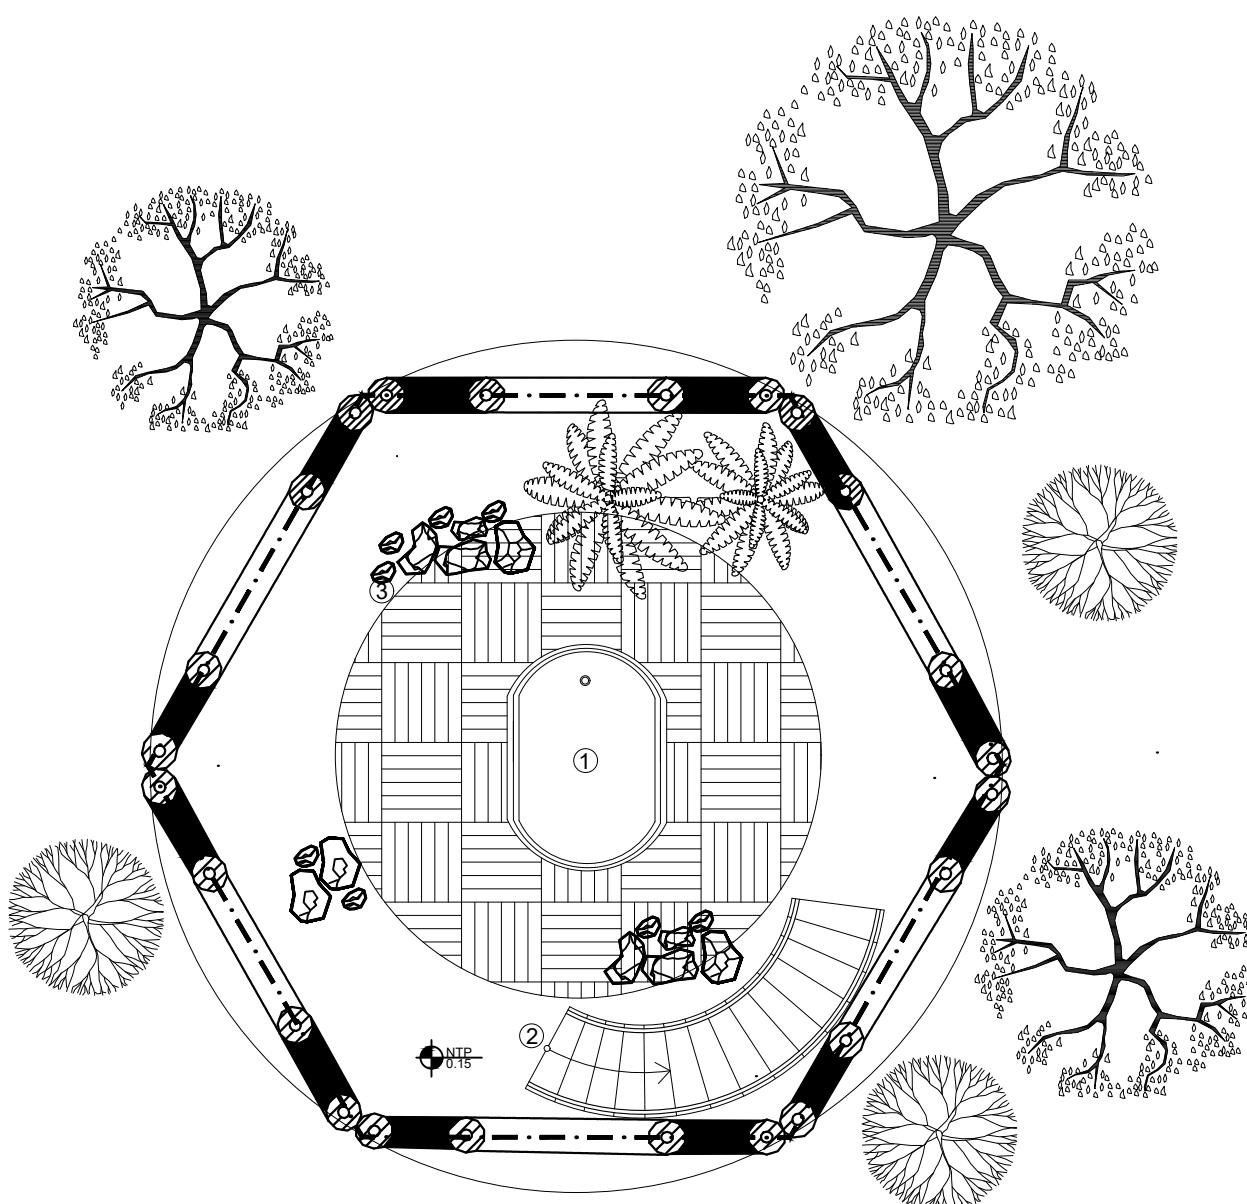

SIMBOLOGÍA DE MATERIALES


■ REVESTIMIENTO DE MADERA

PLANTA ARQUITECTONICA AMUEBLADA
PALMA DE COCO SUITE - 1ER NIVEL

ESC:1:100

LEYENDA

- ① POLE DANCE
- ② CLOSET
- ③ BAÑO
- ④ KICHENNETE
- ⑤ BALCÓN
- ⑥ ESCALERAS

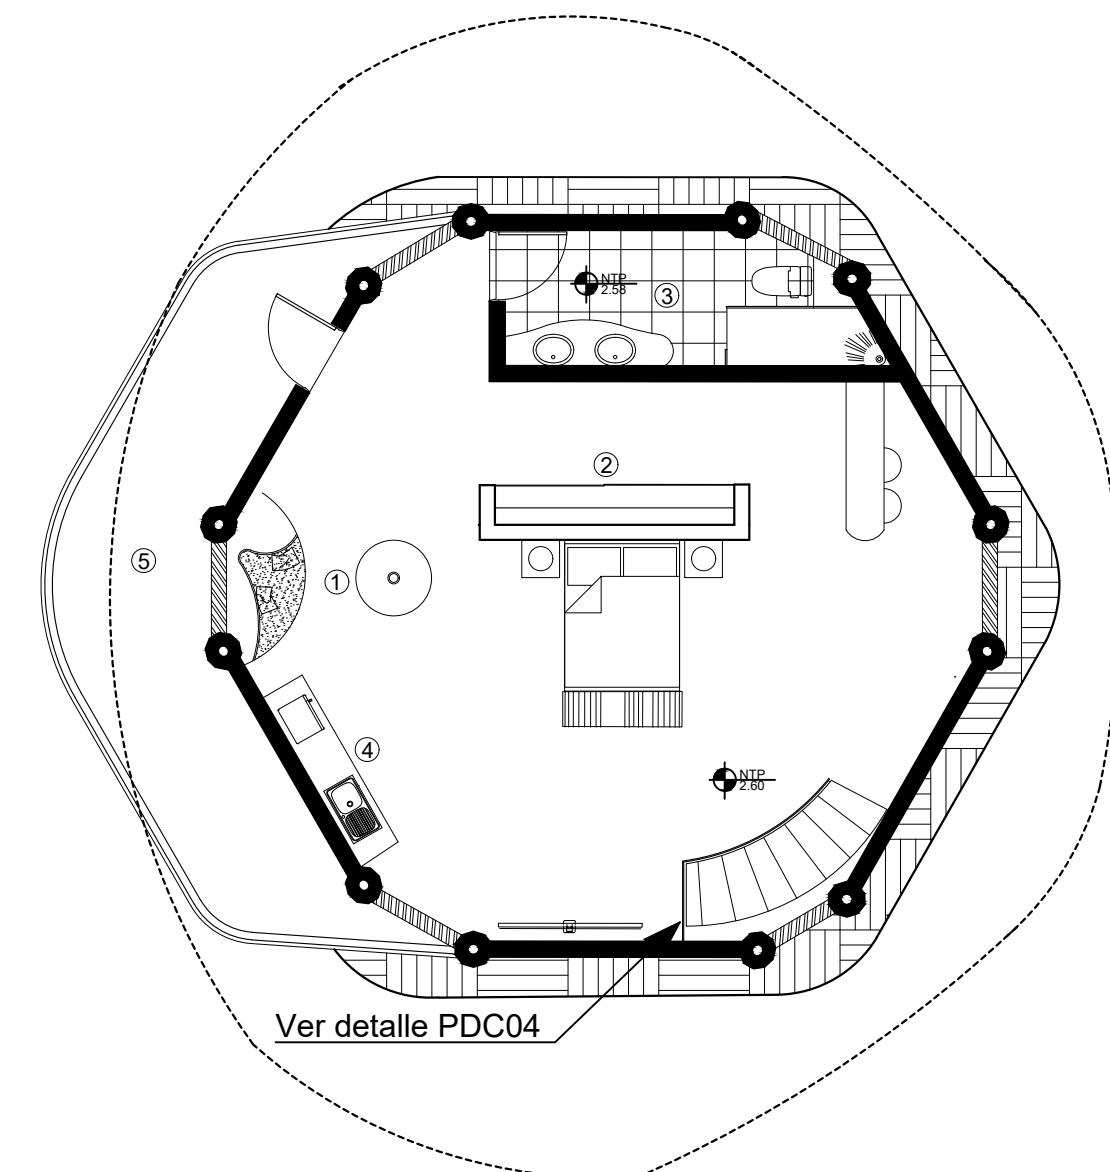

SIMBOLOGÍA DE MATERIALES

■ REVESTIMIENTO DE MADERA

PLANTA ARQUITECTONICA AMUEBLADA
PALMA DE COCO SUITE - 2DO NIVEL

ESC:1:100

PAA03



FACULTAD DE INGENIERIA
ESCUELA DE ARQUITECTURA

ASIGNATURA

DISEÑO V

ESTUDIANTE

SONIA RODRIGUEZ
2022-0336
MARIA ISABEL GRULLON
2022-0599

DOCENTE

JOSE ALBERTO DE LA CRUZ

SEMESTRE

2-2025

PROYECTO

HOTEL BOUTIQUE

CONTENIDO

INDICADO

ESCALA

INDICADA


PAGINA

PAA04

LEYENDA

- ① CLOSET
- ② BAÑO
- ③ KICHENNTE
- ④ TERRAZA

Ver detalle PDC03

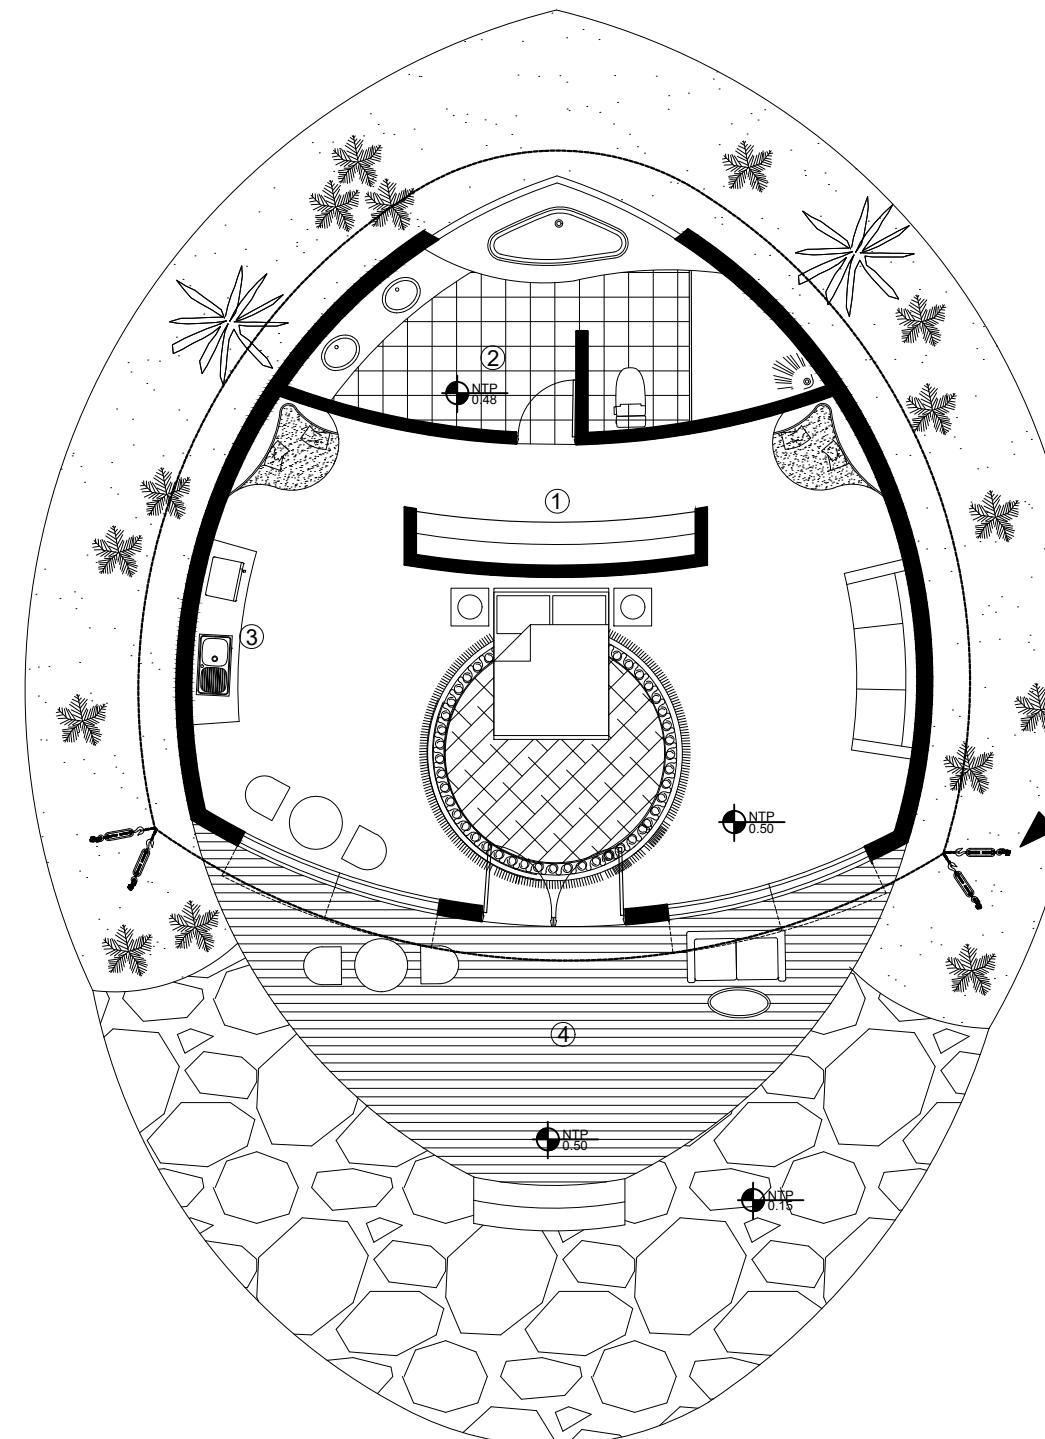


SIMBOLOGÍA DE MATERIALES

- REVESTIMIENTO DE MADERA

LEYENDA

- | | |
|--------------------------|---------------------------|
| ① ESTACIONES | ⑨ OFICINA DEL CHEF |
| ② BAÑOS CLIENTES | ⑩ ALMACEN DIARIO |
| ③ PANADERIA Y REPOSTERIA | ⑪ PREPARACION |
| ④ FRITURA Y EMPANIZADO | ⑫ LAVADO |
| ⑤ BAÑOS EMPLEADOS | ⑬ OFICINA GERENTE ALMACEN |
| ⑥ CASILLEROS | ⑭ ALMACEN GENERAL |
| ⑦ COMEDOR | ⑮ ROPA BLANCA |
| ⑧ ALMACEN DE LIMPIEZA | ⑯ SUMINISTROS GENERALES |
| | ⑰ LIMPIEZA |

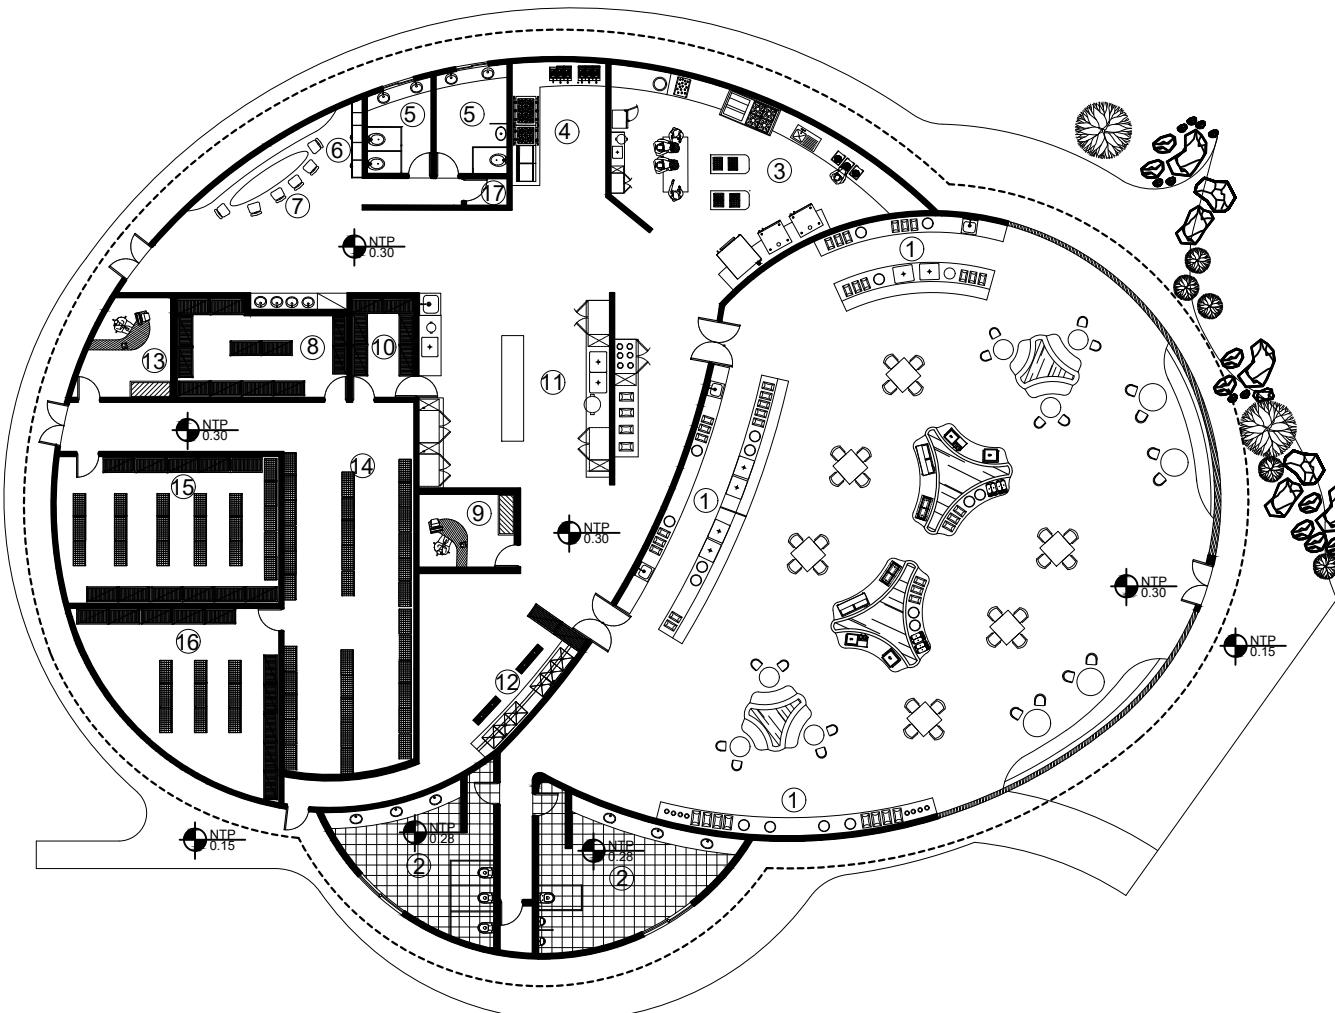


SIMBOLOGÍA DE MATERIALES

REVESTIMIENTO DE MADERA

LEYENDA

- | |
|-----------------------|
| ① ÁREA DE MESAS |
| ② BAR |
| ③ TERRAZA |
| ④ ALMACEN DIARIO |
| ⑤ ÁREA DE LAVADO |
| ⑥ ZONA DE PREPARACIÓN |
| ⑦ COMEDOR |
| ⑧ CASILLEROS |
| ⑨ BAÑOS EMPLEADOS |
| ⑩ BAÑOS CLIENTES |
| ⑪ LIMPIEZA |

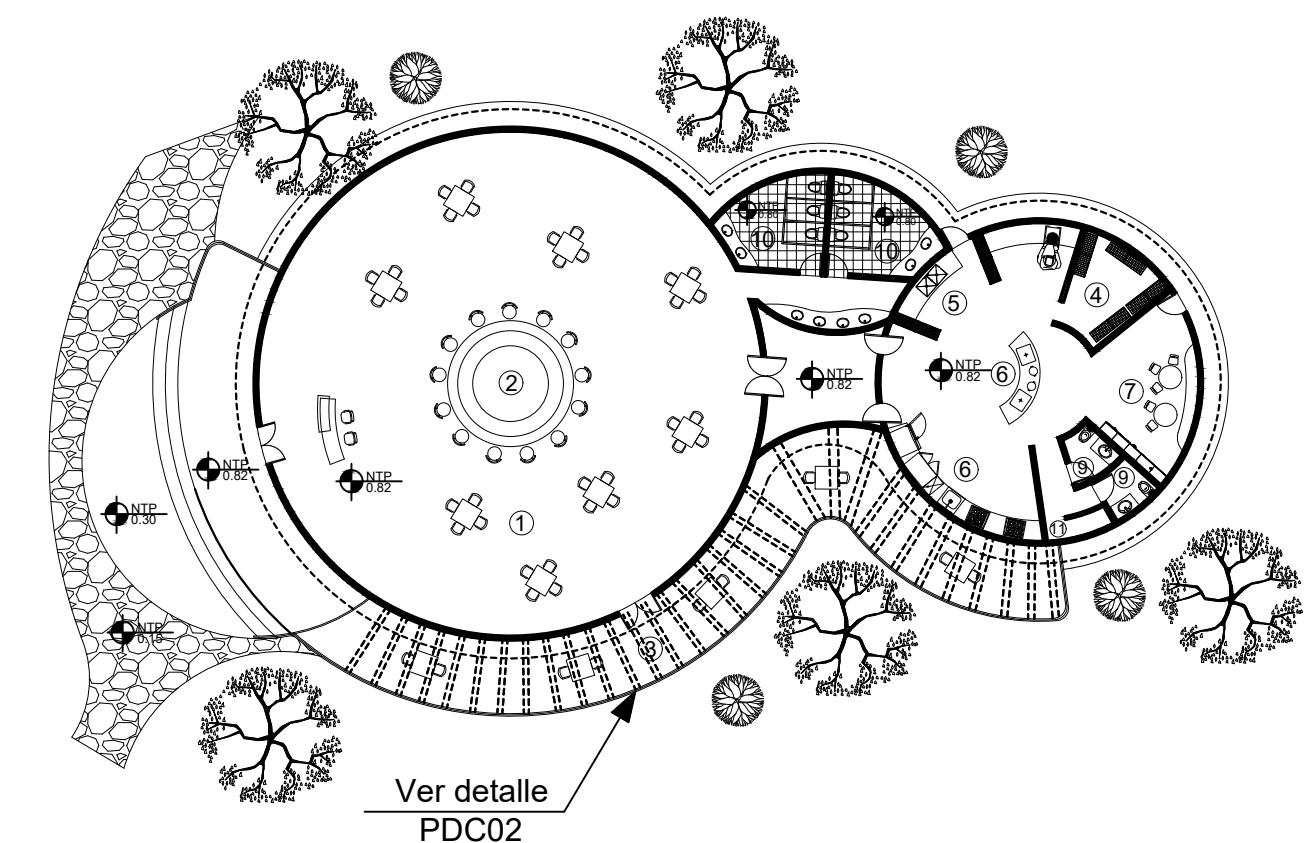

SIMBOLOGÍA DE MATERIALES

REVESTIMIENTO DE MADERA



FACULTAD DE INGENIERIA
ESCUELA DE ARQUITECTURA

ASIGNATURA

DISEÑO V

ESTUDIANTE

SONIA RODRIGUEZ
2022-0336
MARIA ISABEL GRULLON
2022-0599

DOCENTE

JOSE ALBERTO DE LA CRUZ

SEMESTRE

2-2025

PROYECTO

HOTEL BOUTIQUE

CONTENIDO

INDICADO

ESCALA

INDICADA

PAGINA

PAA05



FACULTAD DE INGENIERIA
ESCUELA DE ARQUITECTURA

ASIGNATURA

DISEÑO V

ESTUDIANTE

SONIA RODRIGUEZ
2022-0336
MARIA ISABEL GRULLON
2022-0599

DOCENTE

JOSE ALBERTO DE LA CRUZ

SEMESTRE

2-2025

PROYECTO

HOTEL BOUTIQUE

CONTENIDO

INDICADO

ESCALA


INDICADA

PAGINA

PAA06

LEYENDA

- ① ESCENARIO
- ② ÁREA DE MESAS
- ③ BARRA

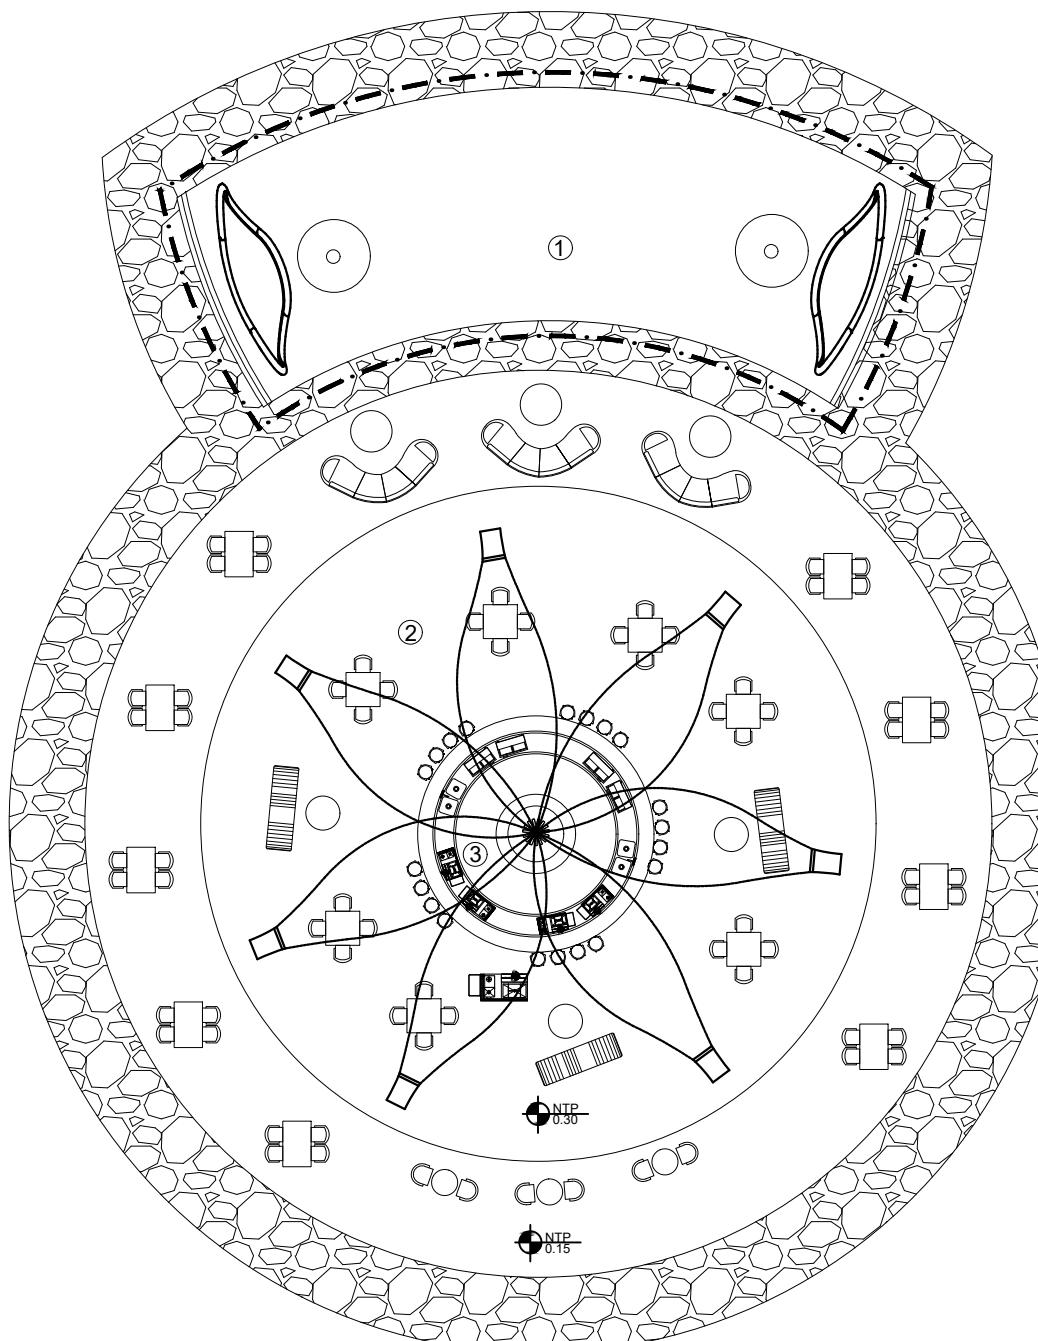


SIMBOLOGÍA DE MATERIALES

■ REVESTIMIENTO DE MADERA

LEYENDA

- ① RECEPCIÓN
- ② BAR
- ③ CAMERINOS
- ④ ALMACEN
- ⑤ SHIBARI
- ⑥ BONDAGE
- ⑦ SALA DE ROL
- ⑧ ALMACEN
- ⑨ BAÑOS

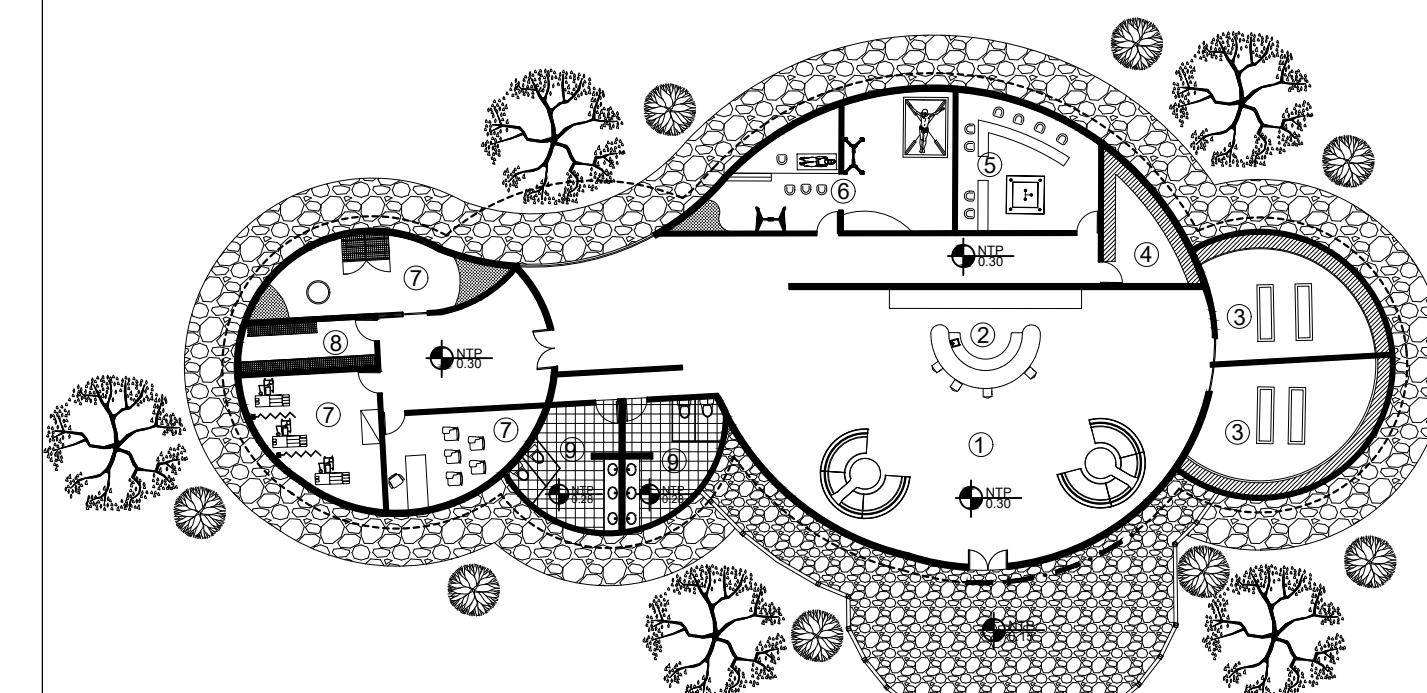

SIMBOLOGÍA DE MATERIALES

■ REVESTIMIENTO DE MADERA



FACULTAD DE INGENIERIA
ESCUELA DE ARQUITECTURA

ASIGNATURA

DISEÑO V

ESTUDIANTE

SONIA RODRIGUEZ
2022-0336
MARIA ISABEL GRULLON
2022-0599

DOCENTE

JOSE ALBERTO DE LA CRUZ

SEMESTRE

2-2025

PROYECTO

HOTEL BOUTIQUE

CONTENIDO

INDICADO

ESCALA


INDICADA

PAGINA

PAA07


LEYENDA

- ① RECEPCIÓN
- ② ROPA LIMPIA - ROPA SUCIA
- ③ VESTIDOR
- ④ MASAJES INDIVIDUALES
- ⑤ CLASE DE MASAJES EROTICOS
- ⑥ SAUNA
- ⑦ BAÑOS
- ⑧ JARDIN INTERIOR

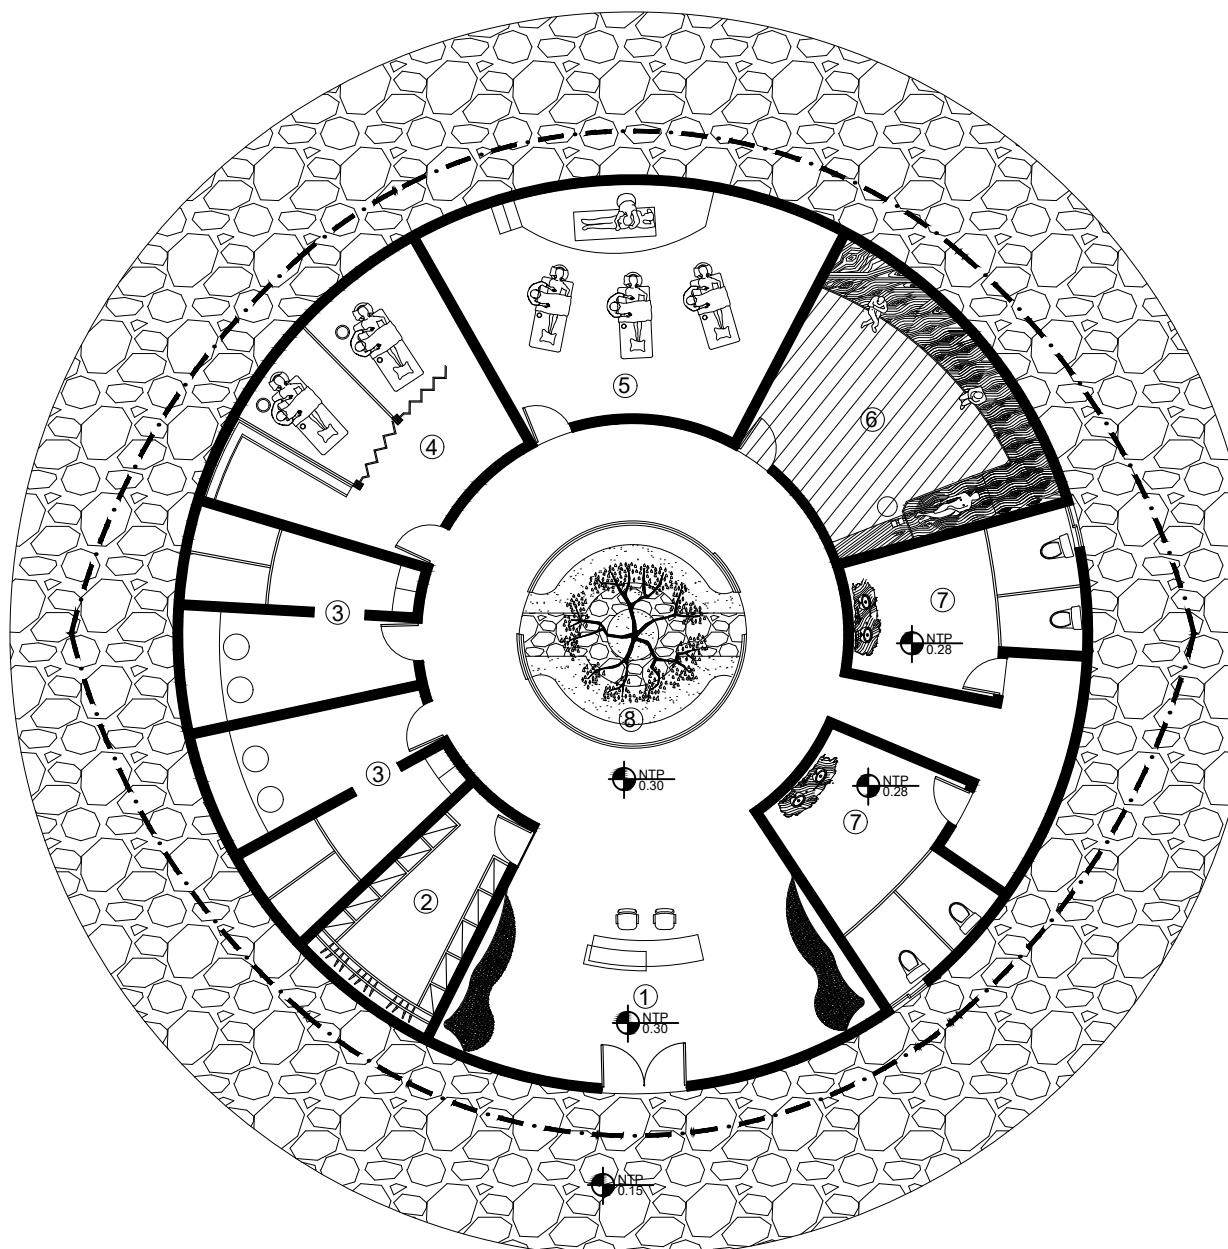

SIMBOLOGÍA DE MATERIALES

■ REVESTIMIENTO DE MADERA

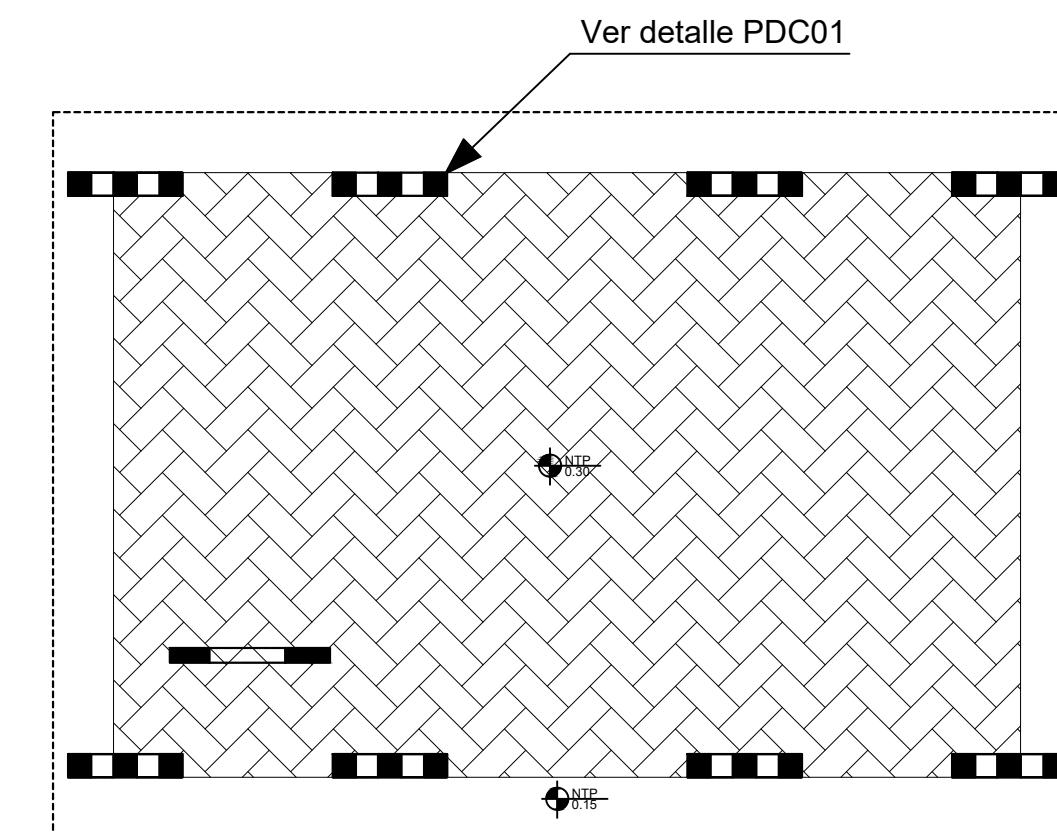

SIMBOLOGÍA DE MATERIALES


■ REVESTIMIENTO DE MADERA

NOTA

El edificio consta de dos niveles. Sin embargo, el primer nivel se ha diseñado con doble altura (6.5M), lo que permite alojar los tanques elevados a una altura equivalente a un tercer nivel. Esta disposición garantiza la presión y distribución adecuada del agua tratada hacia todas las áreas del proyecto.

LEYENDA

- ① BOMBAS DE AGUA
- ② FILTROS DE AGUA
- ③ ESCALERAS
- ④ POZO TUBULAR
- ⑤ CALENTADORES DE AGUA

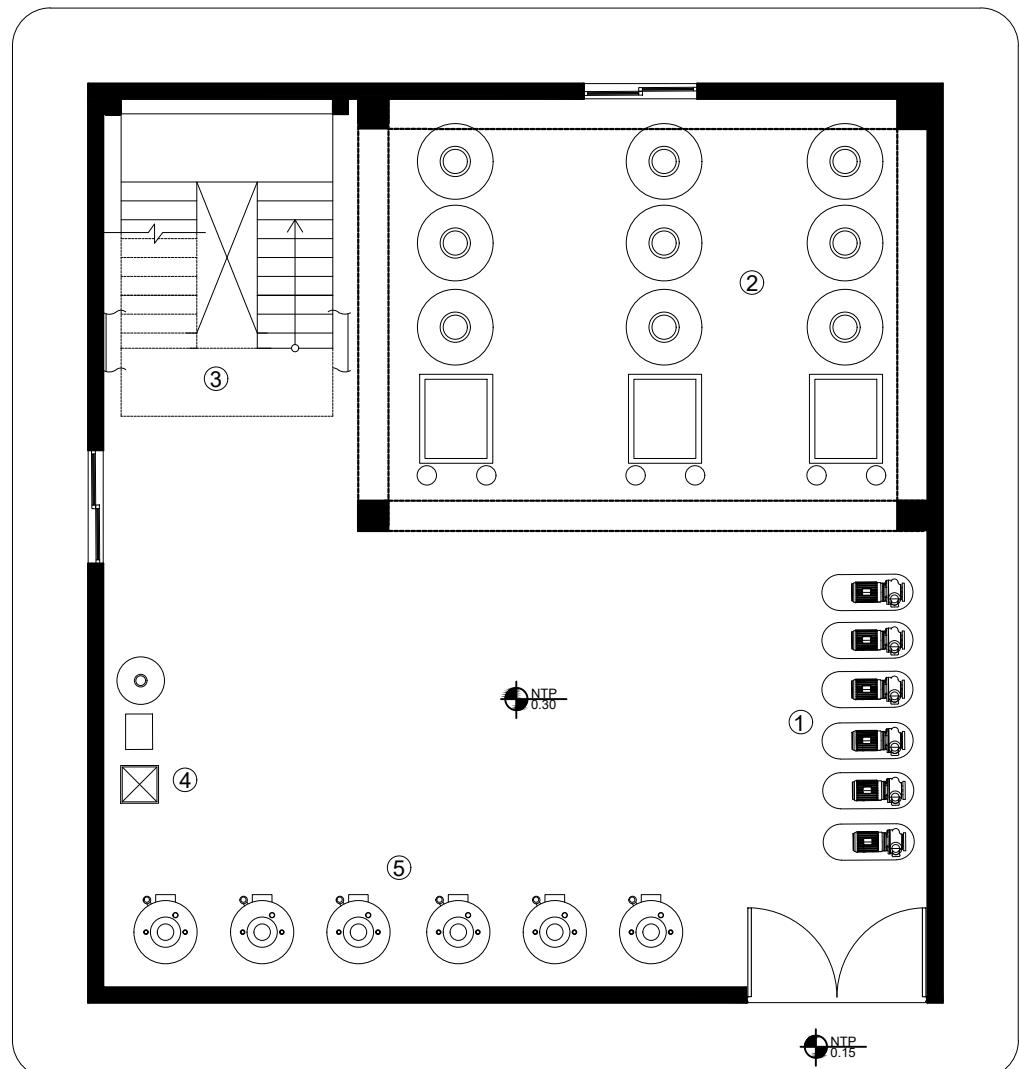


SIMBOLOGÍA DE MATERIALES

REVESTIMIENTO DE MADERA

LEYENDA

- ① TANQUES ELEVADOS

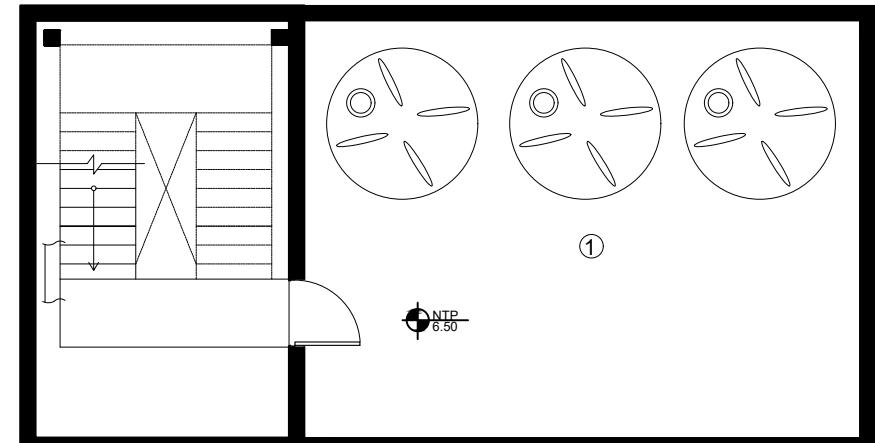

SIMBOLOGÍA DE MATERIALES

REVESTIMIENTO DE MADERA



FACULTAD DE INGENIERIA
ESCUELA DE ARQUITECTURA

ASIGNATURA

DISEÑO V

ESTUDIANTE

SONIA RODRIGUEZ
2022-0336
MARIA ISABEL GRULLON
2022-0599

DOCENTE

JOSE ALBERTO DE LA CRUZ

SEMESTRE

2-2025

PROYECTO

HOTEL BOUTIQUE

CONTENIDO

INDICADO

ESCALA

INDICADA

PAGINA

PAA08



FACULTAD DE INGENIERIA
ESCUELA DE ARQUITECTURA

ASIGNATURA

DISEÑO V

ESTUDIANTE

SONIA RODRIGUEZ
2022-0336
MARIA ISABEL GRULLON
2022-0599

DOCENTE

JOSE ALBERTO DE LA CRUZ

SEMESTRE

2-2025

PROYECTO

HOTEL BOUTIQUE

CONTENIDO

INDICADO

ESCALA


INDICADA

PAGINA

PAA09

LEYENDA

- ① CUARTO ELECTRICO
- ② CLOSET ELECTRCIO
- ③ MANTENIMIENTO
- ④ ALMACEN
- ⑤ LAVANDERIA
- ⑥ CLASIFICACIÓN
- ⑦ LAVADO Y CENTRIFUGADO
- ⑧ SECADO
- ⑨ COSTURA
- ⑩ ALMACENAMIENTO
- ⑪ BAÑO
- ⑫ OFICINA

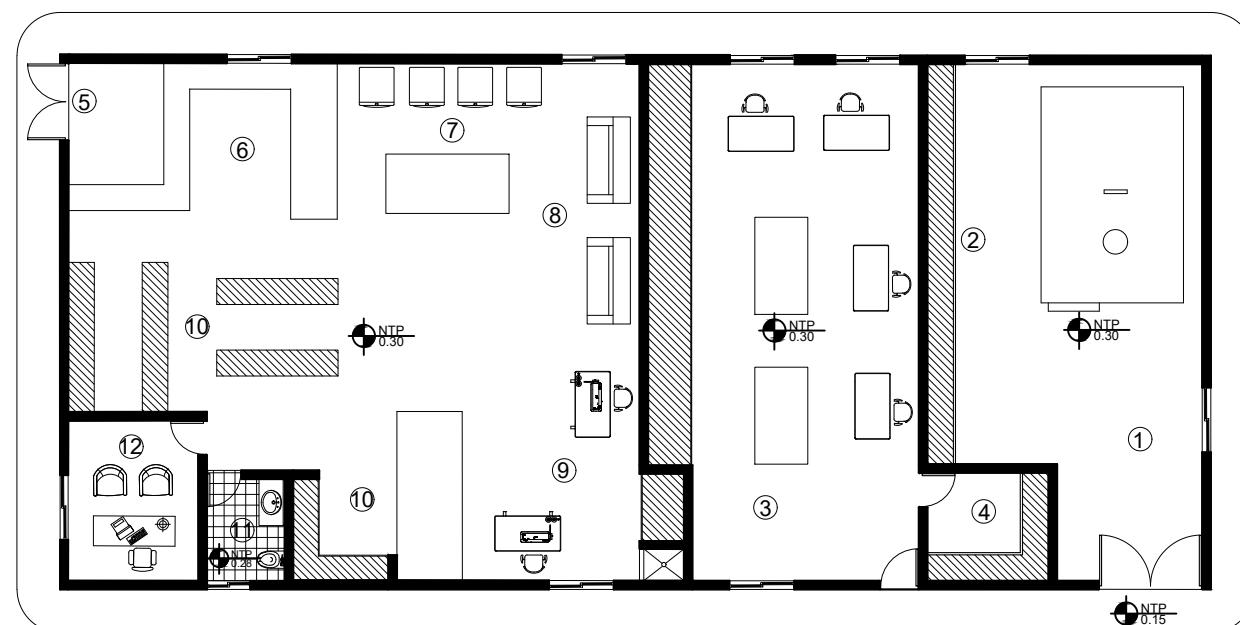

SIMBOLOGÍA DE MATERIALES


REVESTIMIENTO DE MADERA

PLANTA ARQUITECTONICA AMUEBLADA
CUARTO DE MAQUINA - MANTENIMIENTO - LAVANDERIA

ESC:1:100

LEYENDA

- ① BAÑO

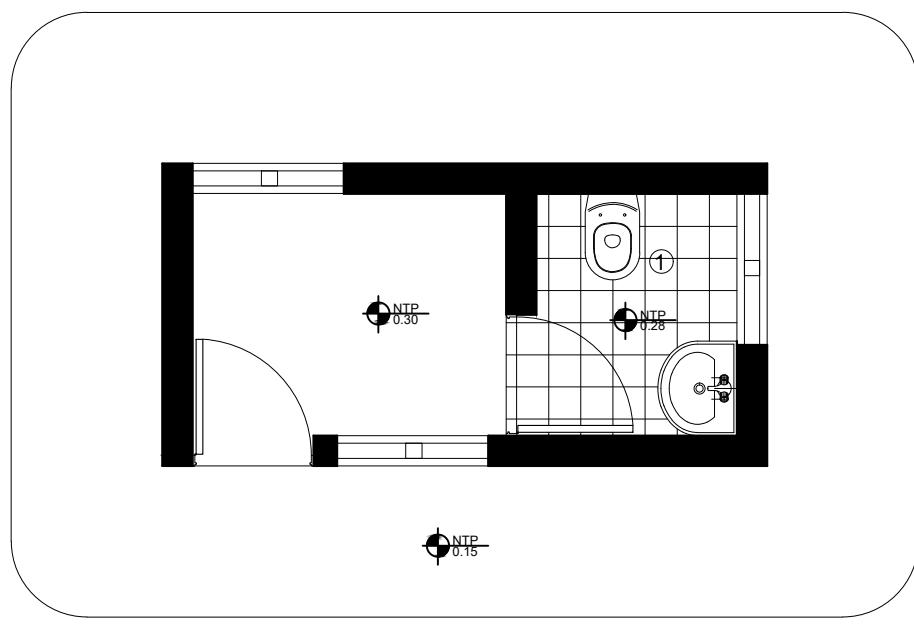

SIMBOLOGÍA DE MATERIALES

REVESTIMIENTO DE MADERA

PLANTA ARQUITECTONICA AMUEBLADA
CASETA DE SEGURIDAD - ENTRADA

ESC:1:50

PAA09



FACULTAD DE INGENIERIA
ESCUELA DE ARQUITECTURA

ASIGNATURA

DISEÑO V

ESTUDIANTE

SONIA RODRIGUEZ
2022-0336
MARIA ISABEL GRULLON
2022-0599

DOCENTE

JOSE ALBERTO DE LA CRUZ

SEMESTRE

2-2025

PROYECTO

HOTEL BOUTIQUE

CONTENIDO


INDICADO

ESCALA

INDICADA

PAGINA

PAA09

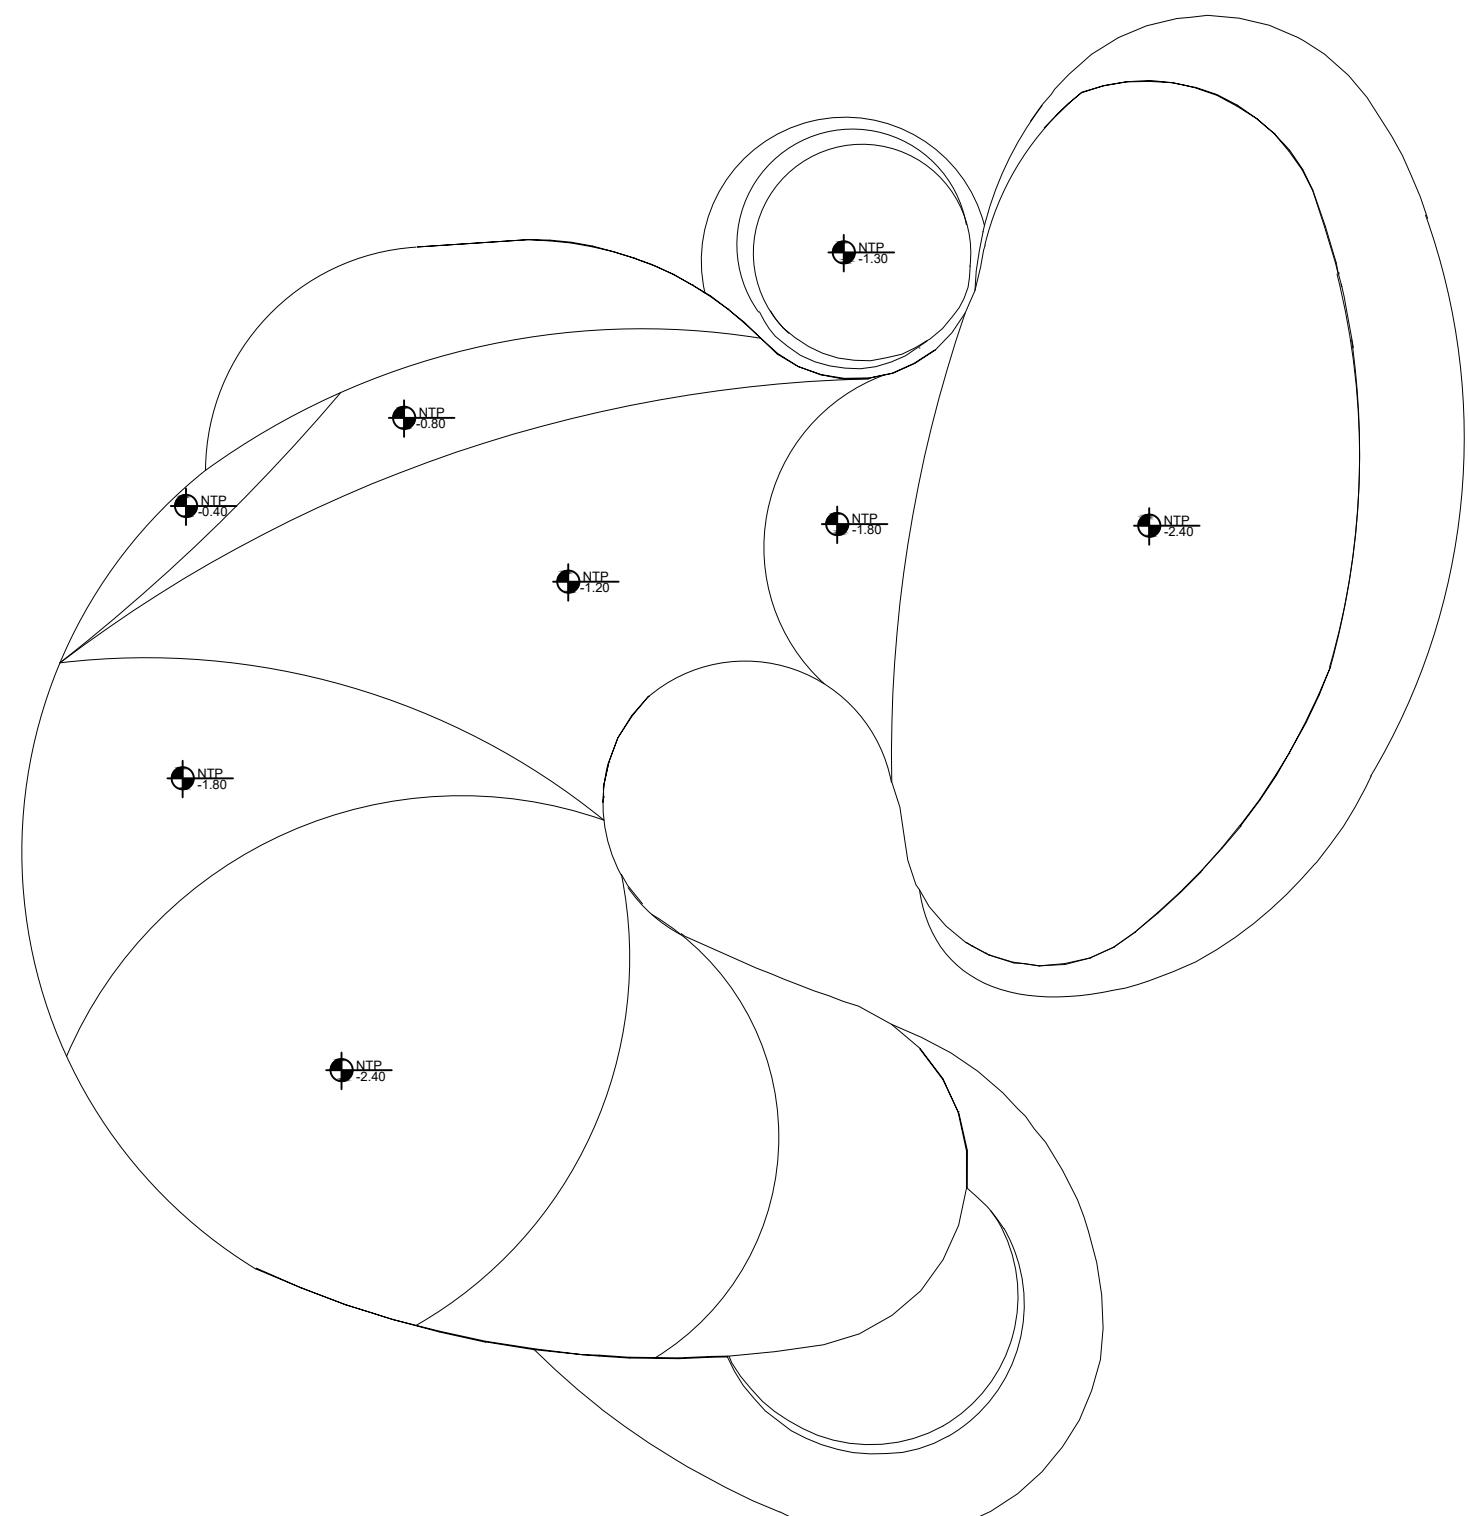



FACULTAD DE INGENIERIA
ESCUELA DE ARQUITECTURA

ASIGNATURA

DISEÑO V

ESTUDIANTE

SONIA RODRIGUEZ
2022-0336
ARIA ISABEL GRULLON
2022-0599

DOCENTE

JOSE ALBERTO DE LA CRUZ

SEMESTRE

PROYECTO

HOTEL BOUTIQUE

CONTENIDO


INDICADO

ESCALA

INDICADA

PAGINA

PAD01

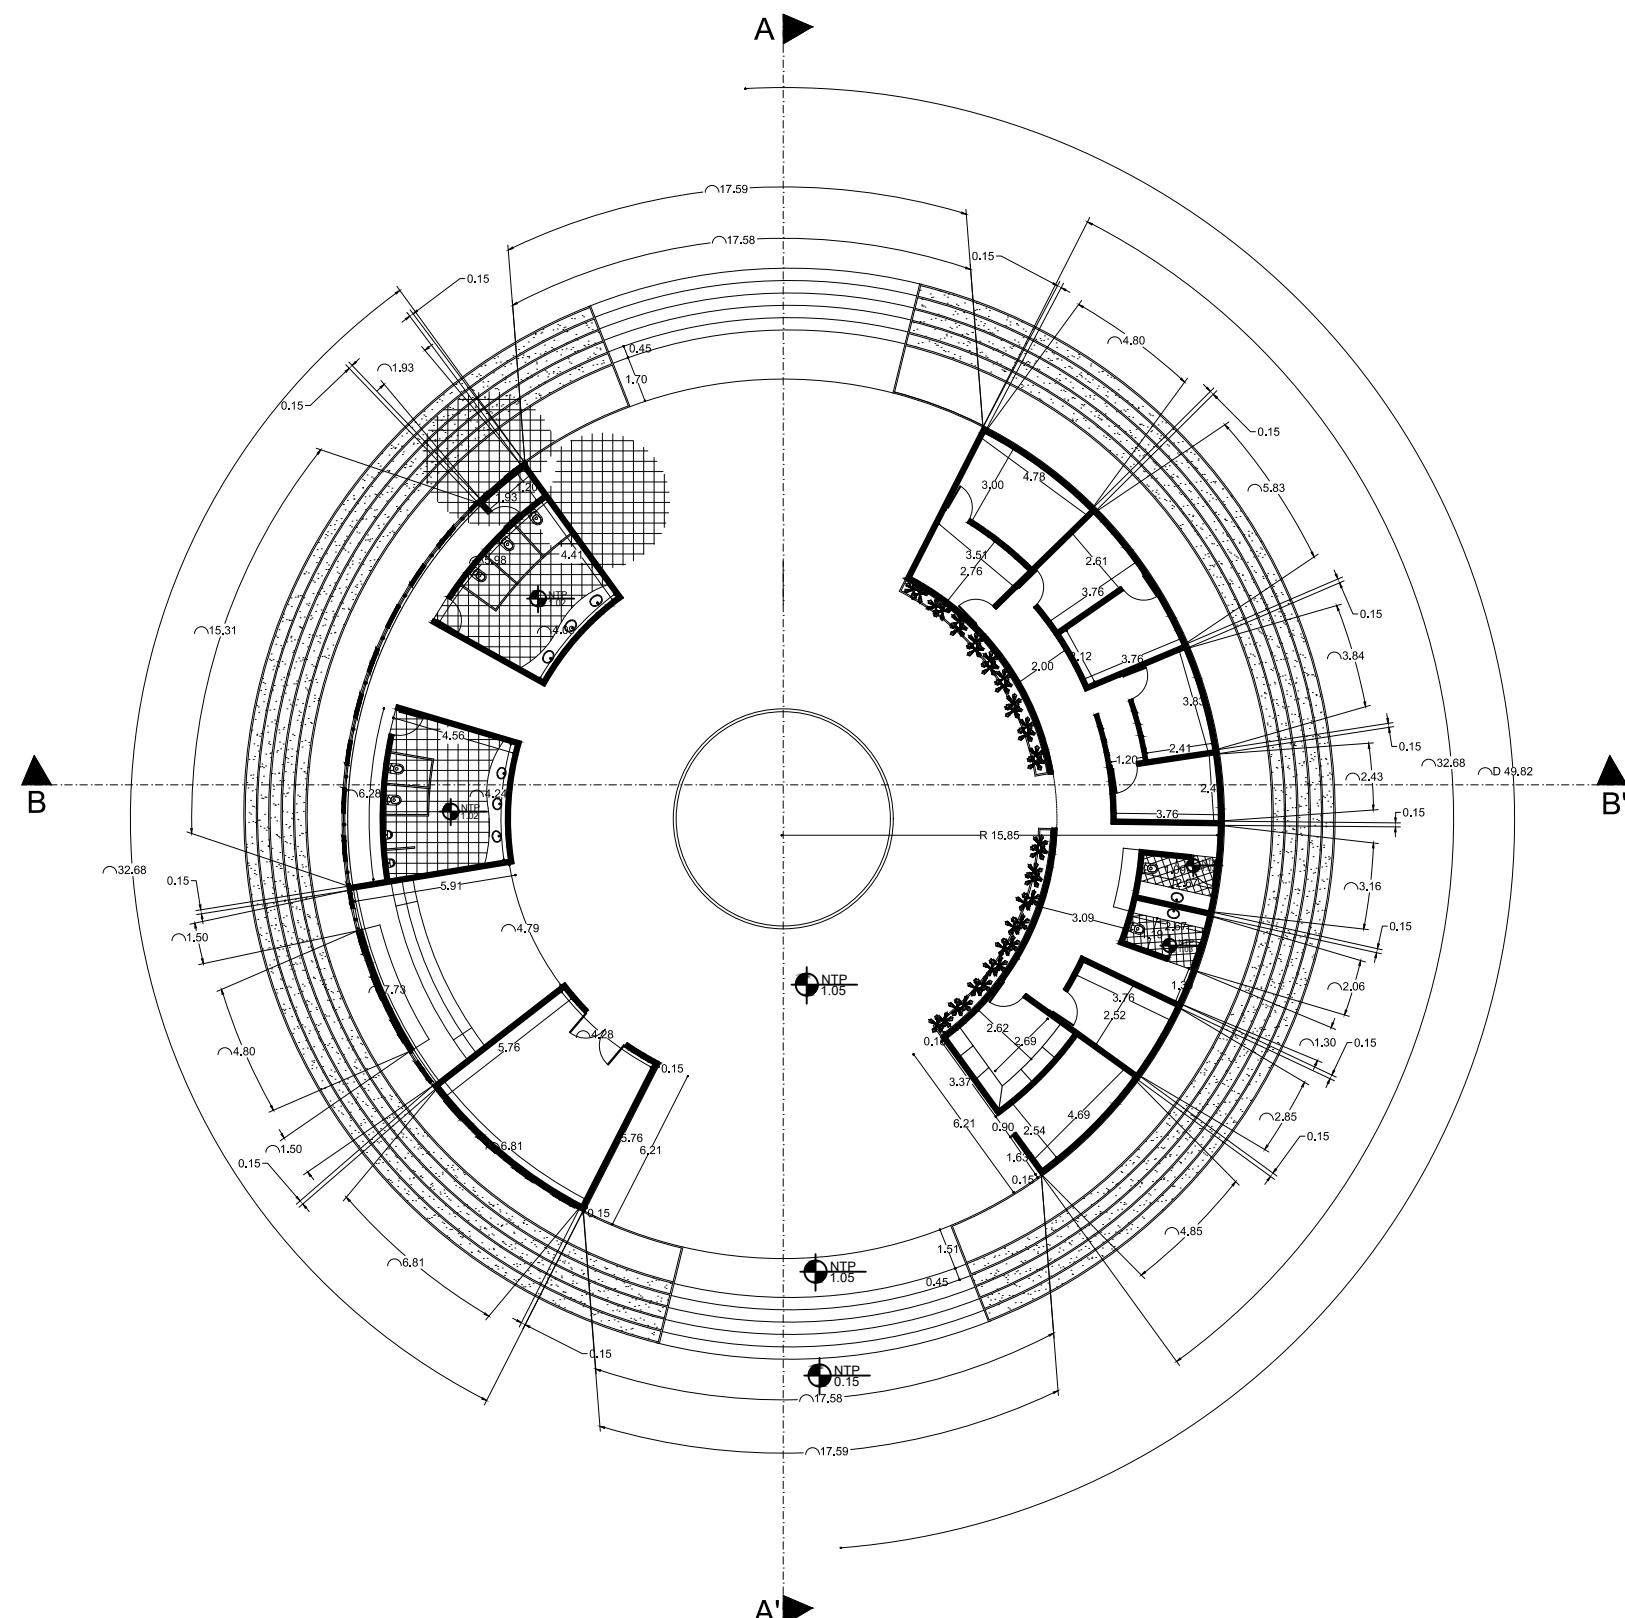

PLANTA ARQUITECTÓNICA DIMENSIONADA

ESC:1.2



FACULTAD DE INGENIERIA
ESCUELA DE ARQUITECTURA

ASIGNATURA

DISEÑO V

ESTUDIANTE

SONIA RODRIGUEZ
2022-0336
ARIA ISABEL GRULLON
2022-0599

DOCENTE

JOSE ALBERTO DE LA CRUZ

SEMESTRE

Page 1

— 1 —

HOTEL BOUTIQUE


CONTENIDO

INDICARO

ESCALA

INDICADA

—
—

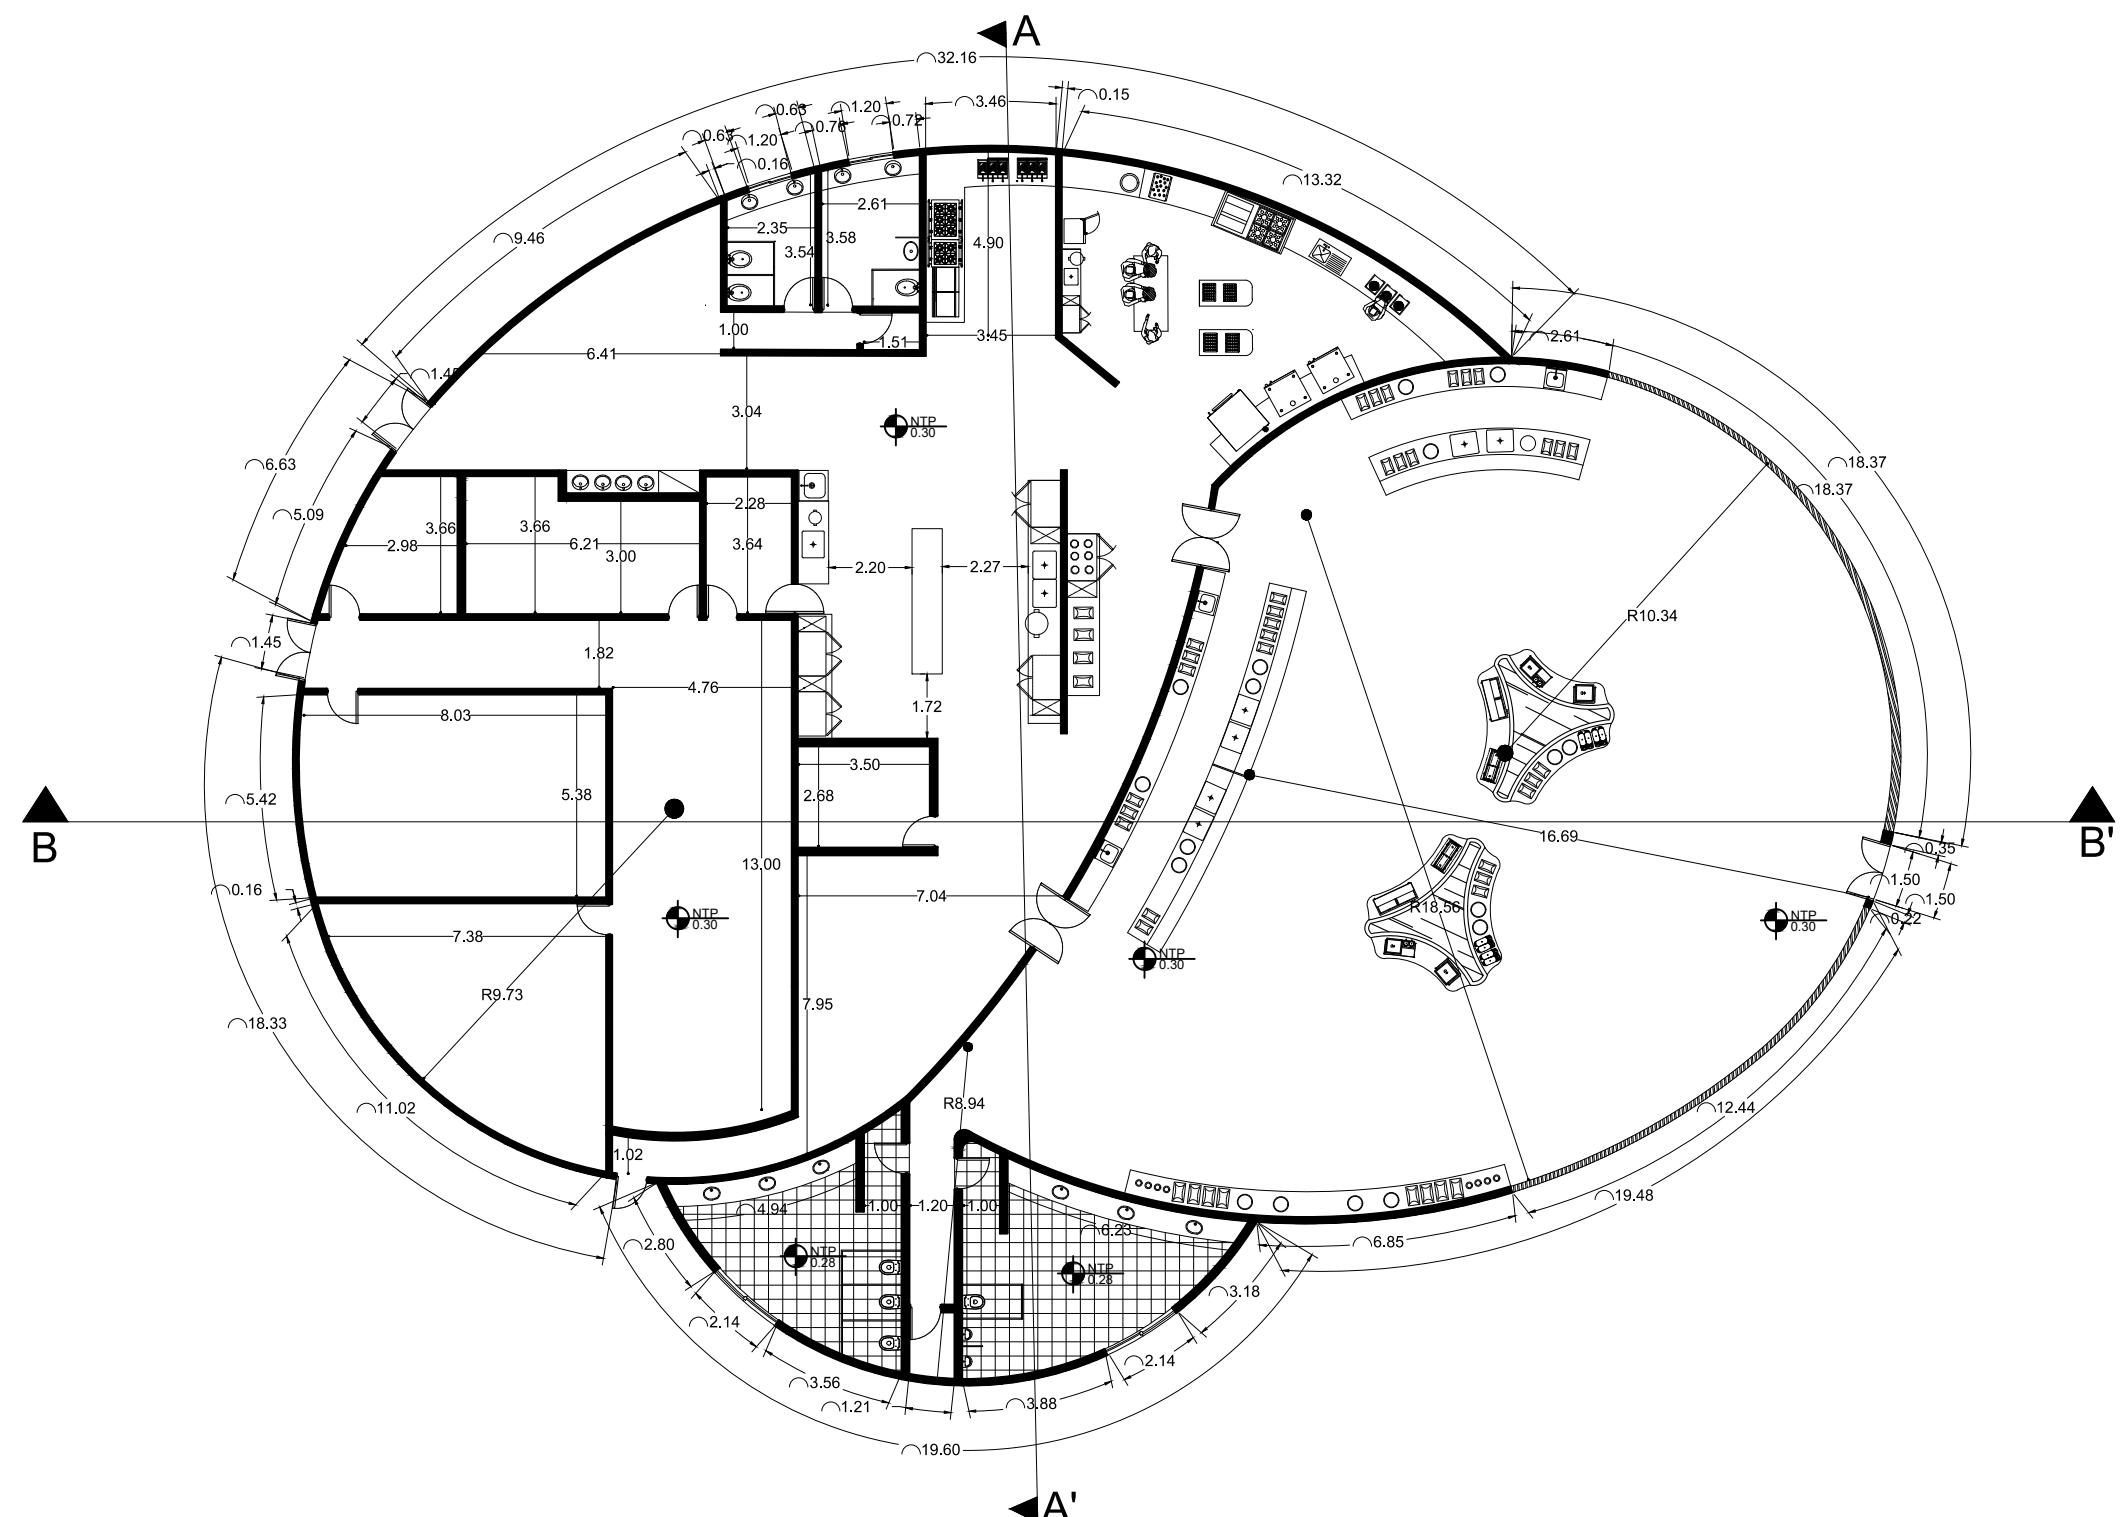

PLANTA ARQUITECTÓNICA DIMENSIONADA

ECC-1.2



FACULTAD DE INGENIERIA
ESCUELA DE ARQUITECTURA

ASIGNATURA

DISEÑO V

ESTUDIANTE

SONIA RODRIGUEZ
2022-0336
MARIA ISABEL GRULLON
2022-0599

DOCENT

JOSE ALBERTO DE LA CRUZ

CEMETRE

3.2025


— 1 —


—

— 1 —

— 1 —

PAD03

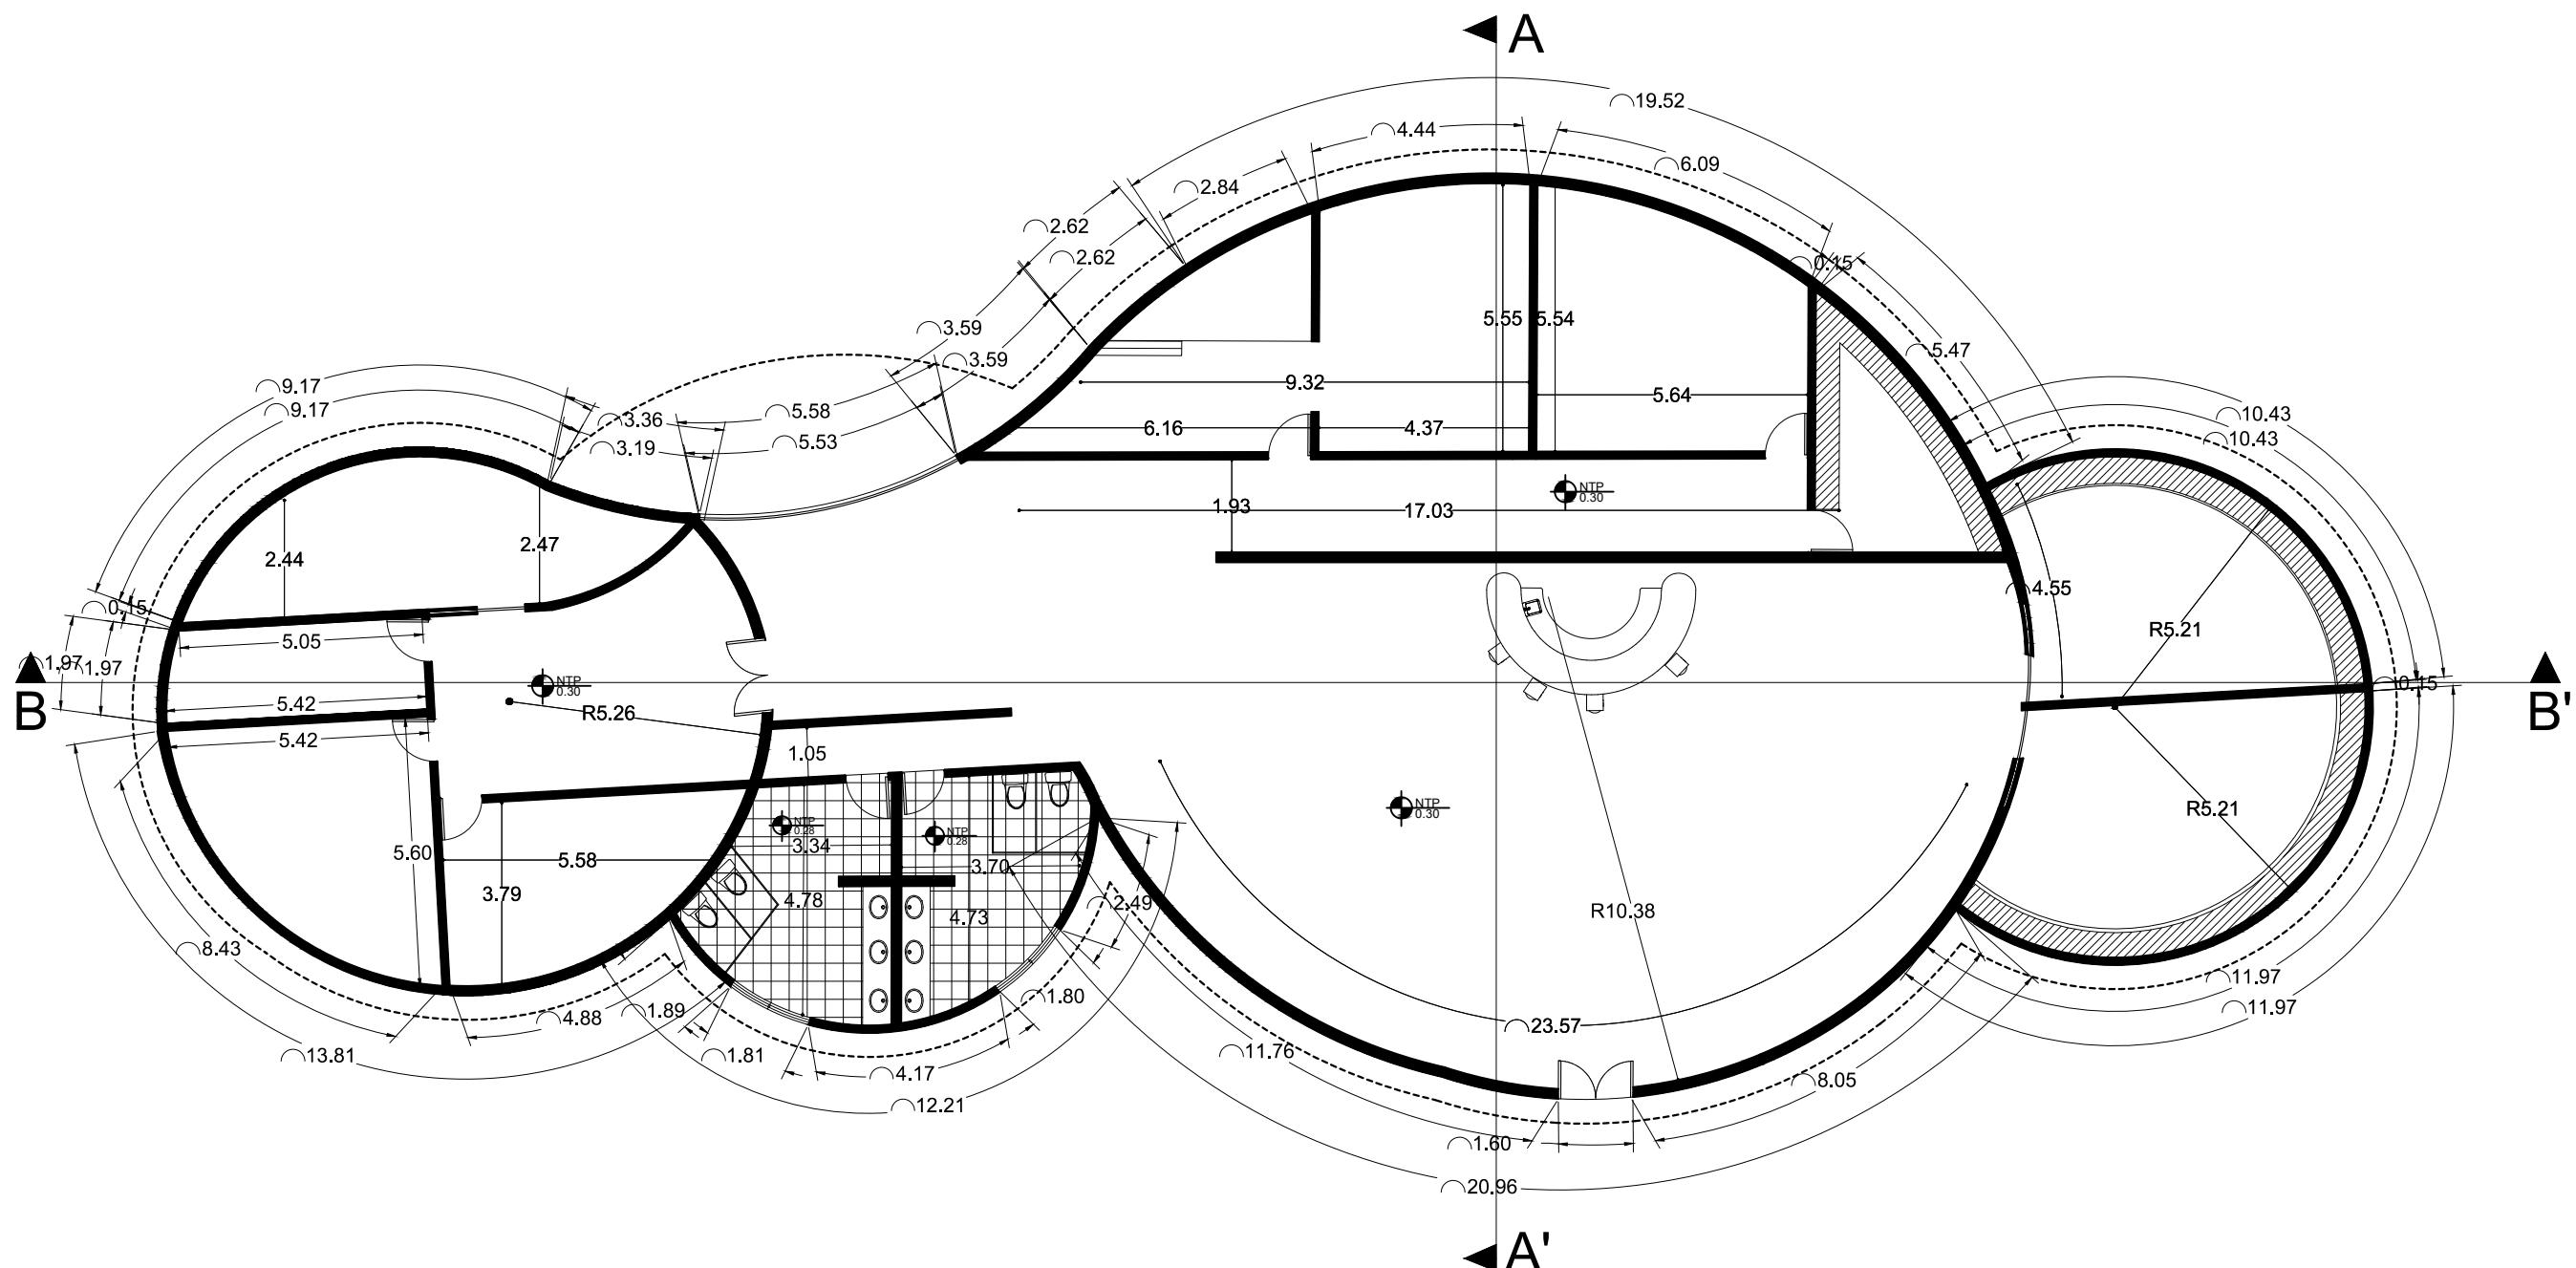

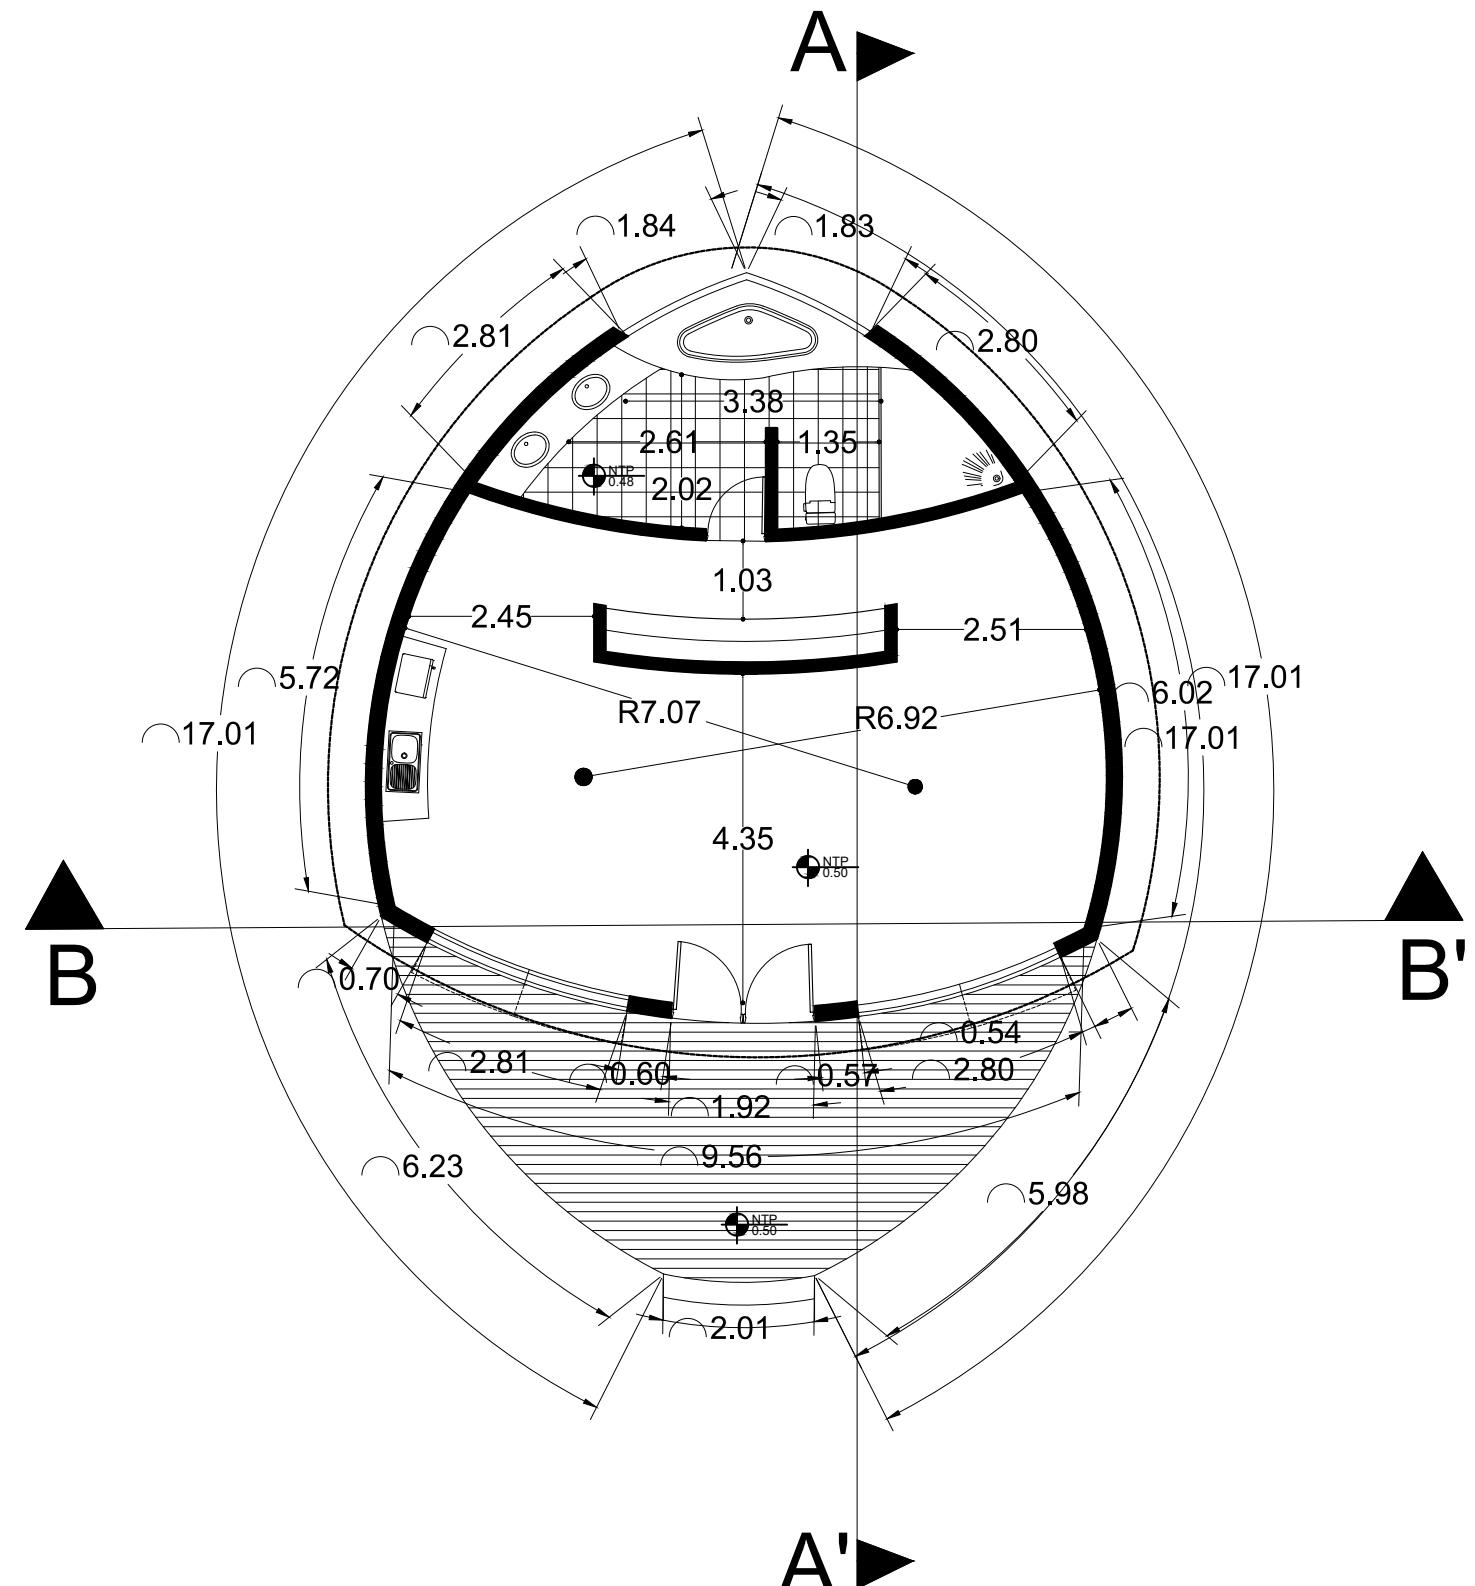



FACULTAD DE INGENIERIA
ESCUELA DE ARQUITECTURA

ASIGNATURA

DISEÑO V

ESTUDIANTE

SONIA RODRIGUEZ
2022-0336
MARIA ISABEL GRULLON
2022-0599

DOCENTE

JOSE ALBERTO DE LA CRUZ

SEMESTRE

2-2025

PROYECTO

HOTEL BOUTIQUE

CONTENIDO


INDICADO

ESCALA

INDICADA


PAGINA

PPV01

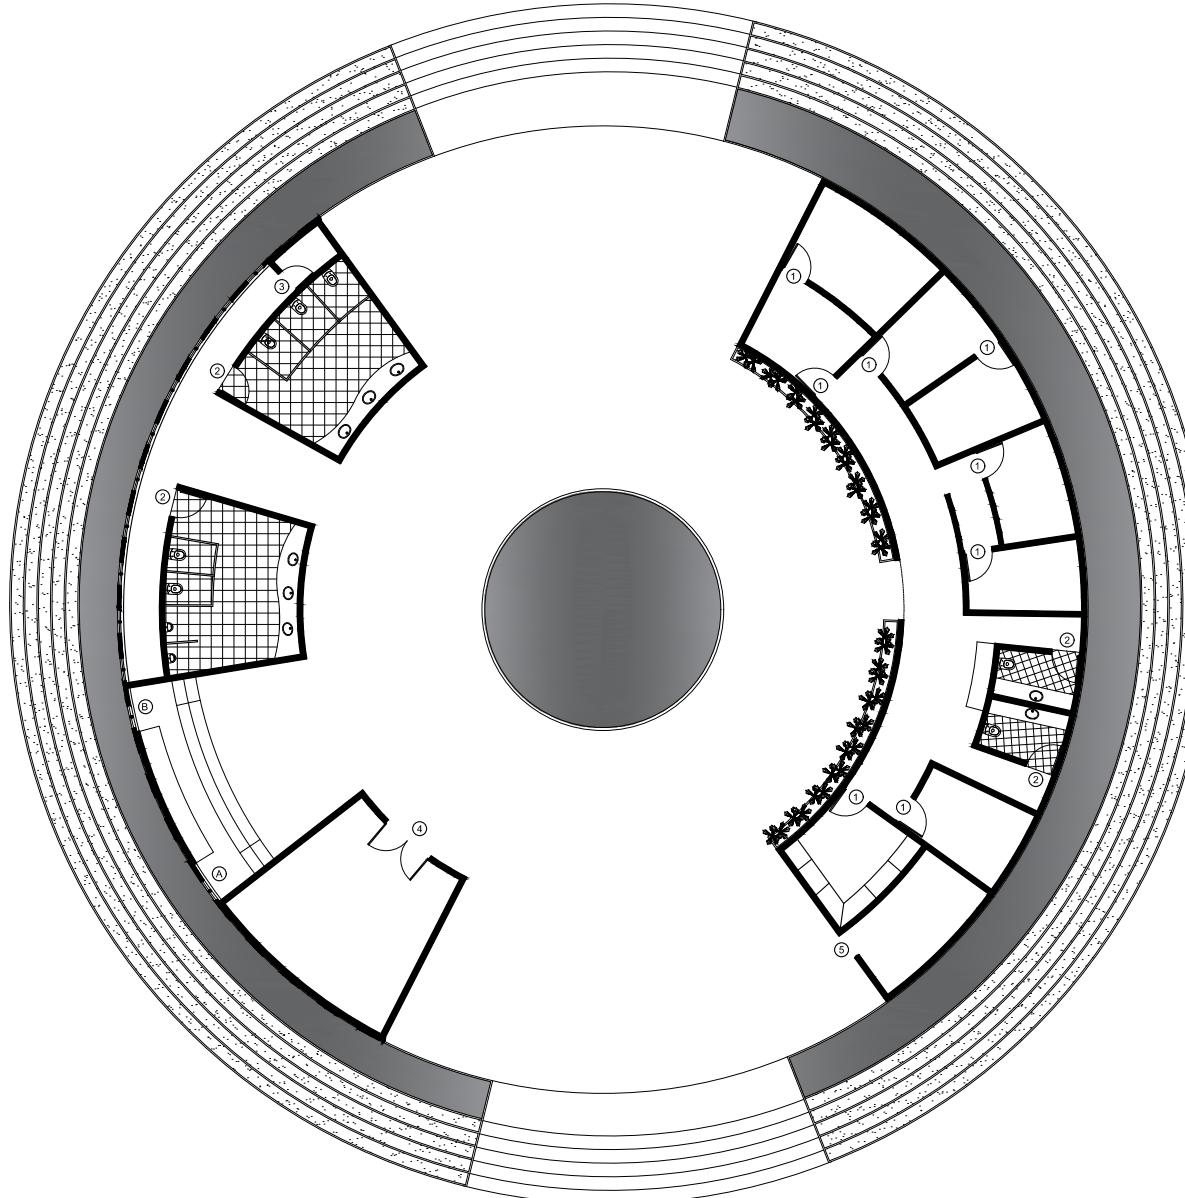


○ TABLA DE PUERTAS


Marca	Cantidad	Ancho	Alto	Descripción
1	8	0.95	2.10	Puerta batiente de 1 hoja
2	4	0.95	2.10	Puerta batiente de 1 hoja
3	1	0.80	2.10	Puerta batiente de 1 hoja
4	1	1.90	2.10	Puerta batiente de 2 hoja
5	1	0.90	2.10	Puerta corrediza

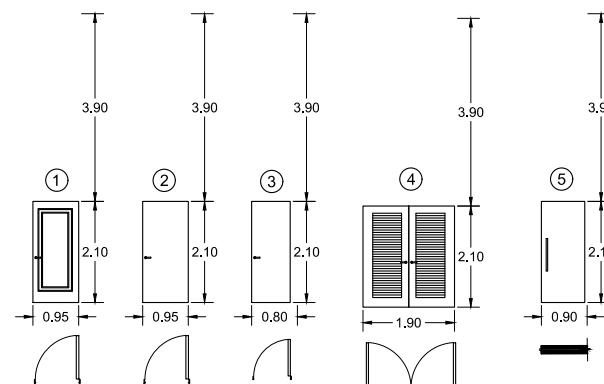

○ TABLA DE VENTANAS

Marca	Cantidad	Ancho	Alto	Descripción
A	1	1.50	4.00	Ventana fija curva de cristal
B	1	1.50	4.00	Ventana fija curva de cristal

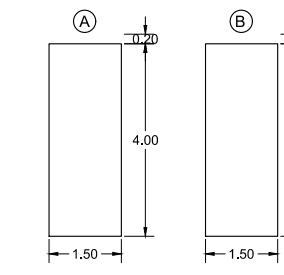

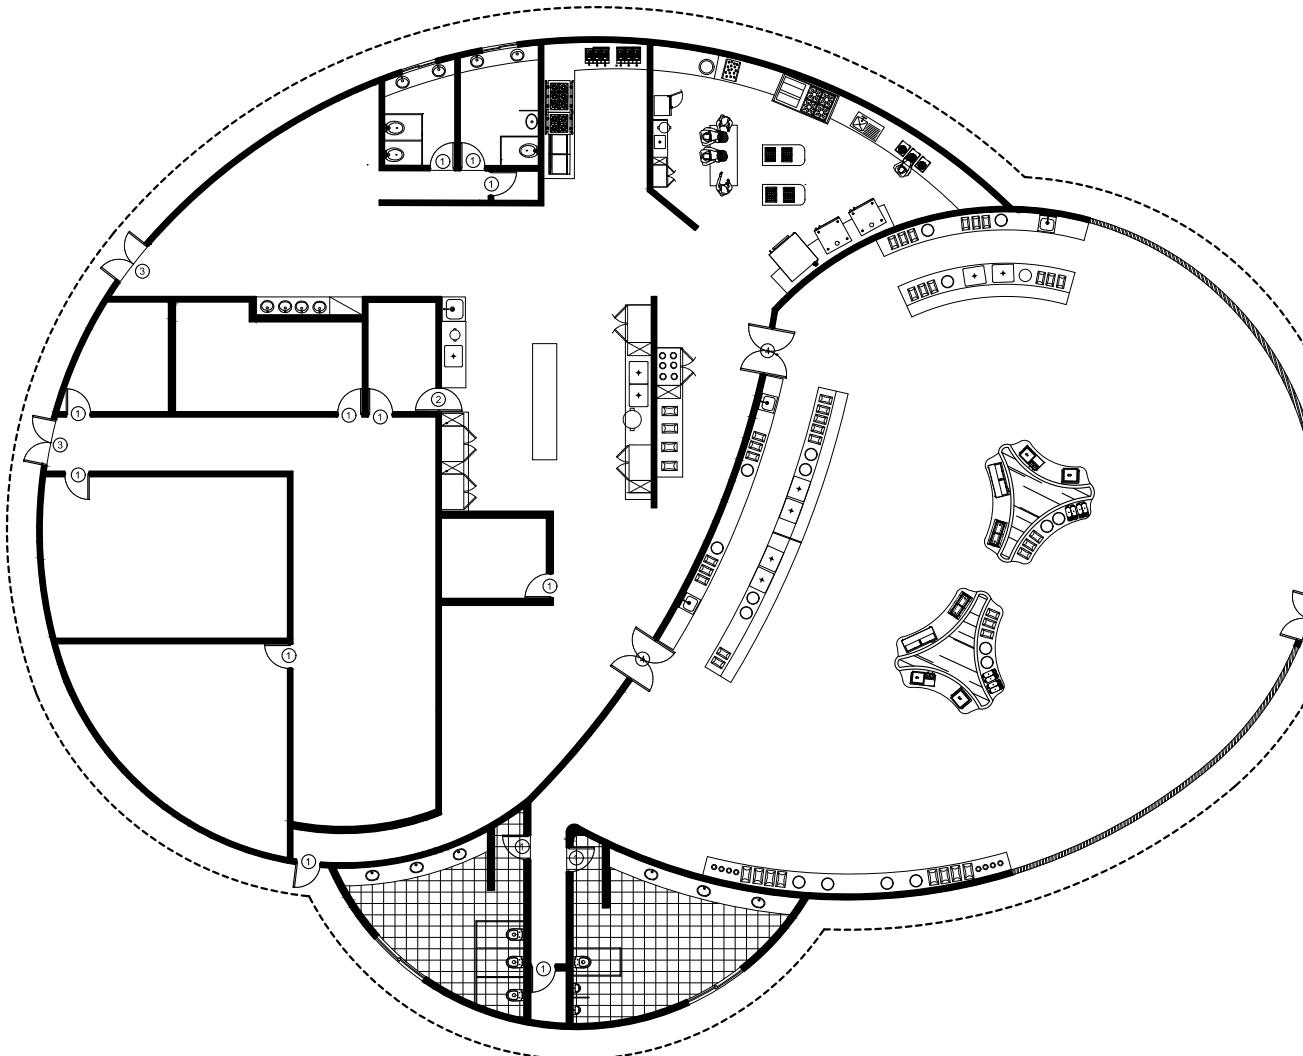


PLANO DE DETALLES DE PUERTAS Y VENTANAS

RESTAURANTE BUFFET

ESC:1:250


○ TABLA DE PUERTAS


Marca	Cantidad	Ancho	Alto	Descripcion
1	13	0.85	2.10	Puerta batiente de 1 hoja
2	1	0.80	2.10	Puerta de vaiven de 1 hoja
3	2	1.60	2.10	Puerta batiente de 2 hoja
4	2	1.60	2.10	Puerta de vaiven de 2 hoja
5	1	1.60	2.10	Puerta batiente de 2 hoja

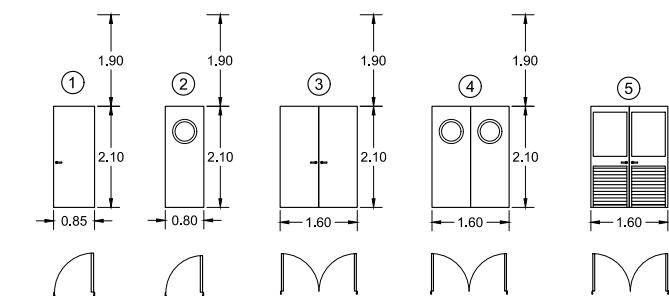

○ TABLA DE VENTANAS


Marca	Cantidad	Ancho	Alto	Descripcion
A	1	2.10	1.00	Ventana corrediza curva de cristal
B	1	2.10	1.00	Ventana corrediza curva de cristal
C	1	1.20	1.00	Ventana corrediza curva de cristal
D	1	1.20	1.00	Ventana corrediza curva de cristal

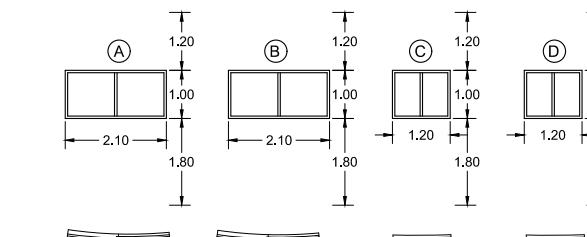

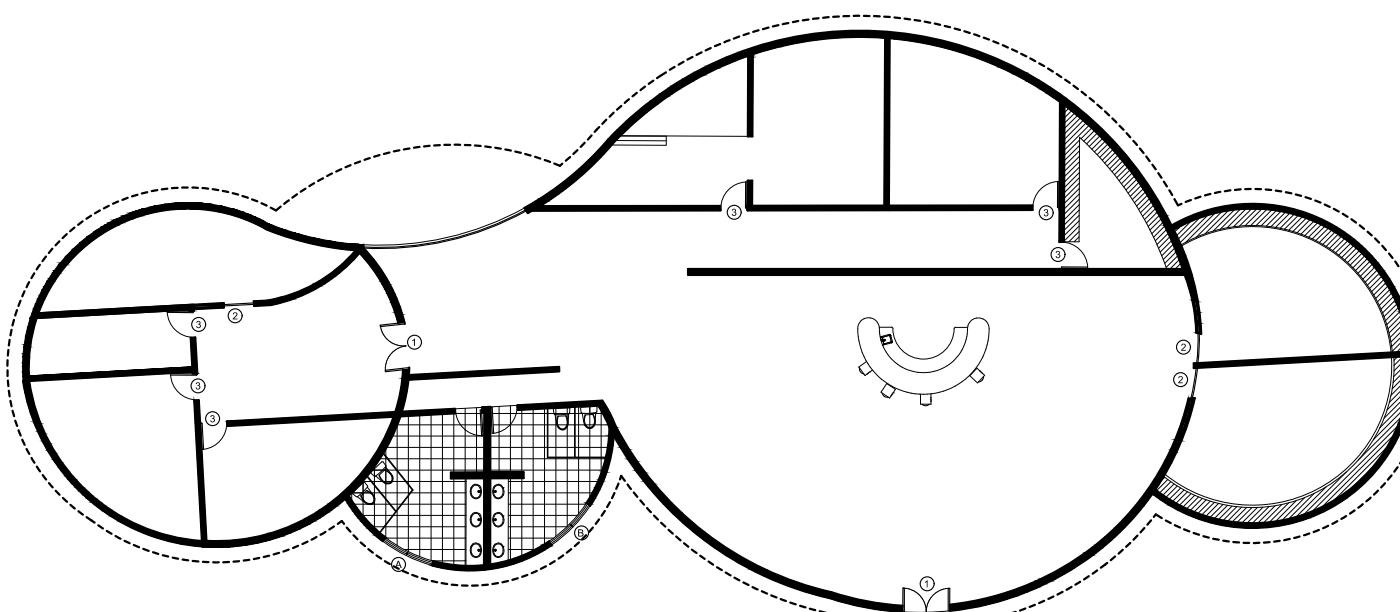


○ TABLA DE PUERTAS


Marca	Cantidad	Ancho	Alto	Descripcion
1	2	1.60	2.10	Puerta batiente de 2 hojas
2	3	1.00	2.10	Puerta corrediza
3	2	0.90	2.10	Puerta batiente de 1 hoja

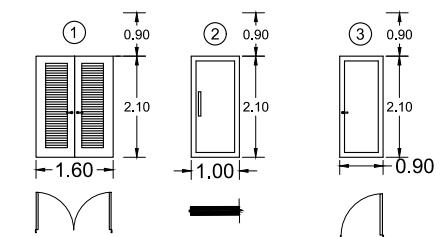

○ TABLA DE VENTANAS

Marca	Cantidad	Ancho	Alto	Descripcion
A	1	1.80	1.00	Ventana corrediza curva de cristal
B	1	1.80	1.00	Ventana corrediza curva de cristal

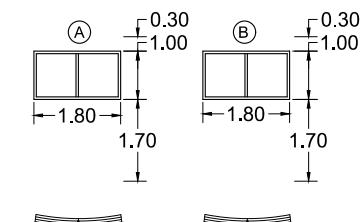

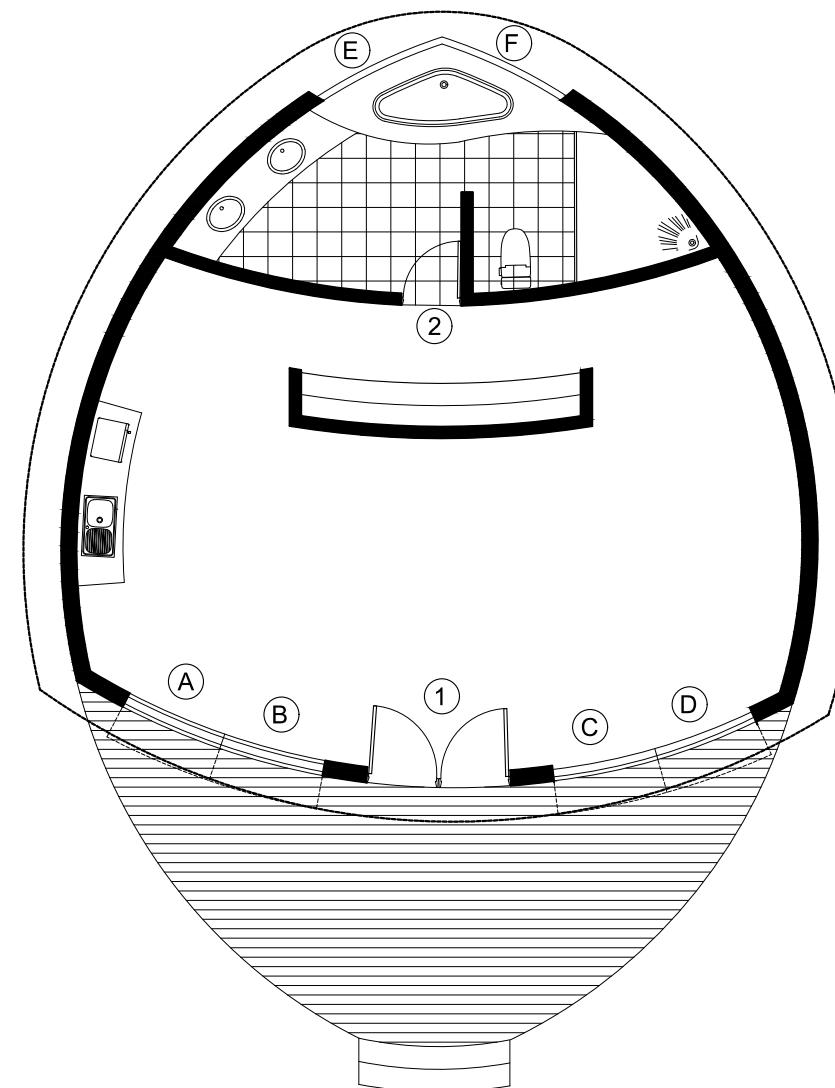


PLANO DE DETALLES DE PUERTAS Y VENTANAS

RESTAURANTE BUFFET

ESC:1:250


○ TABLA DE PUERTAS

Marca	Cantidad	Ancho	Alto	Descripcion
1	2	1.60	2.10	Puerta batiente de 2 hojas
2	3	1.00	2.10	Puerta corrediza
3	2	0.90	2.10	Puerta batiente de 1 hoja

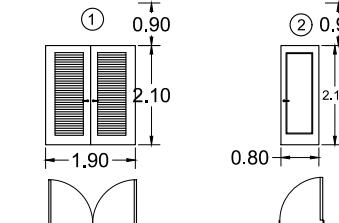

○ TABLA DE VENTANAS

Marca	Cantidad	Ancho	Alto	Descripcion
A	1	1.40	1.00	Ventana pivotante curva de cristal
B	1	1.40	1.00	Ventana pivotante curva de cristal
C	1	1.40	1.00	Ventana pivotante curva de cristal
D	1	1.40	1.00	Ventana pivotante curva de cristal
E	1	1.80	1.00	Ventana fija curva de cristal
F	1	1.80	1.00	Ventana fija curva de cristal

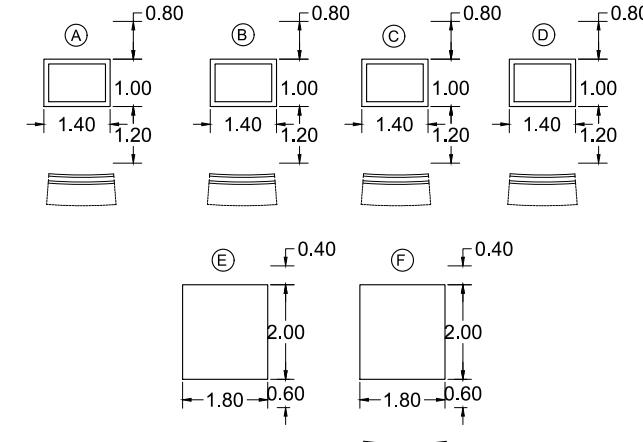

FACULTAD DE INGENIERIA
ESCUELA DE ARQUITECTURA

ASIGNATURA

DISEÑO V

ESTUDIANTE

SONIA RODRIGUEZ
2022-0336
MARIA ISABEL GRULLON
2022-0599

DOCENTE

JOSE ALBERTO DE LA CRUZ

SEMESTRE

2-2025

PROYECTO

HOTEL BOUTIQUE

CONTENIDO

INDICADO

ESCALA

INDICADA

PAGINA

PPV04



FACULTAD DE INGENIERIA
ESCUELA DE ARQUITECTURA

ASIGNATURA

DISEÑO V

ESTUDIANTE

SONIA RODRIGUEZ
2022-0336
MARIA ISABEL GRULLON
2022-0599

DOCENTE

JOSE ALBERTO DE LA CRUZ

SEMESTRE

2-2025

PROYECTO

HOTEL BOUTIQUE

CONTENIDO


INDICADO

ESCALA

INDICADA

PAGINA

SEC01

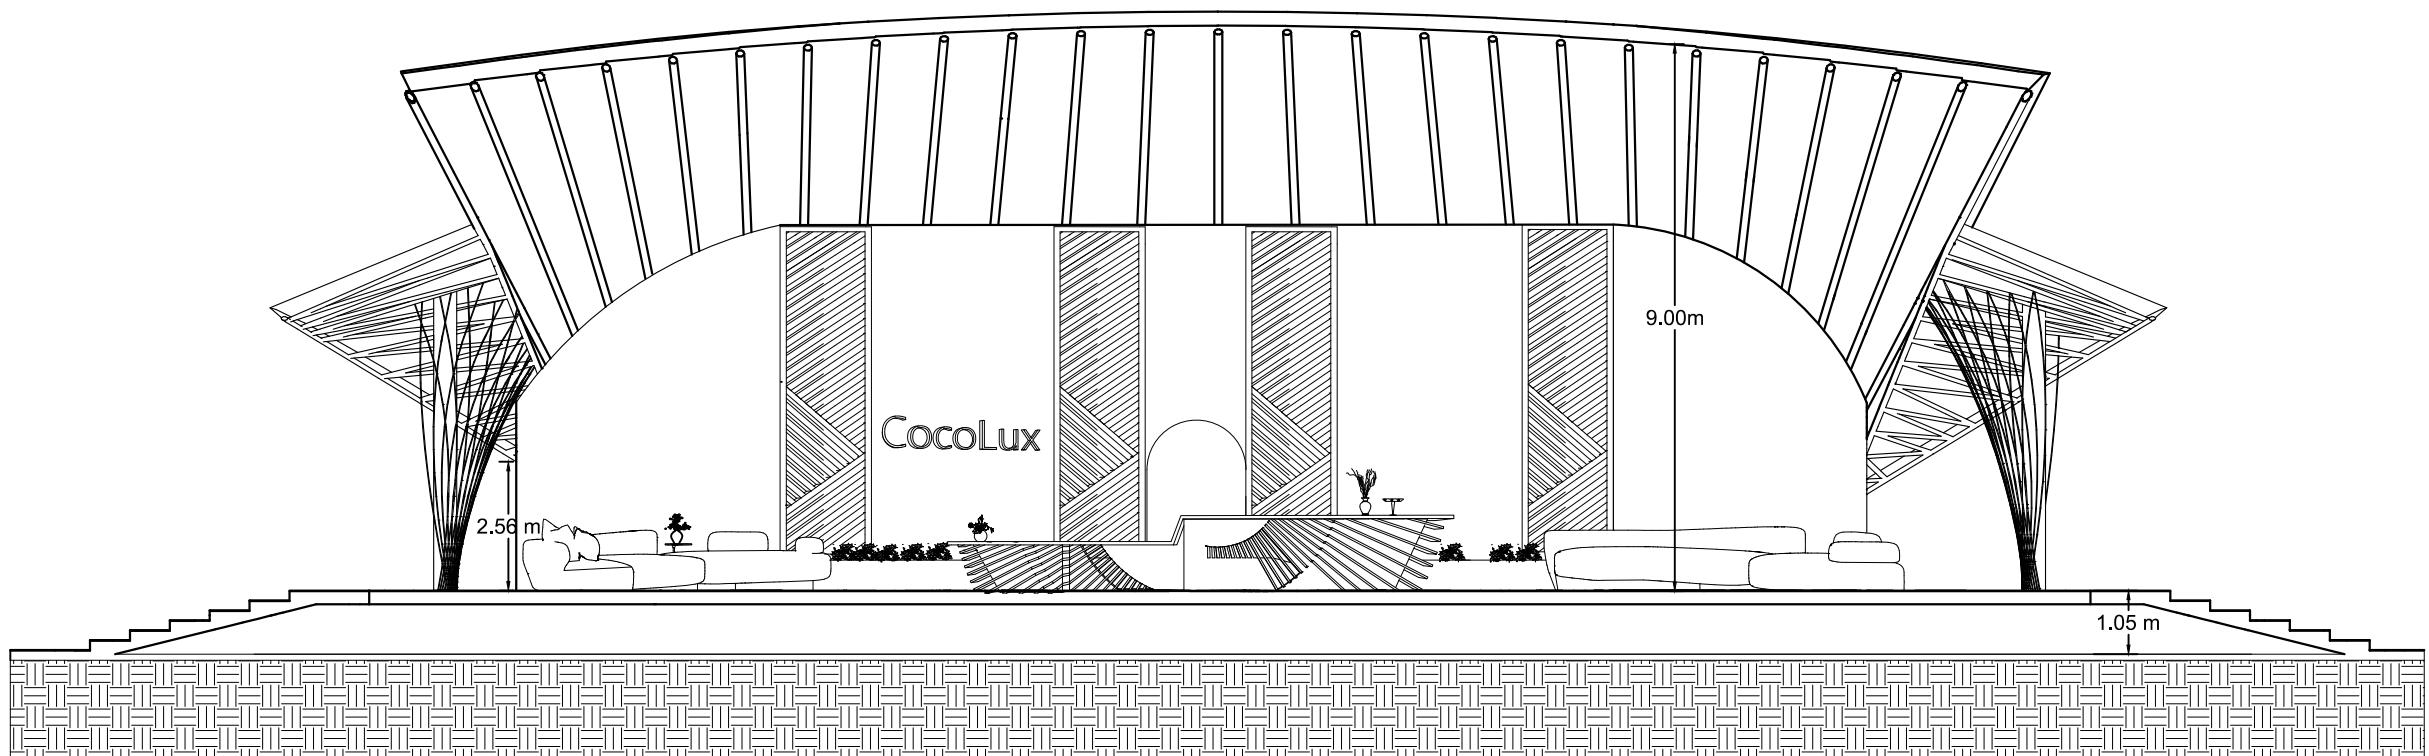

SECCIÓN A - A'
LOBBY

ESC:1:150



FACULTAD DE INGENIERIA
ESCUELA DE ARQUITECTURA

ASIGNATURA

DISEÑO V

ESTUDIANTE

SONIA RODRIGUEZ
2022-0336
MARIA ISABEL GRULLON
2022-0599

DOCENTE

JOSE ALBERTO DE LA CRUZ

SEMESTRE

2-2025

PROYECTO

HOTEL BOUTIQUE

CONTENIDO


INDICADO

ESCALA

INDICADA

PAGINA

SEC02

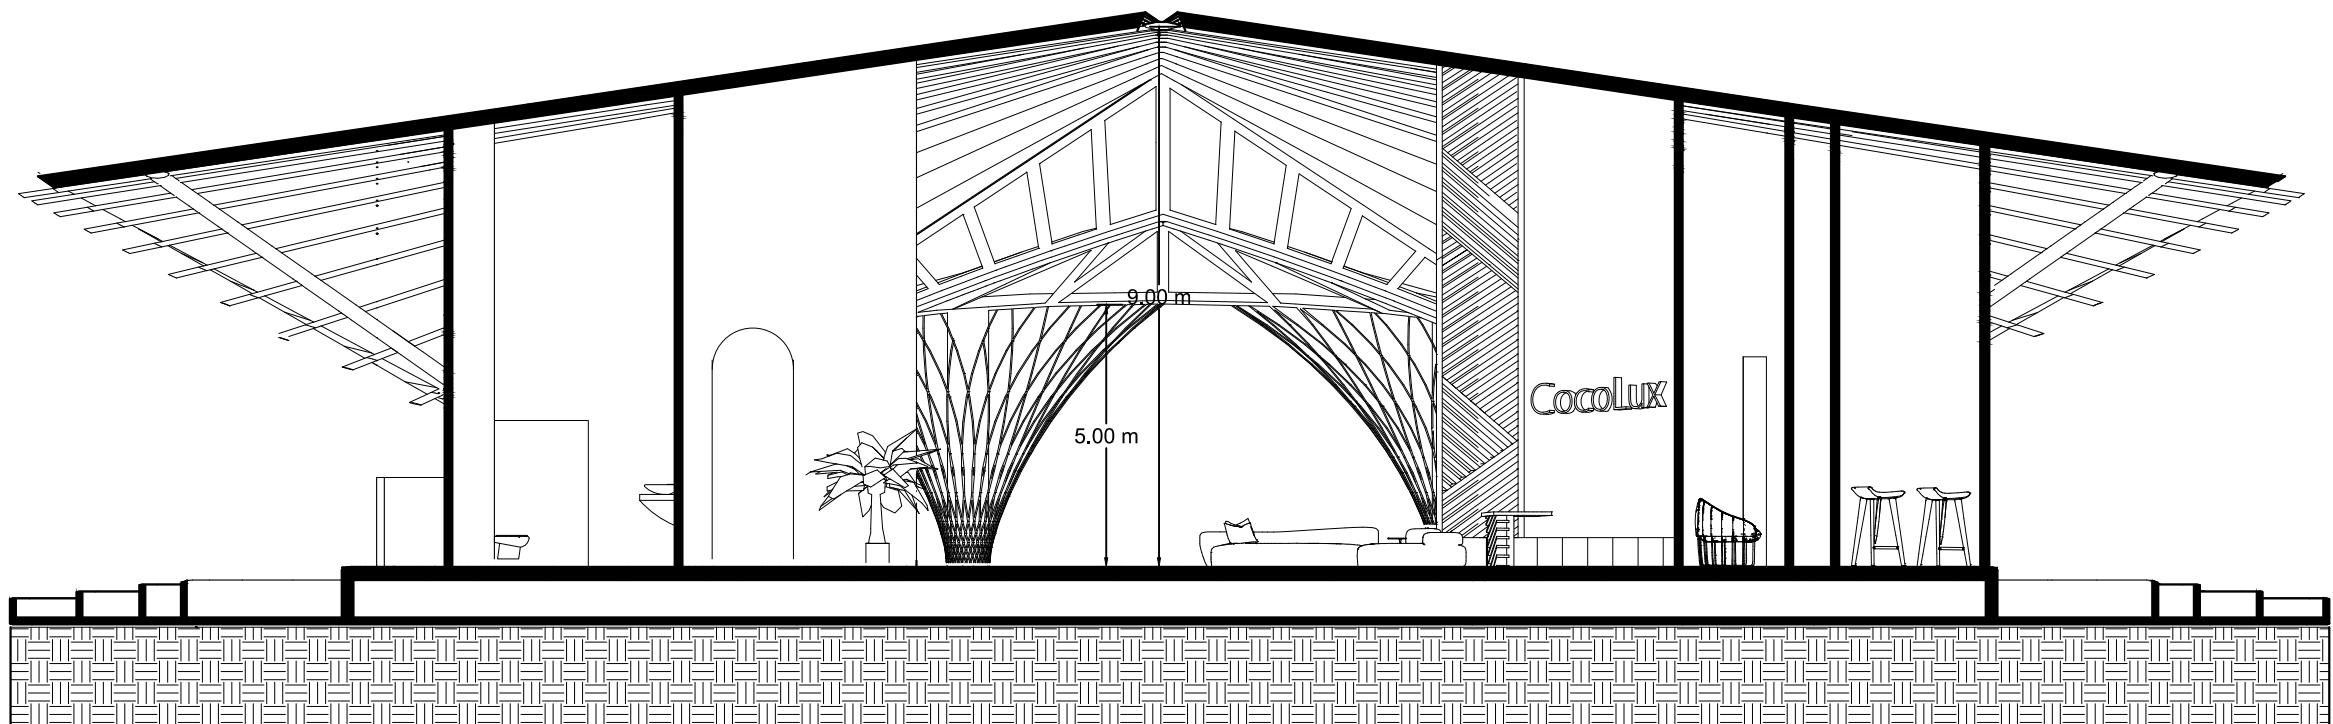

SECCIÓN B - B'
LOBBY

ESC:1:150



FACULTAD DE INGENIERIA
ESCUELA DE ARQUITECTURA

ASIGNATURA

DISEÑO V

ESTUDIANTE

SONIA RODRIGUEZ
2022-0336
MARIA ISABEL GRULLON
2022-0599

DOCENTE

JOSE ALBERTO DE LA CRUZ

SEMESTRE

2-2025

PROYECTO

HOTEL BOUTIQUE

CONTENIDO


INDICADO

ESCALA

INDICADA


PAGINA

SEC03

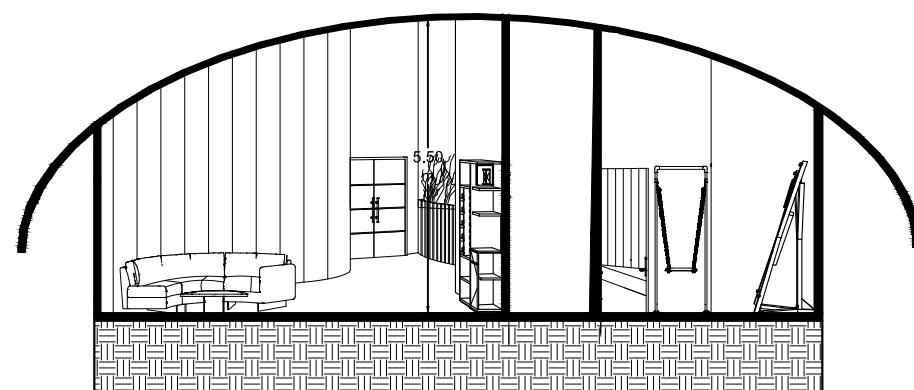

SECCIÓN A - A'
PRACTICA EL COCO

ESC:1:200

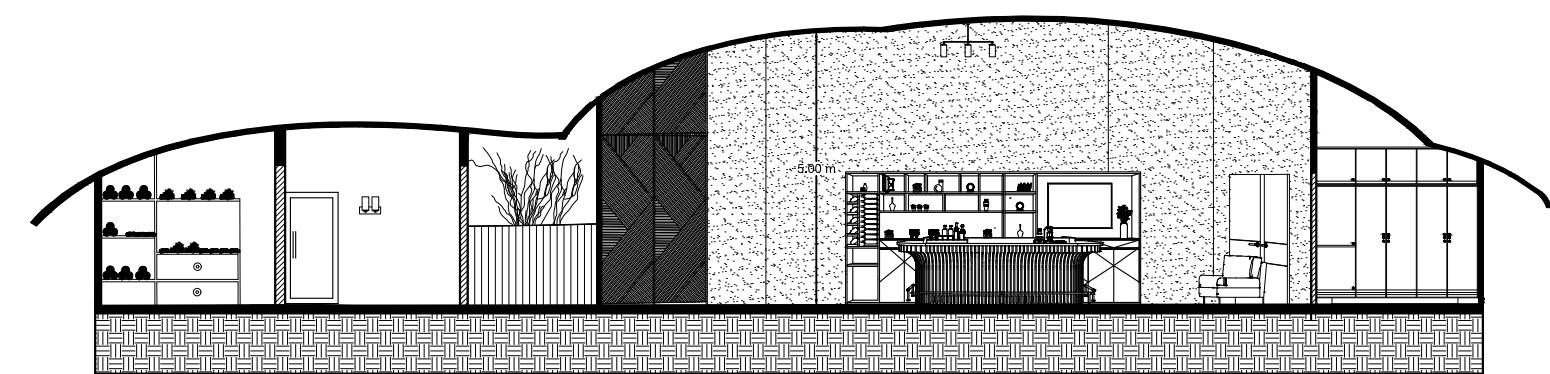

SECCIÓN B - B'
PRACTICA EL COCO

ESC:1:250



FACULTAD DE INGENIERIA
ESCUELA DE ARQUITECTURA

ASIGNATURA

DISEÑO V

ESTUDIANTE

SONIA RODRIGUEZ
2022-0336
MARIA ISABEL GRULLON
2022-0599

DOCENTE

JOSE ALBERTO DE LA CRUZ

SEMESTRE

2-2025

PROYECTO

HOTEL BOUTIQUE

CONTENIDO


INDICADO

ESCALA

INDICADA


PAGINA

SEC04

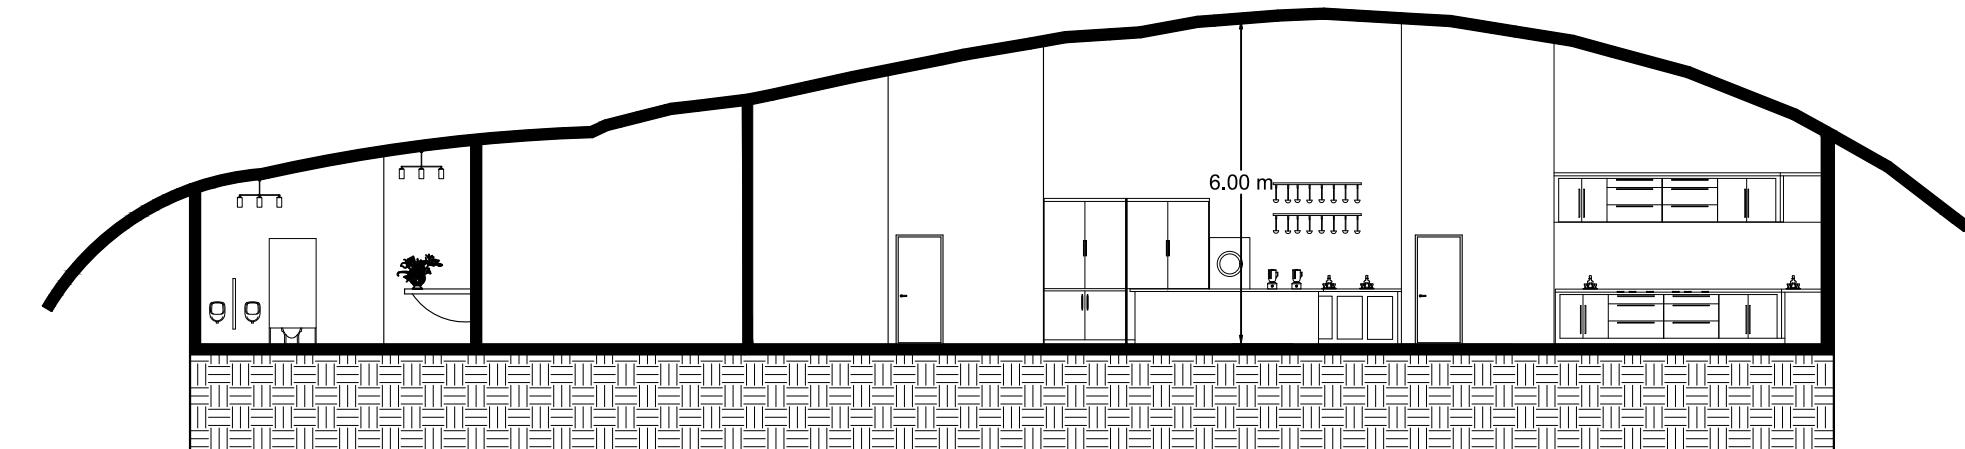

SECCIÓN A - A'
RESTAURANTE BUFFET

ESC:1:150

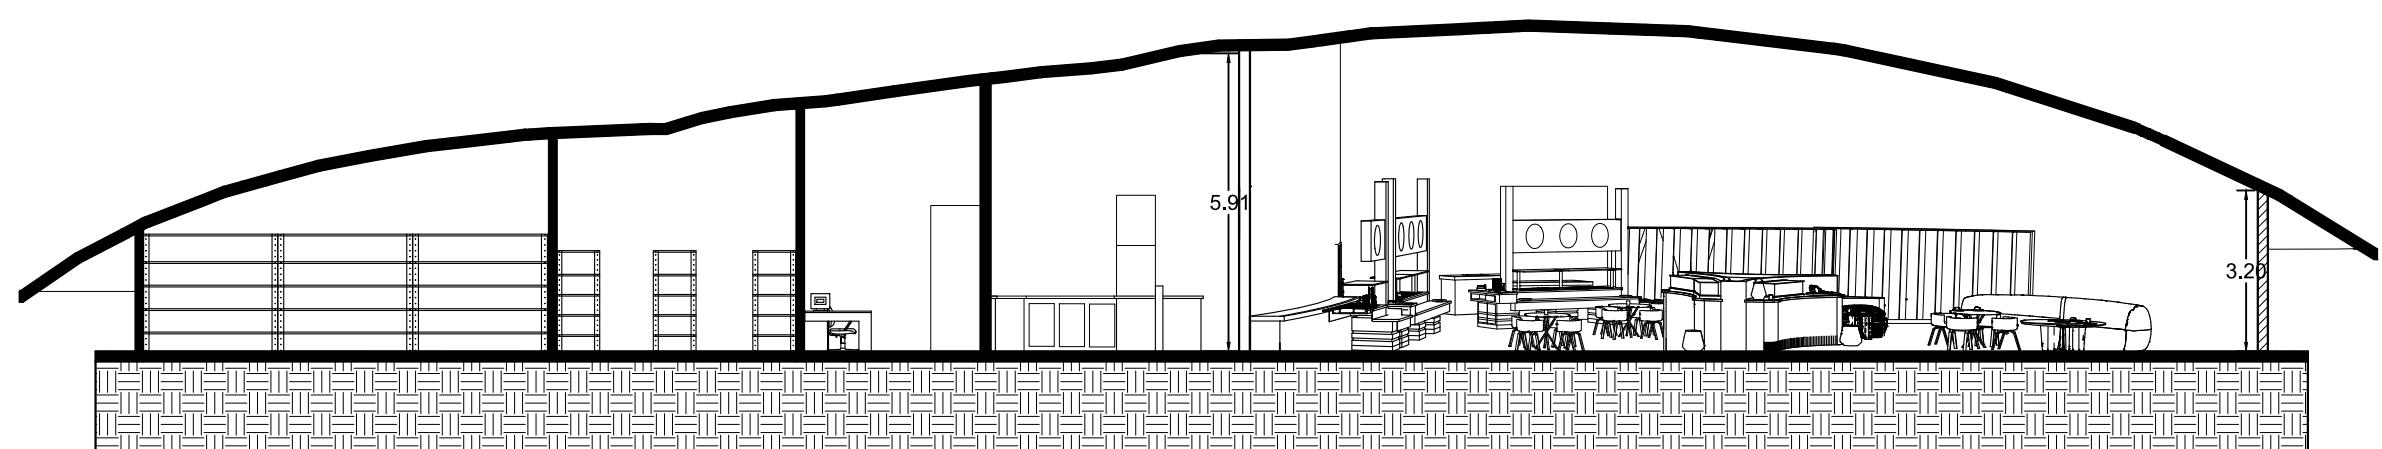

SECCIÓN B - B'
RESTAURANTE BUFFET

ESC:1:150

ASIGNATURA

DISEÑO V

ESTUDIANTE

SONIA RODRIGUEZ
 2022-0336
 MARIA ISABEL GRULLON
 2022-0599

DOCENTE

JOSE ALBERTO DE LA CRUZ

SEMESTRE

2-2025

PROYECTO

HOTEL BOUTIQUE

CONTENIDO

INDICADO

ESCALA

INDICADA


PAGINA

SEC05



SECCIÓN A - A'
 REFUGIO DEL COCO SUITE

ESC:1:100

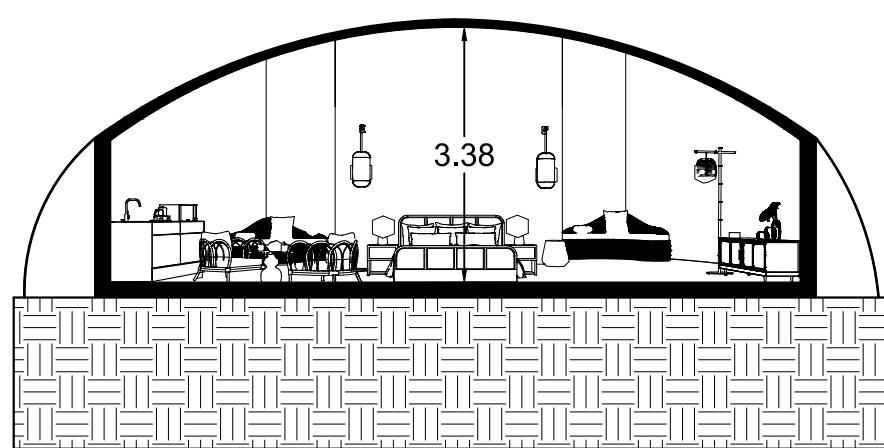

SECCIÓN B - B'
 REFUGIO DEL COCO SUITE

ESC:1:100



FACULTAD DE INGENIERIA
ESCUELA DE ARQUITECTURA

ASIGNATURA

DISEÑO V

ESTUDIANTE

SONIA RODRIGUEZ
2022-0336
MARIA ISABEL GRULLON
2022-0599

DOCENTE

JOSE ALBERTO DE LA CRUZ

SEMESTRE

2-2025

PROYECTO

HOTEL BOUTIQUE

CONTENIDO


INDICADO

ESCALA

INDICADA

PAGINA

PTS01

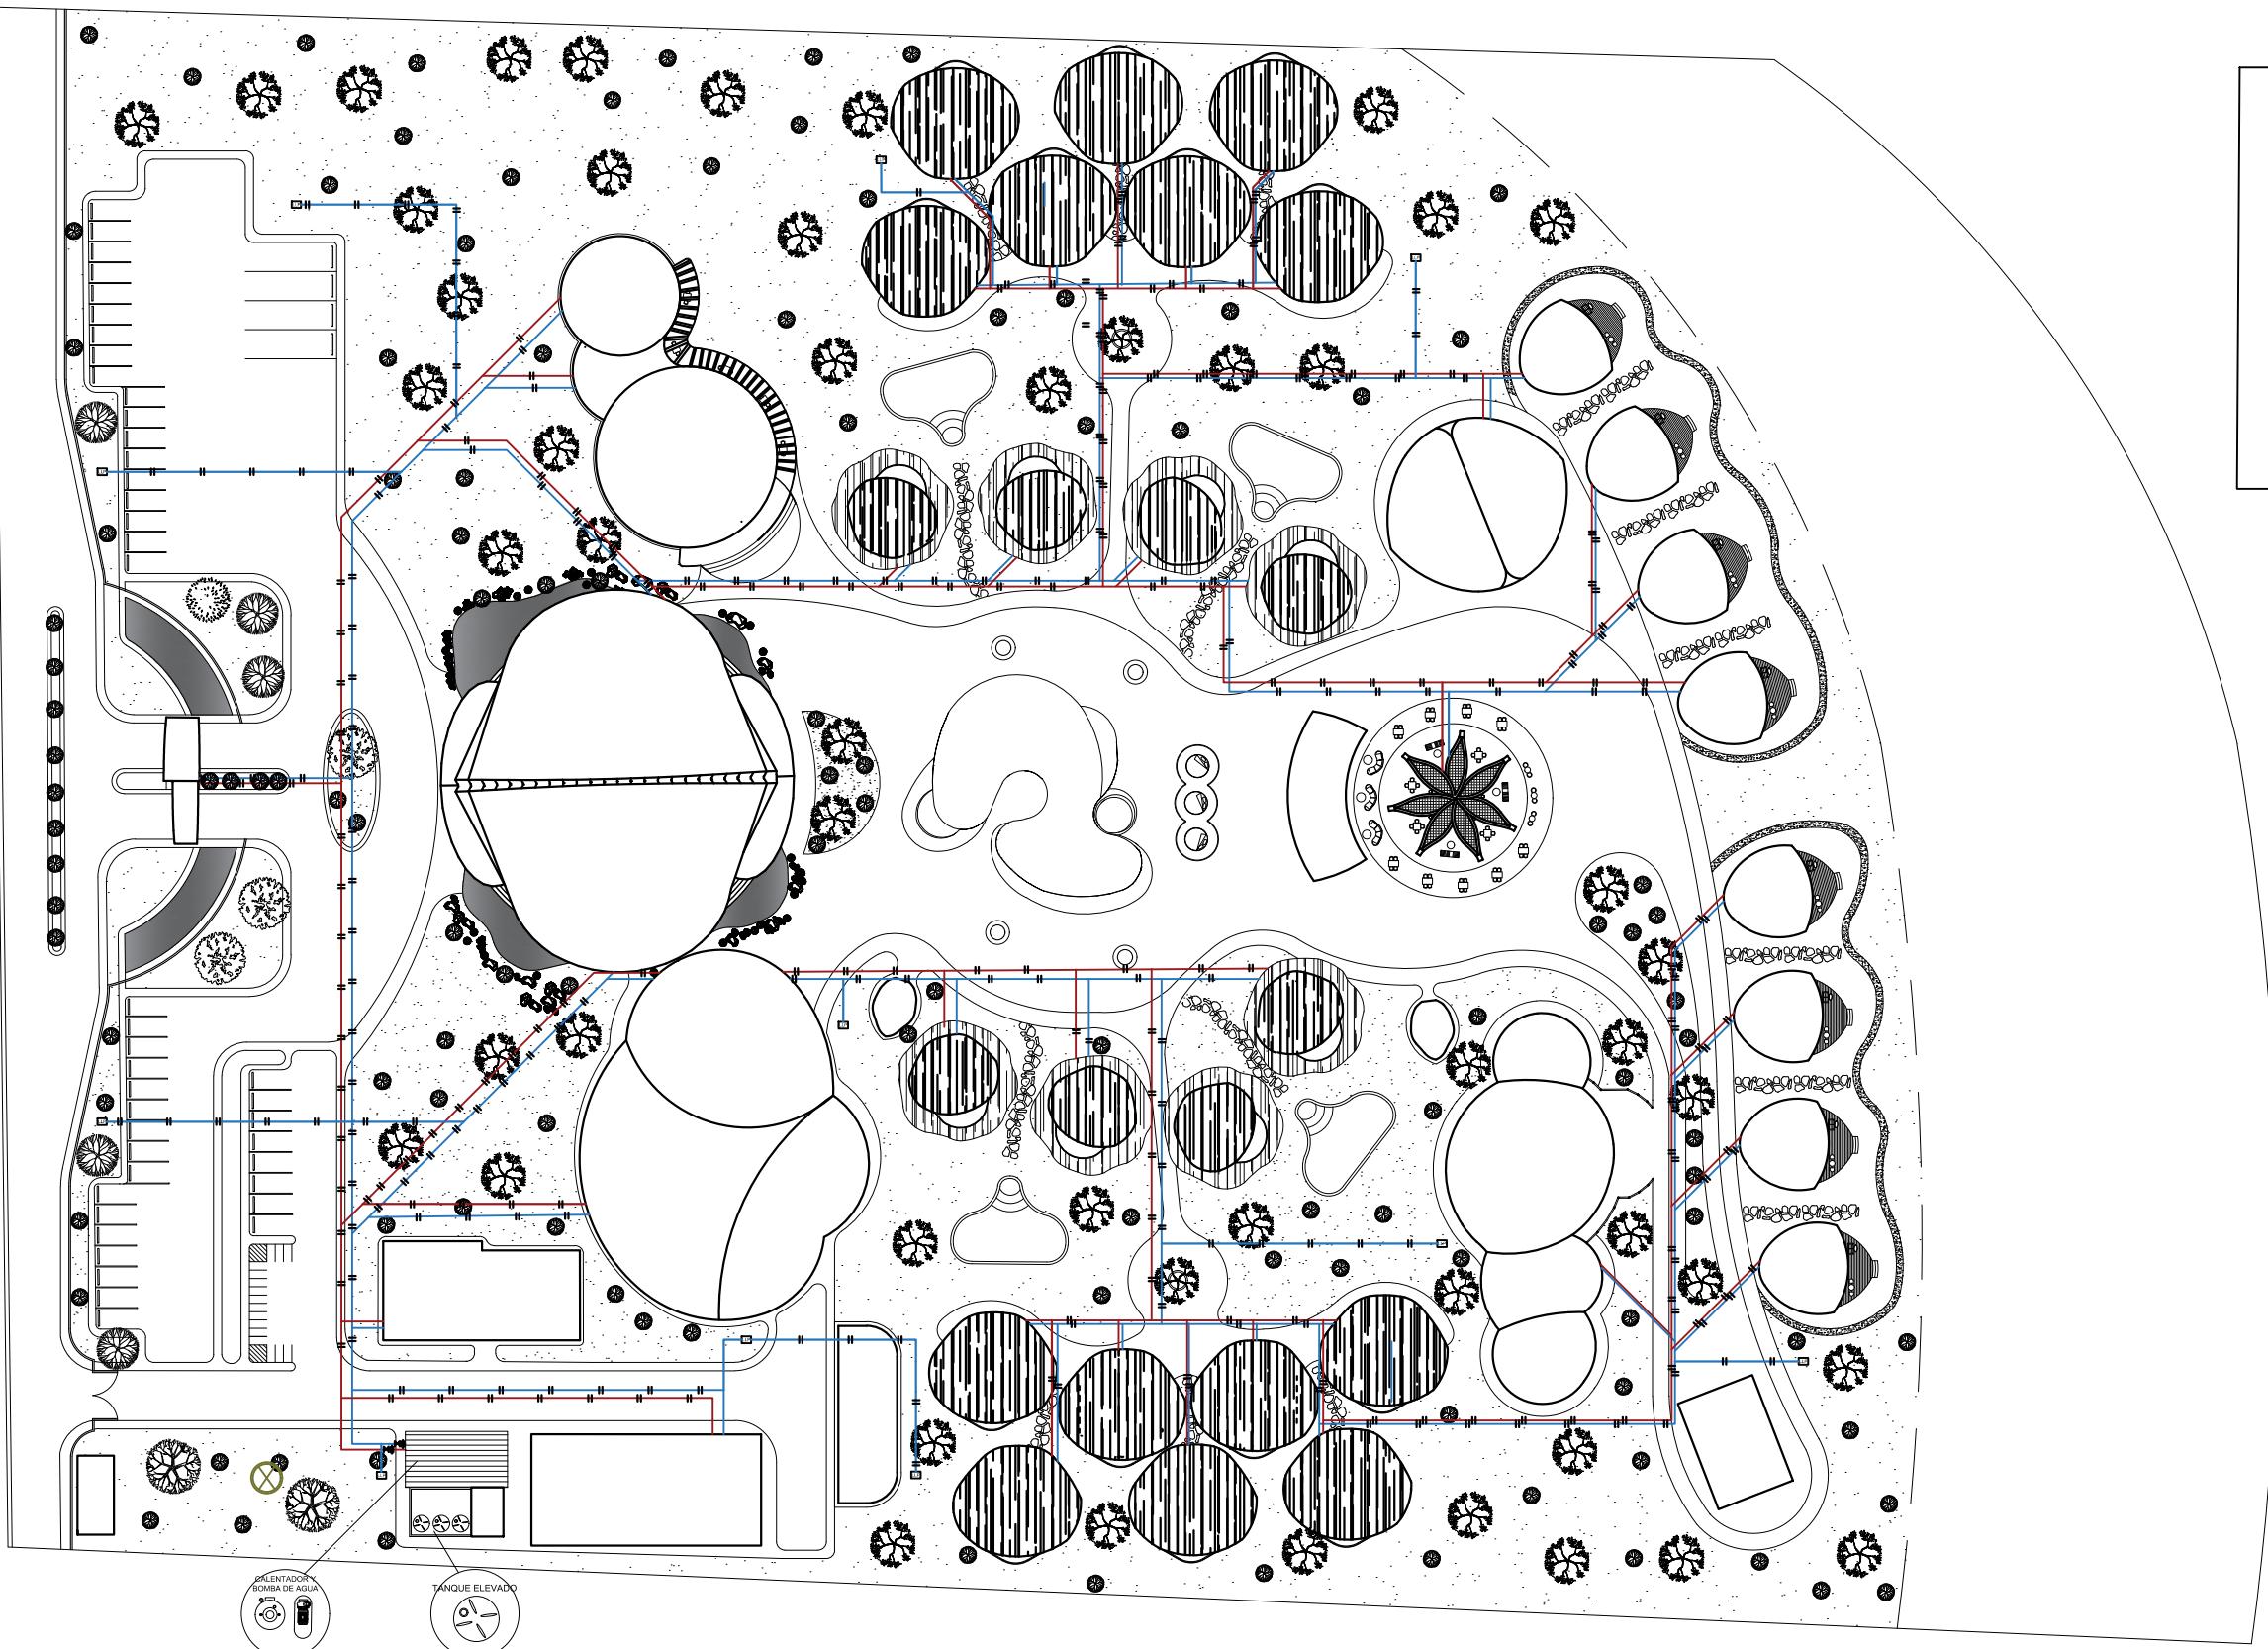

SIMBOLOGÍA

- RED DE AGUA FRÍA
- RED DE AGUA CALIENTE
- [LLP] LLAVE DE PILA
- || NUDO
- ||| ACOMETIDA
- ☒ UNIÓN UNIVERSAL

NOTAS

El suministro de agua proviene de un pozo tubular, pasando posteriormente por un sistema de filtración y purificación automatizado, el cual garantiza que el agua distribuida en todas las áreas cumpla con los estándares de calidad requeridos para su correcto uso.



FACULTAD DE INGENIERIA
ESCUELA DE ARQUITECTURA

ASIGNATURA

DISEÑO V

ESTUDIANTE

SONIA RODRIGUEZ
2022-0336
MARIA ISABEL GRULLON
2022-0599

DOCENTE

JOSE ALBERTO DE LA CRUZ

SEMESTRE

2-2025

PROYECTO

HOTEL BOUTIQUE

CONTENIDO


INDICADO


ESCALA

INDICADA

PAGINA

PTS02

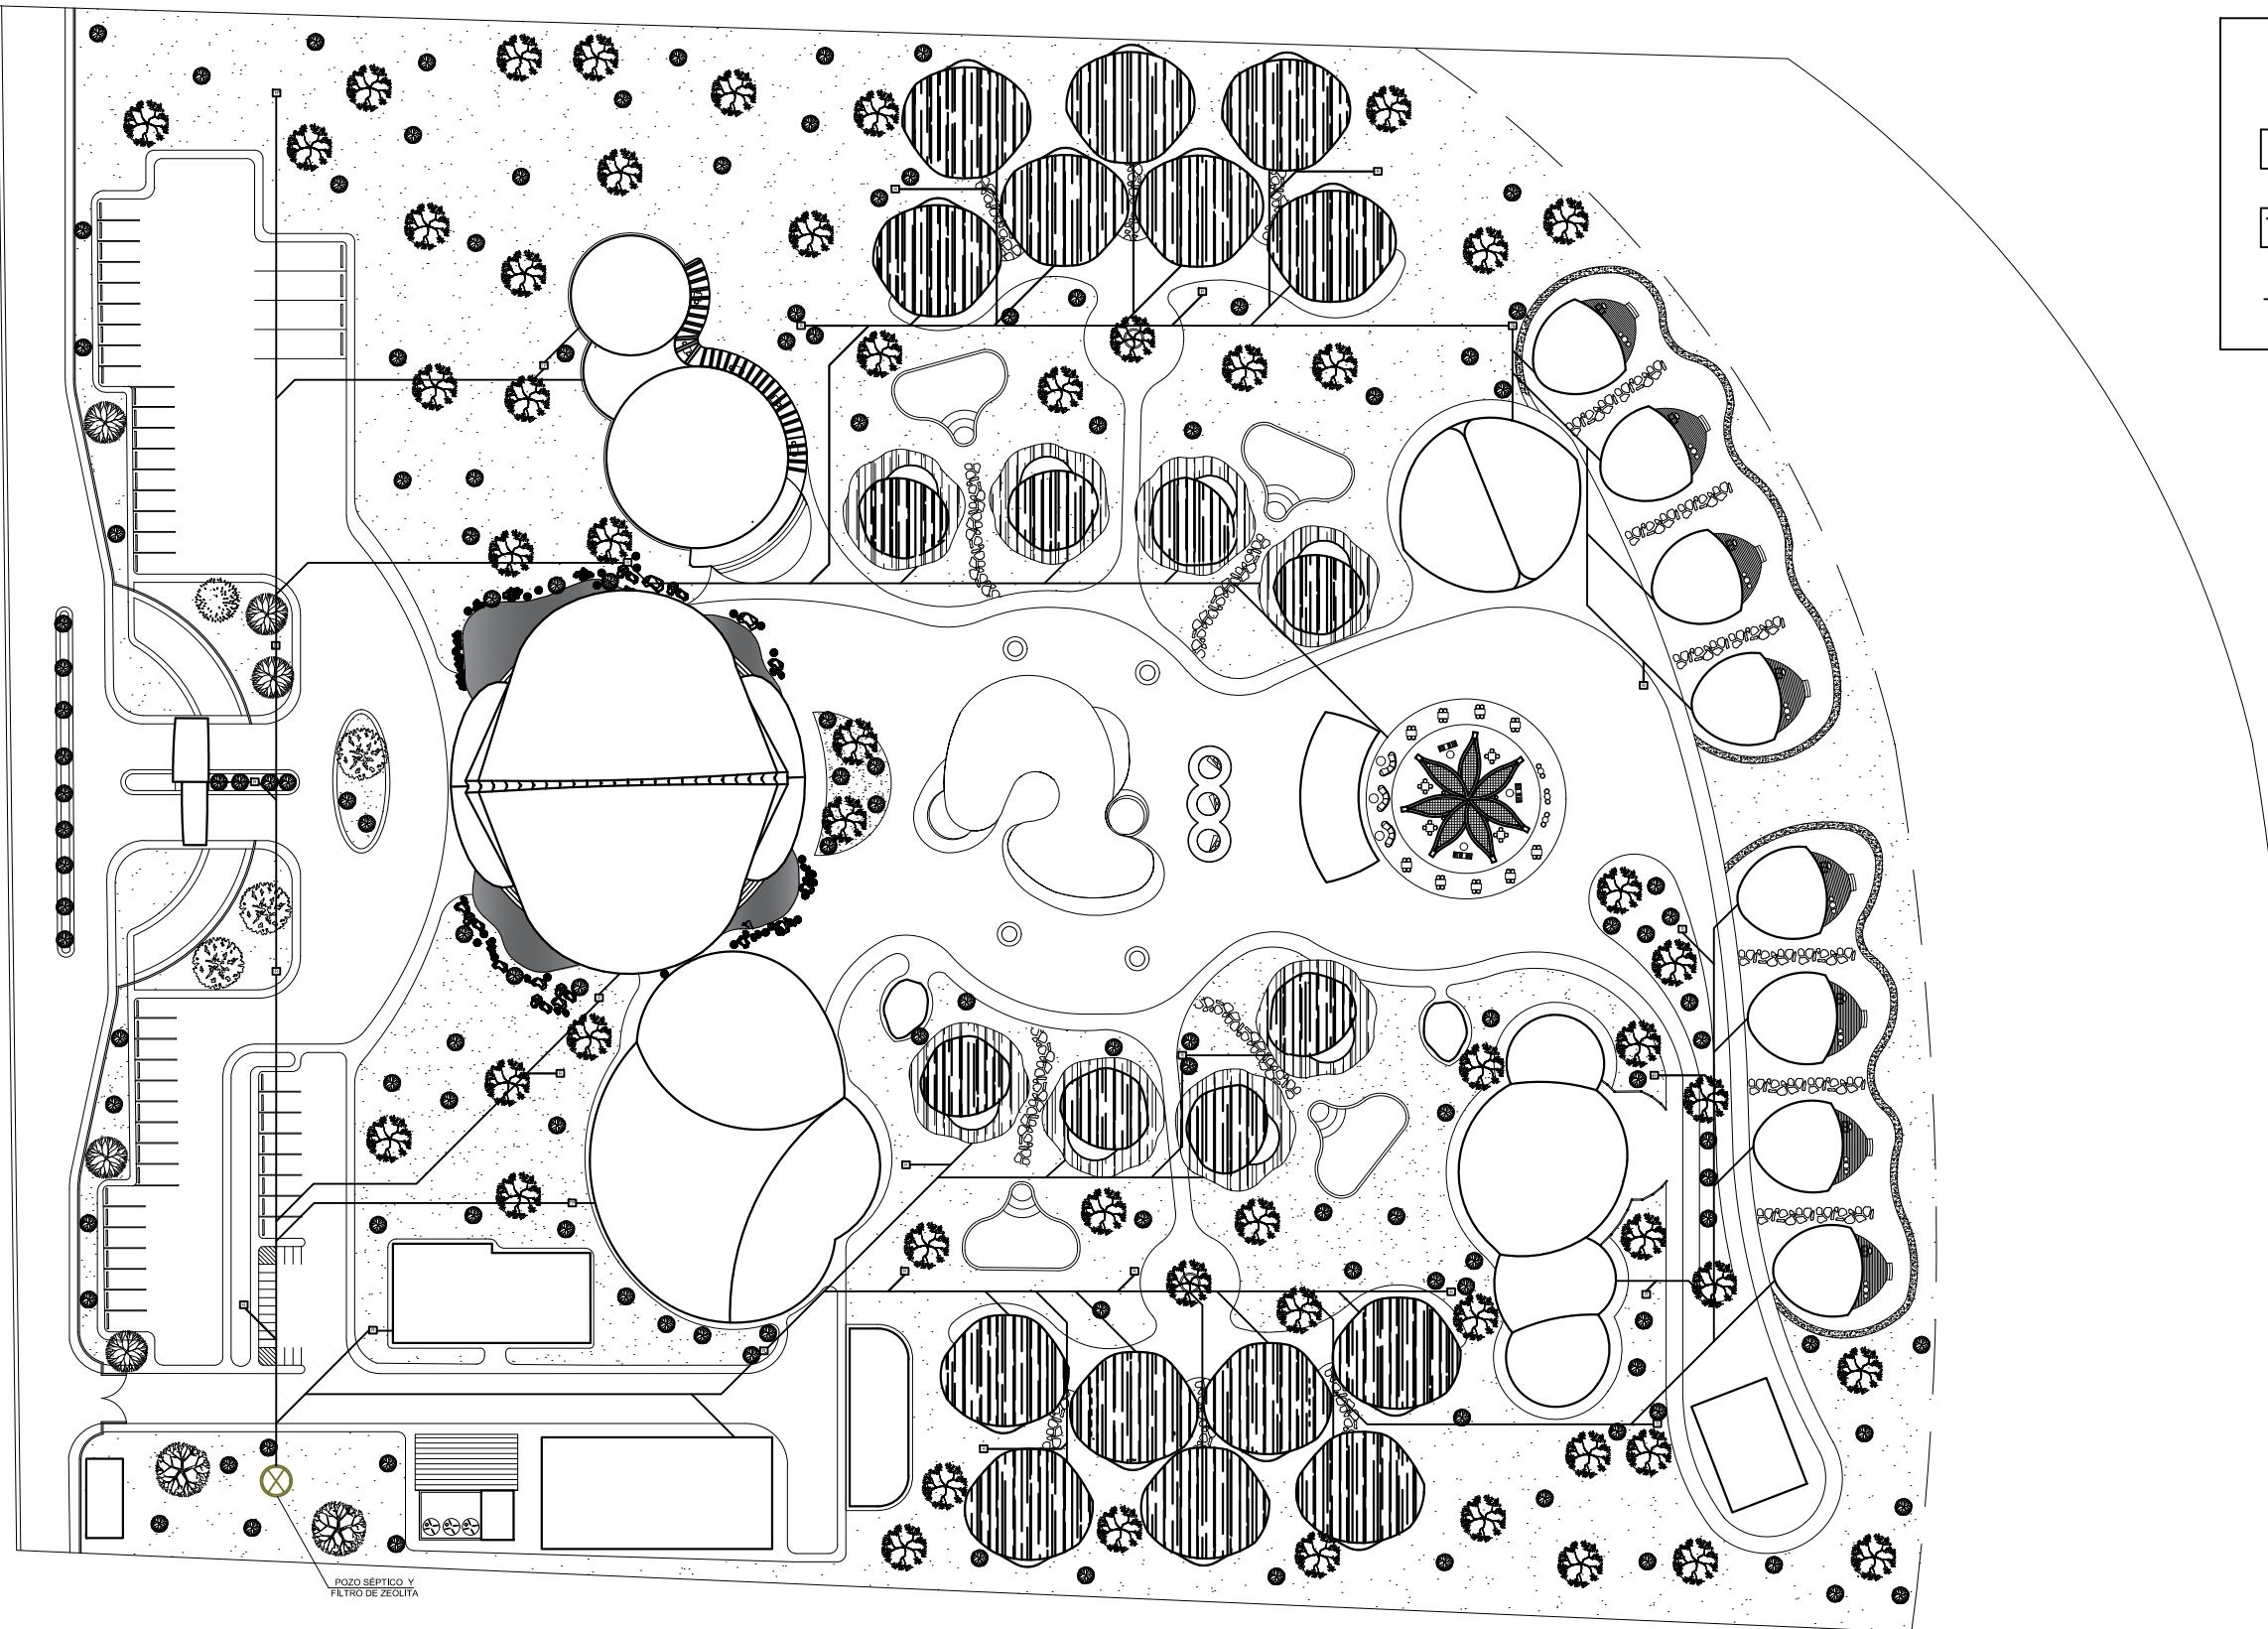

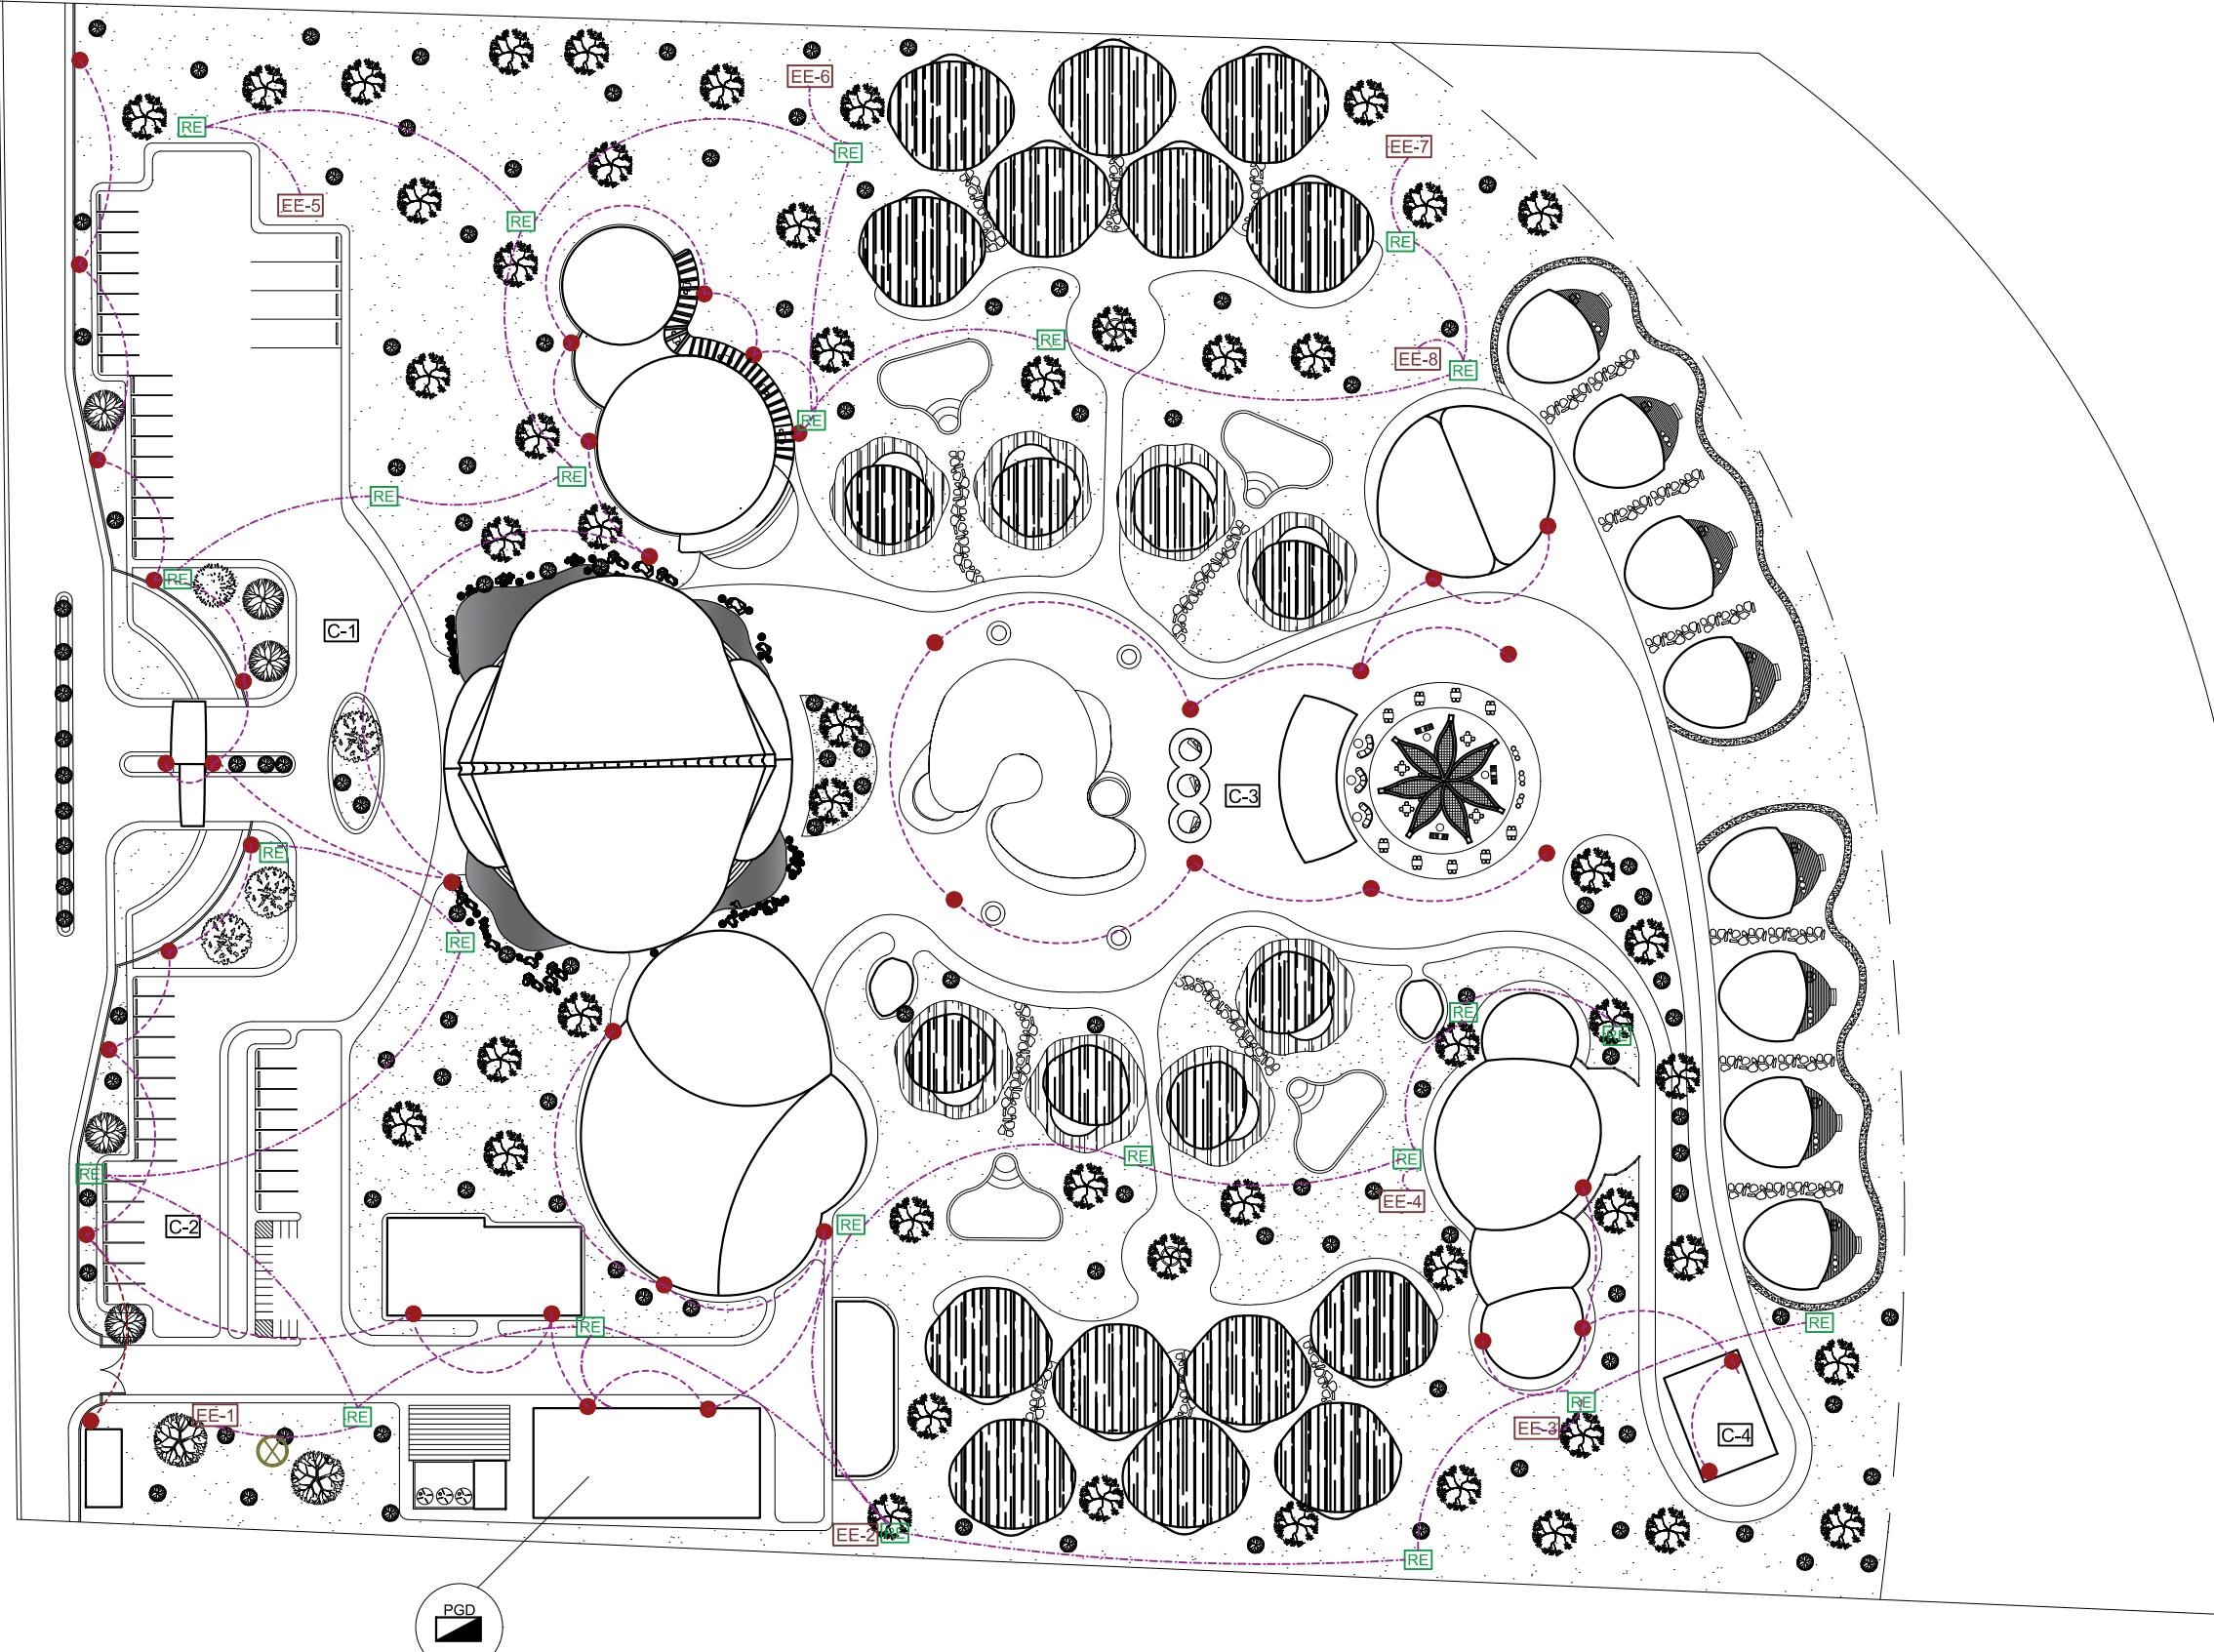


SIMBOLOGÍA

- TOMACORRIENTE 110V
- TUBERIA SOTERRADA
- [C#] CIRCUITO ELECTRICO

NOTAS

1. Todas las estaciones llegan al panel de control
2. Todos los tomacorrientes instalados en áreas exteriores deberán ser del tipo a prueba de intemperie, con cubierta de uso en operación y grado de protección mínimo IP44.
3. El panel de control se encuentra a 1.70 M sobre el NPT.
4. El metrocontador se encuentra a 1.90 sobre el NPT.
5. El circuito eléctrico #1 está conectado a la estación eléctrica 5.
6. El circuito eléctrico #2 está conectado a la estación eléctrica 1.
7. El circuito eléctrico #3 está conectado a la estación eléctrica 8.
8. El circuito eléctrico #4 está conectado a la estación eléctrica 3.

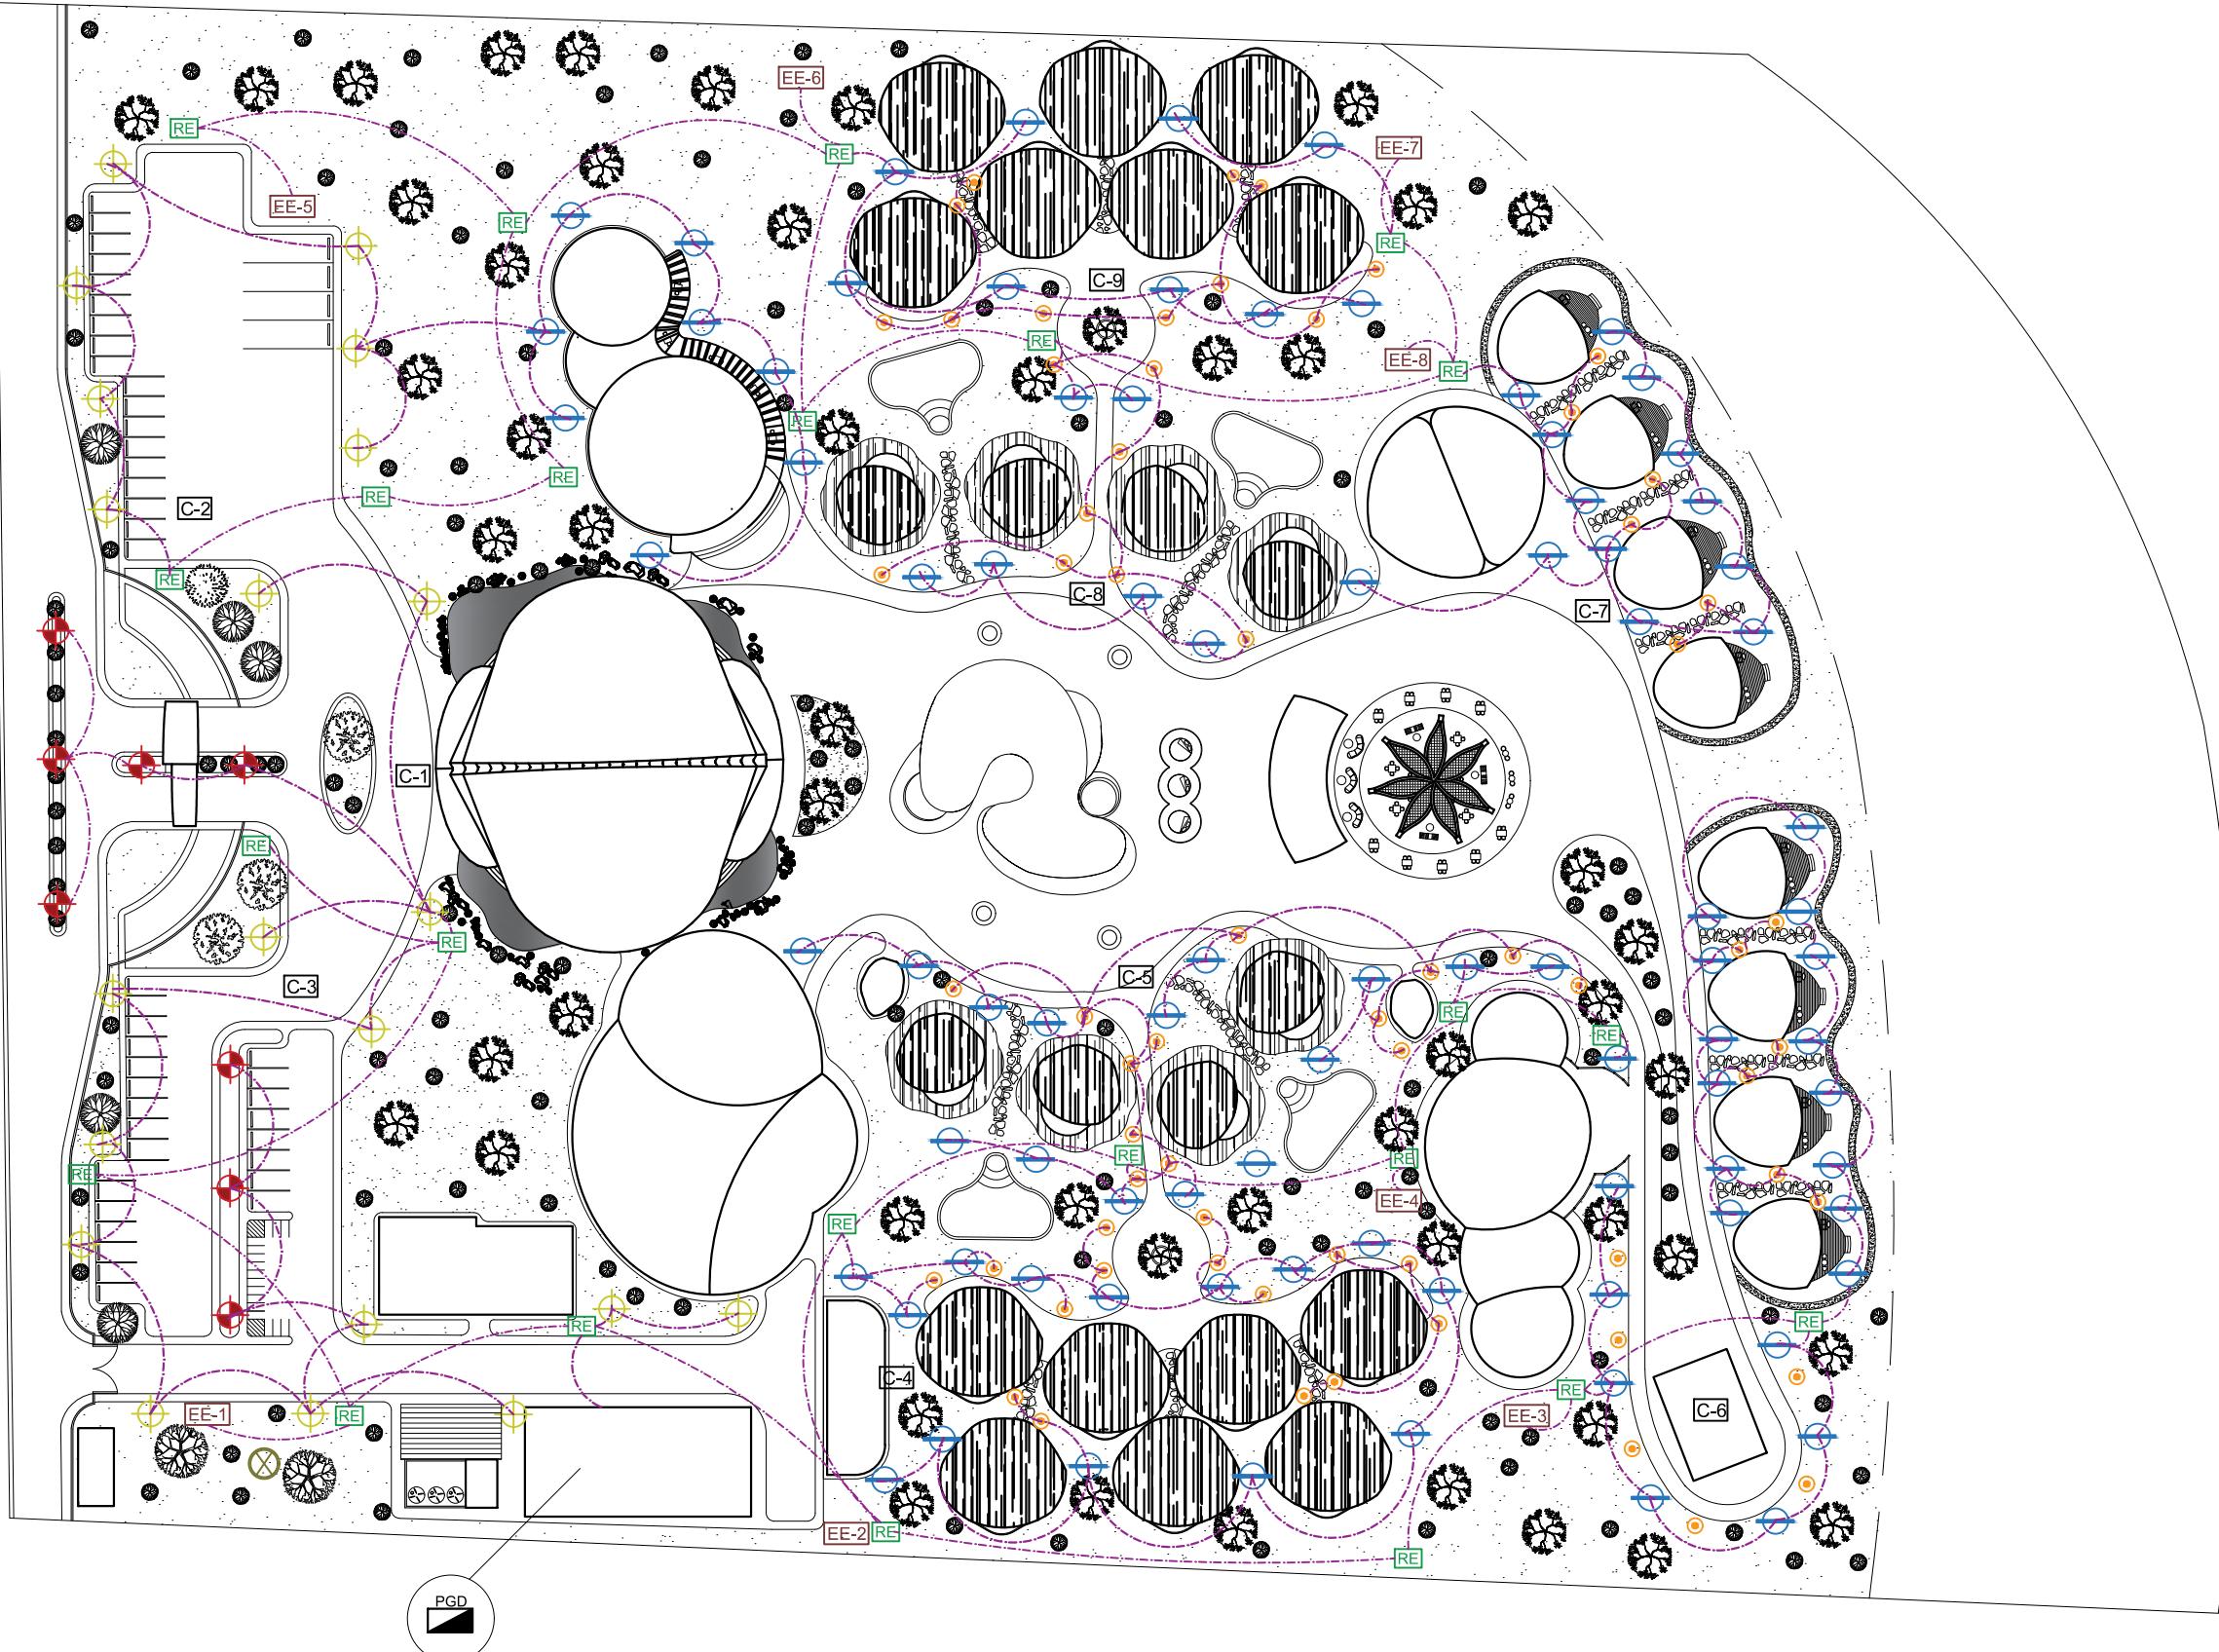

NOTAS

1. Todos los circuitos están conectados al panel general de control
2. El panel general de control está ubicado a 1.70 sobre el NPT.
3. Las luminarias de avenida se instalarán a una altura de 9.00 m sobre el NPT y tienen un diámetro de luminancia de 9m.
4. Las luminarias de boulevard se instalarán a una altura de 5.00 m sobre el NPT y tienen un diámetro de luminancia de 6m.
5. Las luminarias de jardín se instalarán a una altura de 0.50 m sobre el NPT y tienen un diámetro de luminancia de 1m.
6. En cada tramo de circuito de lumaria exterior pasan 2 conductores, retornos y un neutro.
7. Las Fases se encuentran en los registros
8. El circuito de luminarias #1 y #3 están conectados a la estación eléctrica 1.
9. El circuito de luminarias #2 está conectado a la estación eléctrica 5.
10. El circuito de luminarias #4 está conectado a la estación eléctrica 2.
11. El circuito de luminarias #5 está conectado a la estación eléctrica 4.
12. El circuito de luminarias #6 está conectado a la estación eléctrica 3.
13. El circuito de luminarias #7 está conectado a la estación eléctrica 8.
14. El circuito de luminarias #8 está conectado a la estación eléctrica 6.
15. El circuito de luminarias #9 está conectado a la estación eléctrica 7.



FACULTAD DE INGENIERIA
ESCUELA DE ARQUITECTURA

ASIGNATURA

DISEÑO V

ESTUDIANTE

SONIA RODRIGUEZ
2022-0336
MARIA ISABEL GRULLON
2022-0599

DOCENTE

JOSE ALBERTO DE LA CRUZ

SEMESTRE

2-2025

PROYECTO

HOTEL BOUTIQUE

CONTENIDO


INDICADO




ESCALA

INDICADA

PAGINA

PDC01

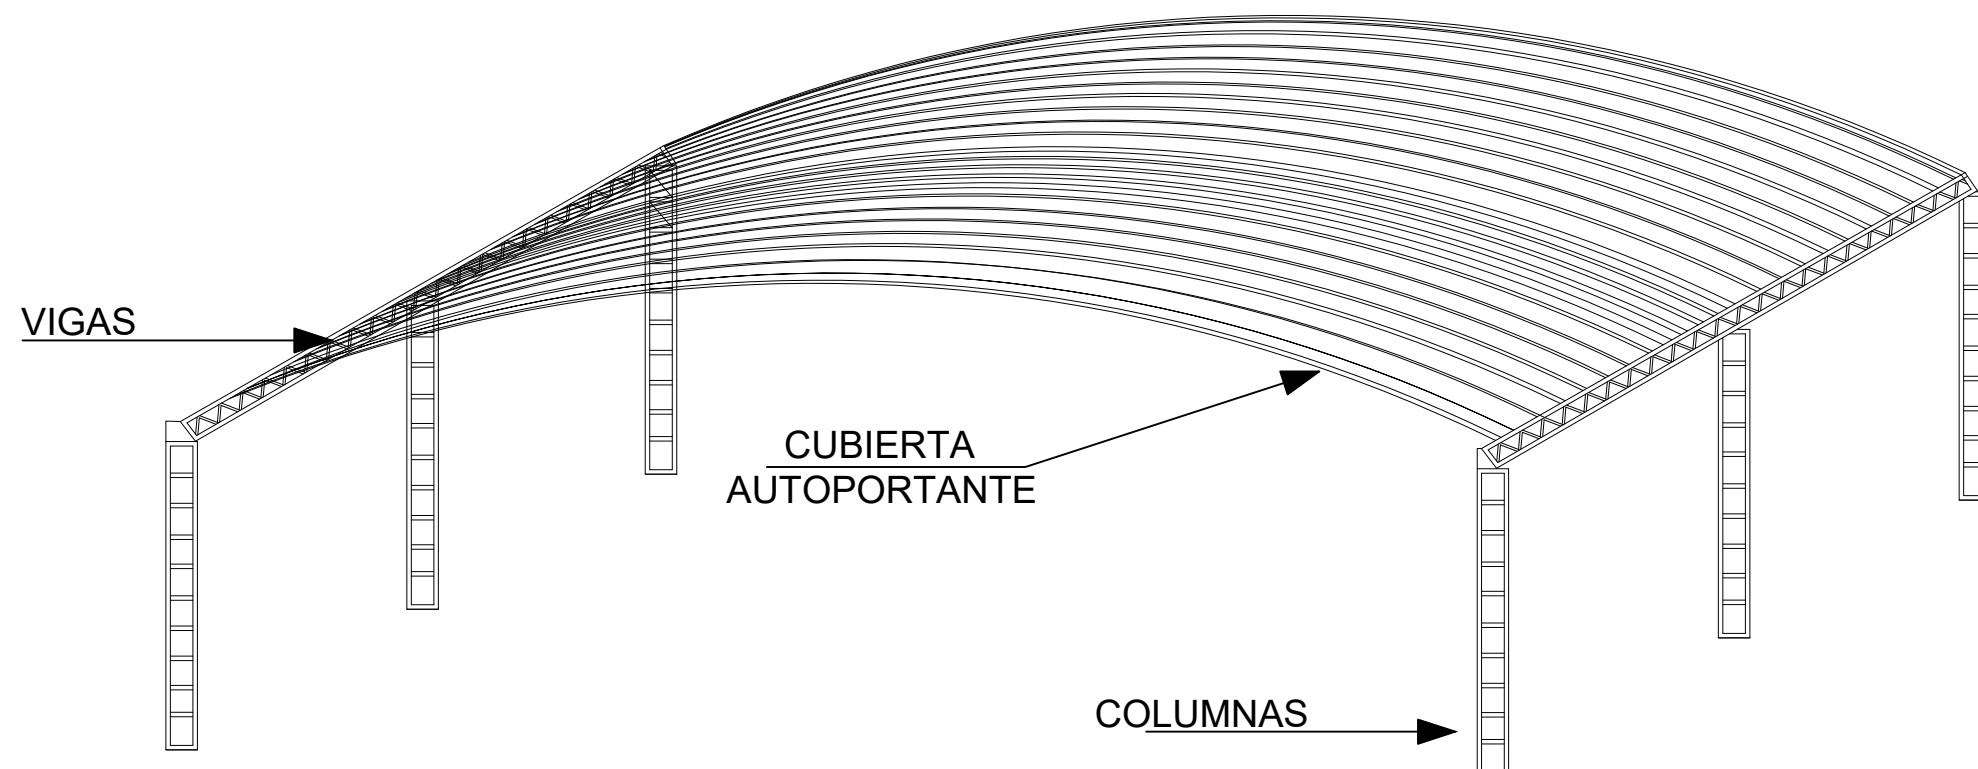

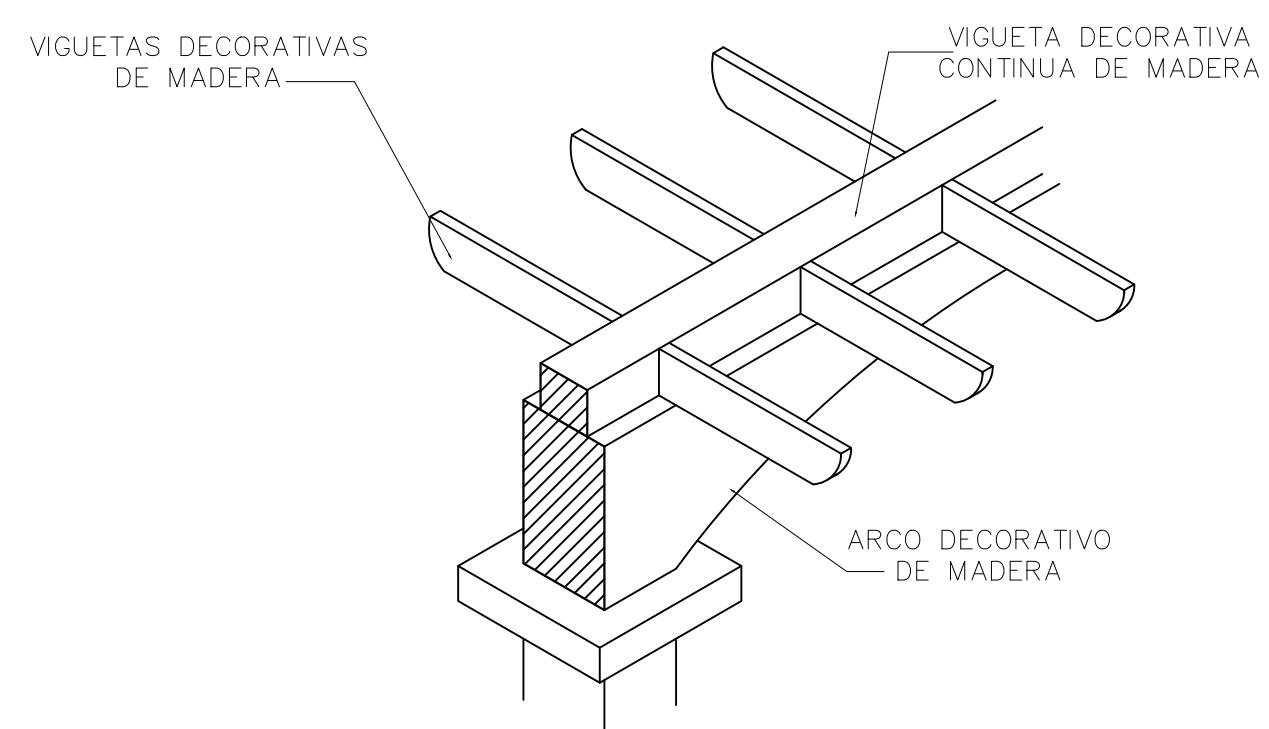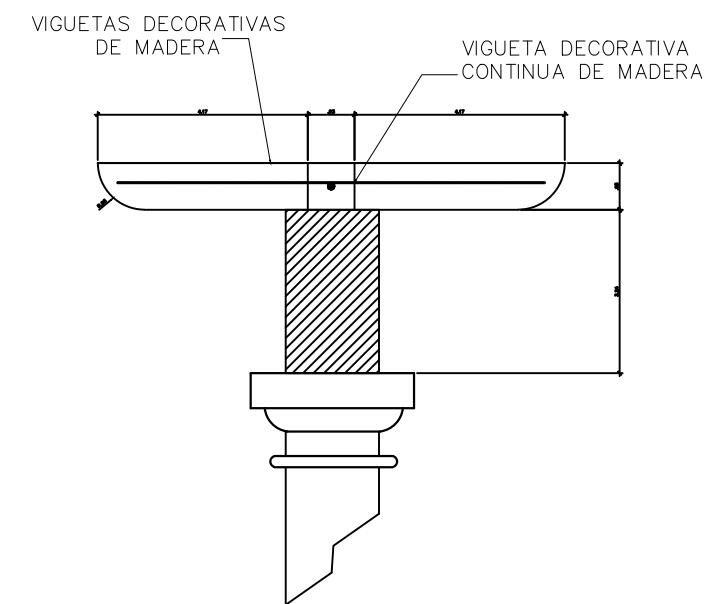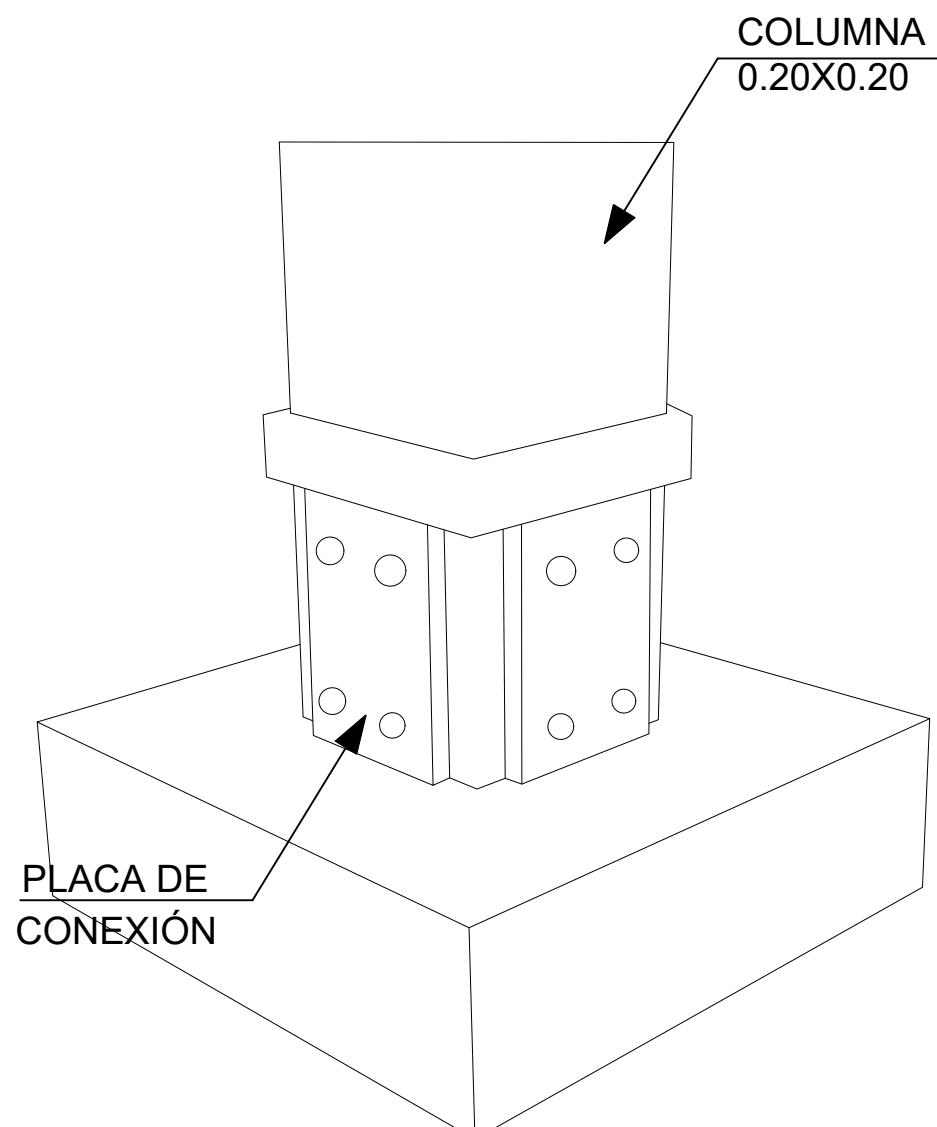

ASIGNATURA

DISEÑO V

ESTUDIANTE

SONIA RODRIGUEZ
2022-0336
MARIA ISABEL GRULLON
2022-0599

DOCENTE

JOSE ALBERTO DE LA CRUZ

SEMESTRE

2-2025

PROYECTO

HOTEL BOUTIQUE

CONTENIDO

INDICADO


ESCALA

INDICADA


PAGINA

PDC03

CAPTACION DE AGUA

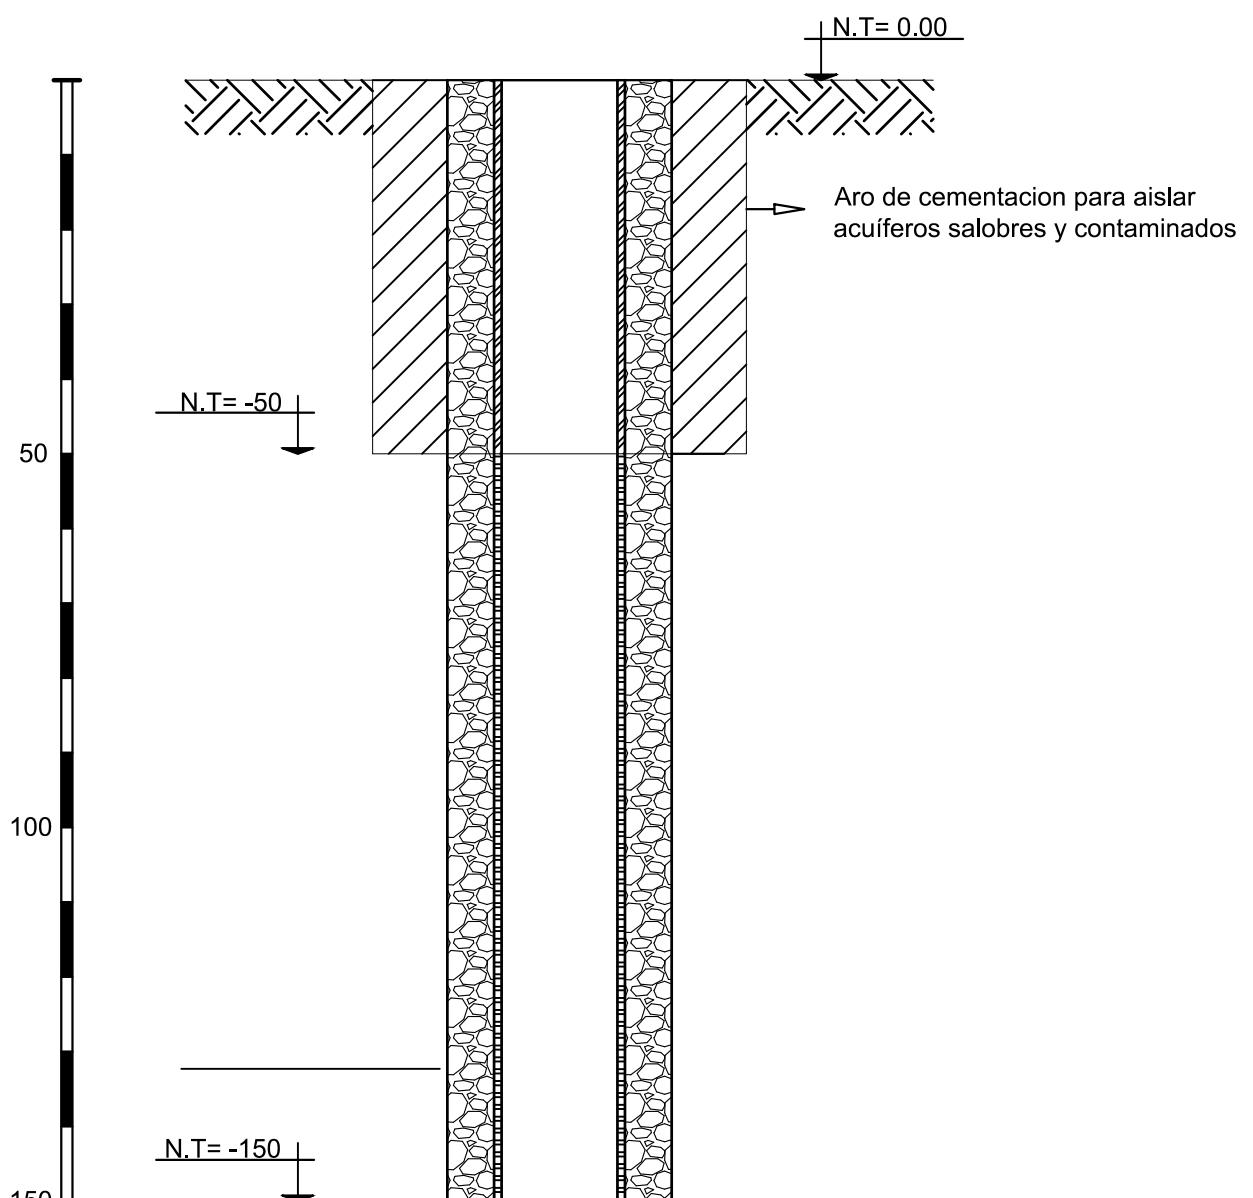

POZO SOTERRADO

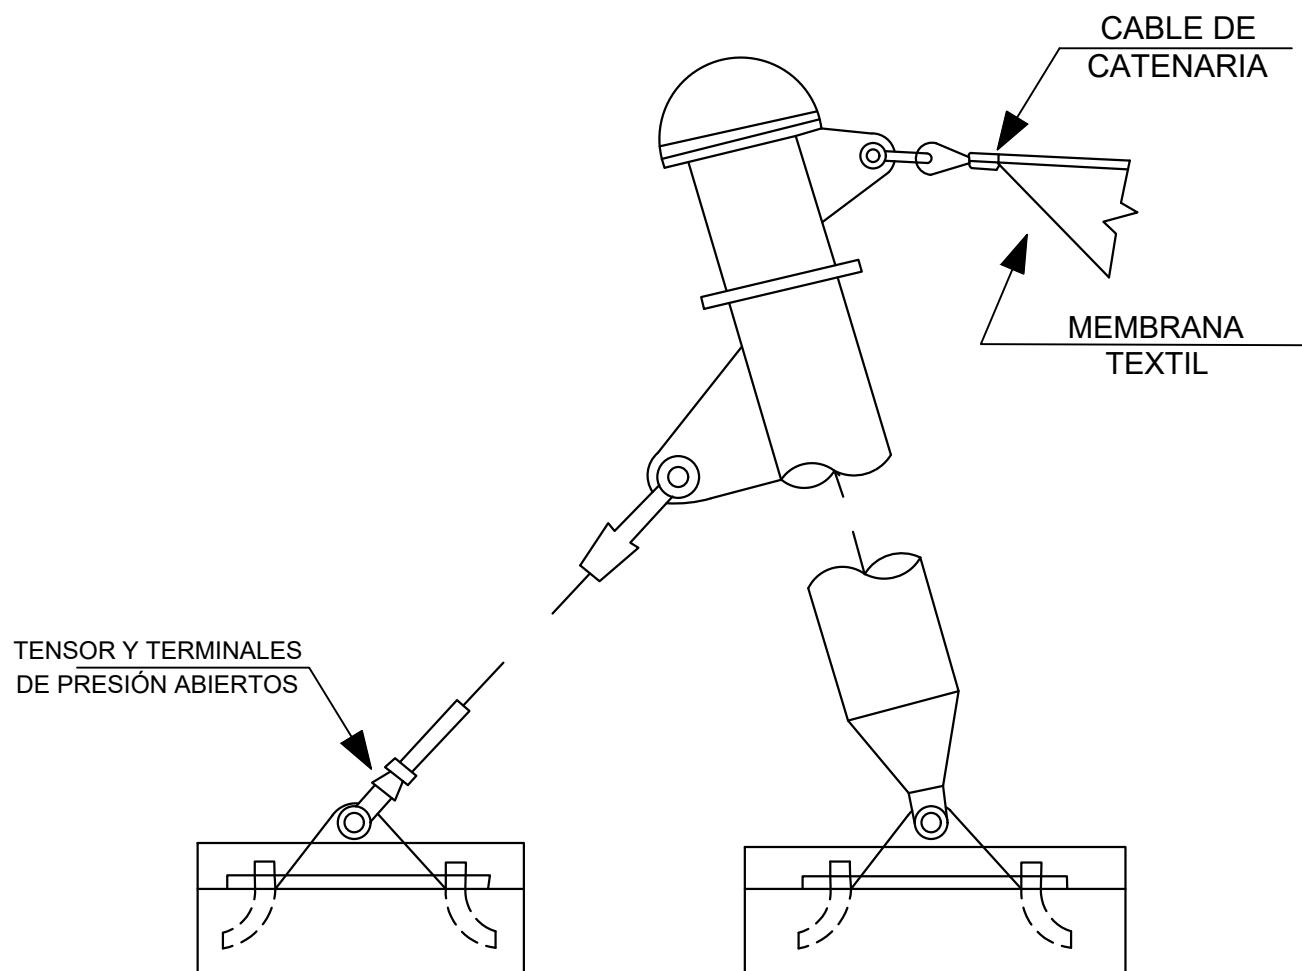

ASIGNATURA

DISEÑO V

ESTUDIANTE

SONIA RODRIGUEZ
2022-0336
MARIA ISABEL GRULLON
2022-0599

DOCENTE

JOSE ALBERTO DE LA CRUZ

SEMESTRE

2-2025

PROYECTO

HOTEL BOUTIQUE

CONTENIDO




INDICADO

ESCALA

INDICADA

PAGINA

PDC04

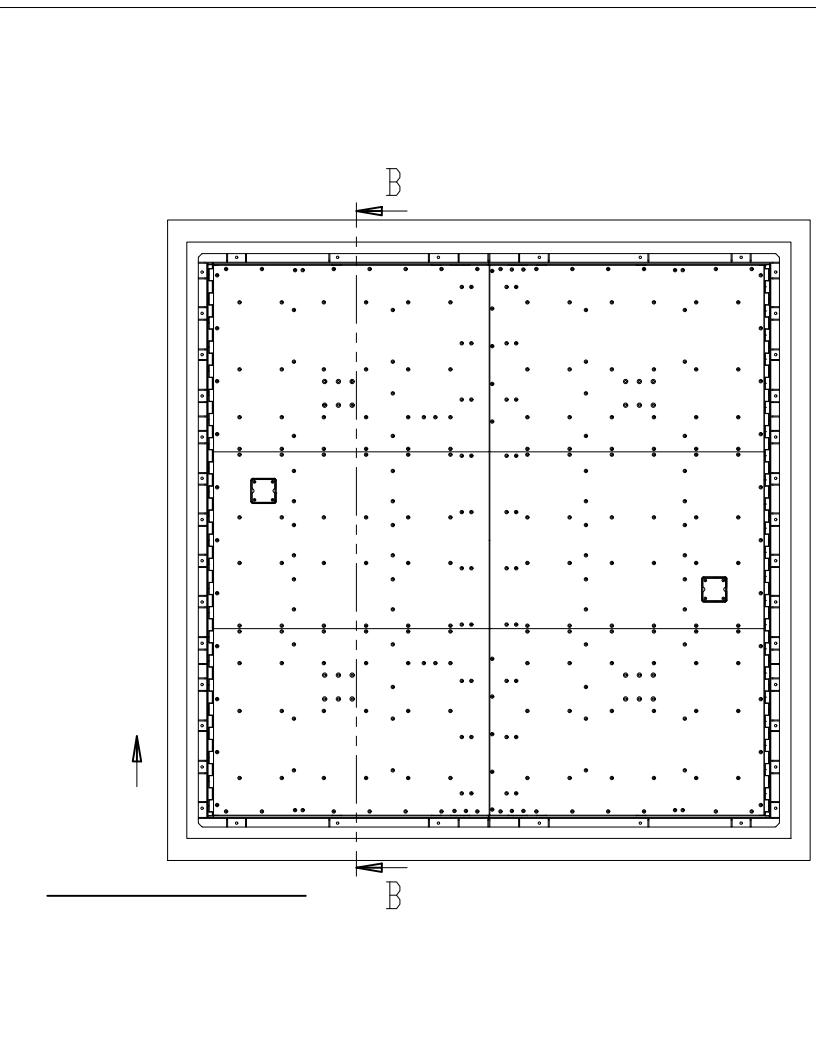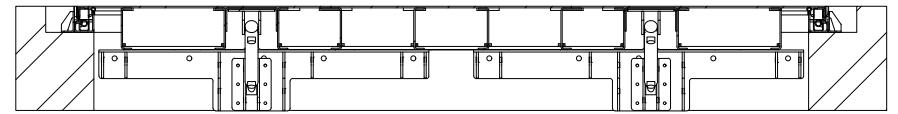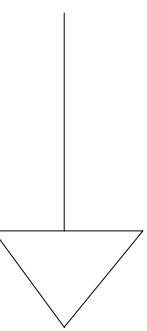

B-B
Vista de cerramiento

